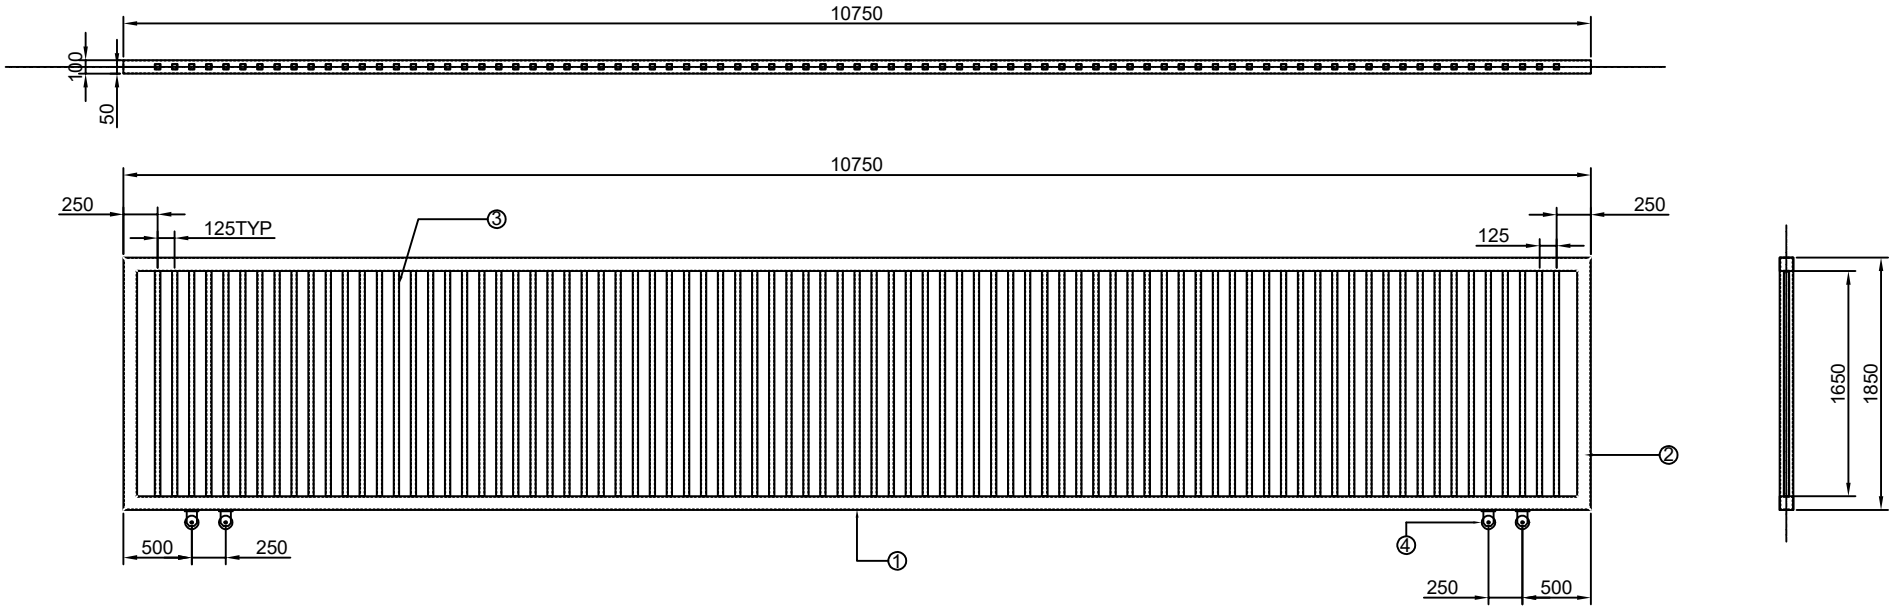


BOM			
SL NO.	DESCRIPTION	SPECIFICATION	QTY
1	MS SQ. TUBE	100X100X3.6X10750L	2NOS
2	MS SQ.TUBE	100X100X3.6X1850L	2NOS
3	MS SQ.TUBE	40X40X2.6X1650L	83NOS
4	WHEEL	4" STD WHEEL	4NOS
5	BRACKET	STD BKT	4NOS

This drawing & design is the property of NIHVA TECHNOLOGIES. Not to be sold or copied to any other concern.

TITLE:- MS Motorised Single Leaf Sliding Gate

	NAME	DATE	SIGN
DRAWN	SUJATA.B	16/10/2021	
CHECK	G.PATIL	16/10/2021	
APPRD.	A.KURHADE	16/10/2021	

If any queries contact : design@nihva.com

ALL DIMENSION ARE IN mm

NIHVA TECHNOLOGIES PVT. LTD.
NIHVA TECHNOLOGIES PVT. LTD. PUNE
Tel : 020 66304033
Email:- info@nihva.com
Website:- www.nihva.com

CLIENT - SCON PROJECTS


LOCATION -

PRODUCT - QTY:-01NO


DWG NO:-NIHVA\21-22\VDR\0251 REV- 0


SCALE: NTS SCALE:-- 1:1 SHEET: 01 OF 01

Rev No.	Revision	Date	Revised By

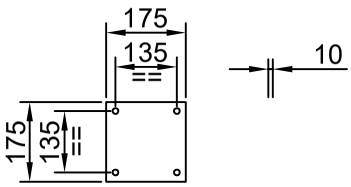

HINGE SUPPORT PLATE

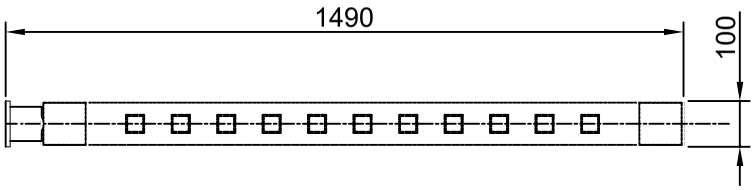

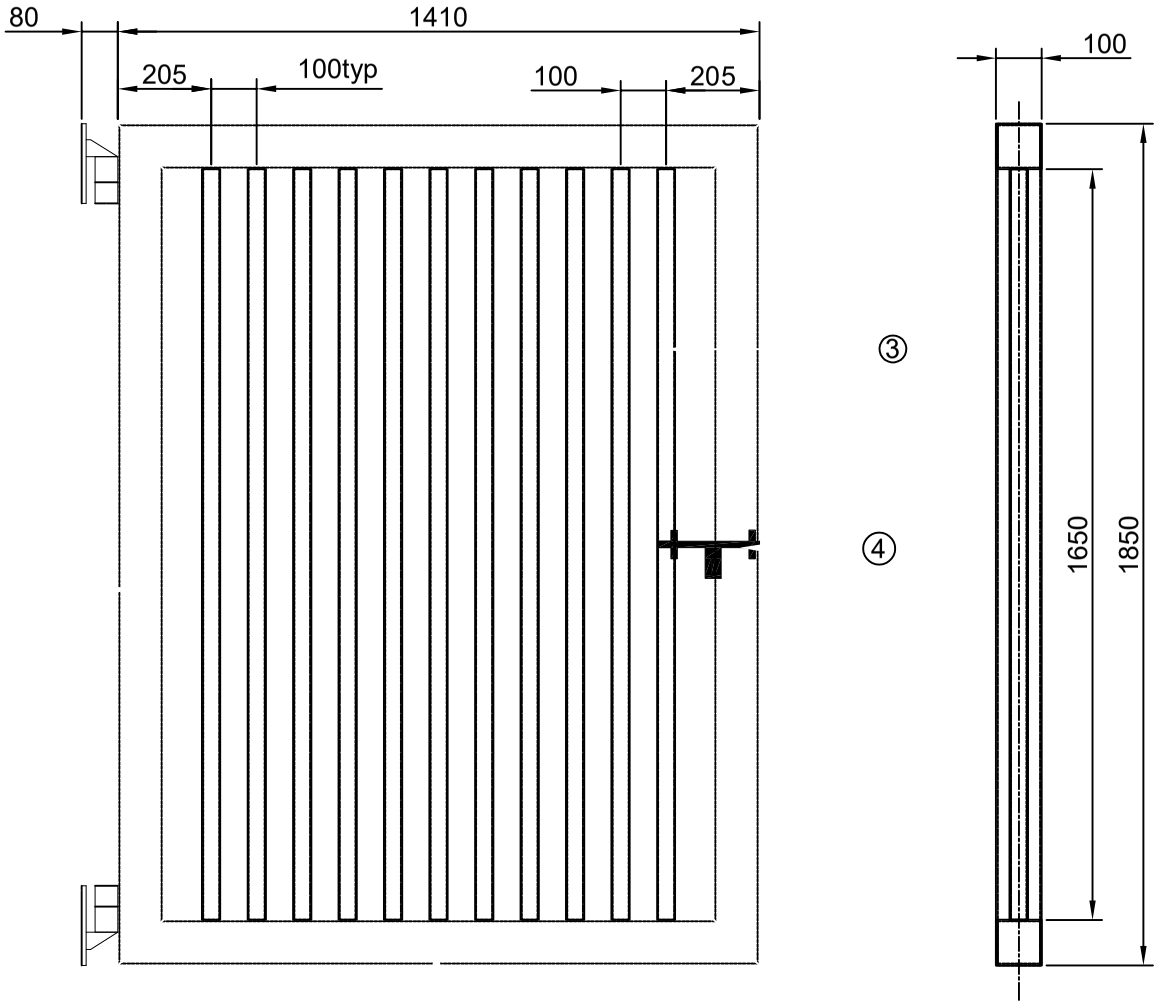

BOM FOR SINGLE POST			
SL NO.	DESCRIPTION	SPECIFICATION	QTY
1	MS SQ. TUBE	100X100X3.6X1850L	2NOS
2	MS SQ. TUBE	100X100X3.6X1410L	2NOS
3	MS SQ. TUBE	40X40X3.6X1650L	11NOS
4	LOCK	ALDROP	1NO
5	SUPPORT CHANNEL	ISMC 75 X 40, 70L	2NOS
6	HINGE	2" MANUAL HINGE	2NOS
7	HINGE SUPPORT PLATE	175X175X10THK	2NOS

This drawing & design is the property of NIHVA TECHNOLOGIES. Not to be sold or copied to any other concern.

TITLE:- WICKET GATE

NIHVA TECHNOLOGIES PVT. LTD.
NIHVA TECHNOLOGIES PVT. LTD. PUNE
Tel : 020 66304033
Email:- info@nihva.com
Website:- www.nihva.com

	NAME	DATE	SIGN
DRAWN	SUJATA.B	16/10/2021	
CHECK	G.PATIL	16/10/2021	
APPRD.	A.KURHADE	16/10/2021	

If any queries contact : design@nihva.com

ALL DIMENSION ARE IN mm

CLIENT -SCON PROJECTS


LOCATION -

PRODUCT - | QTY:-01NO


DWG NO:-NIHVA\21-22\VDR\0253 | REV- 0

SCALE: NTS | SCALE:-- 1:1 | SHEET: 01 OF 01


Rev No.	Revision	Date	Revised By

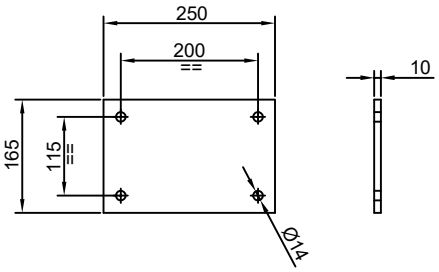

POST SUPPORT PLATE
THK : 10 MM
QTY : 8NOS

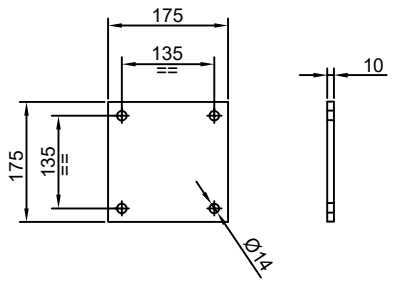

HINGE SUPPORT PLATE
THK : 10 MM
QTY : 2 NOS

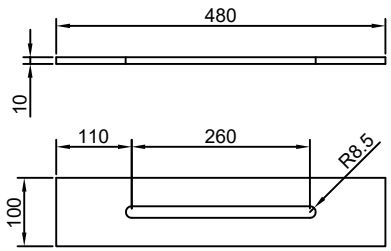

ROLLER SUPPORT PLATE
THK : 10 MM
QTY : 4 NOS

SR. NO.	DESCRIPTION	SPECIFICATION	QTY
1	HINGE SUPPORT PLATE	175 X 175 X 10 THK	2 NOS
2	ROLLER SUPPORT PLATE	480 X 100 X 10 THK	4 NOS
3	POST SUPPORT PLATE	250 X 165 X 10 THK	8 NOS

Rev No.	Revision	Date	Revised By

This drawing & design is the property of NIHVA TECHNOLOGIES. Not to be sold or copied to any other concern.


TITLE:- WICKET GATE FOUNDATION DRAWING

	NAME	DATE	SIGN
DRAWN	SUJATA.B	22/10/2021	
CHECK	G.PATIL	22/10/2021	
APPRD.	A.KURHADE	22/10/2021	

NIHVA TECHNOLOGIES PVT. LTD.
NIHVA TECHNOLOGIES PVT. LTD. PUNE
Tel : 020 66304033
Email:- info@nihva.com
Website:- www.nihva.com

CLIENT - SCON PROJECT
LOCATION -
PRODUCT - CUTTING PARTS

If any queries contact : design@nihva.com
DWG NO:-NIHVA\21-22\VDR\0254
REV- 0
ALL DIMENSION ARE IN mm
SCALE: NTS
SCALE:-- 1:1
SHEET: 01 OF 01

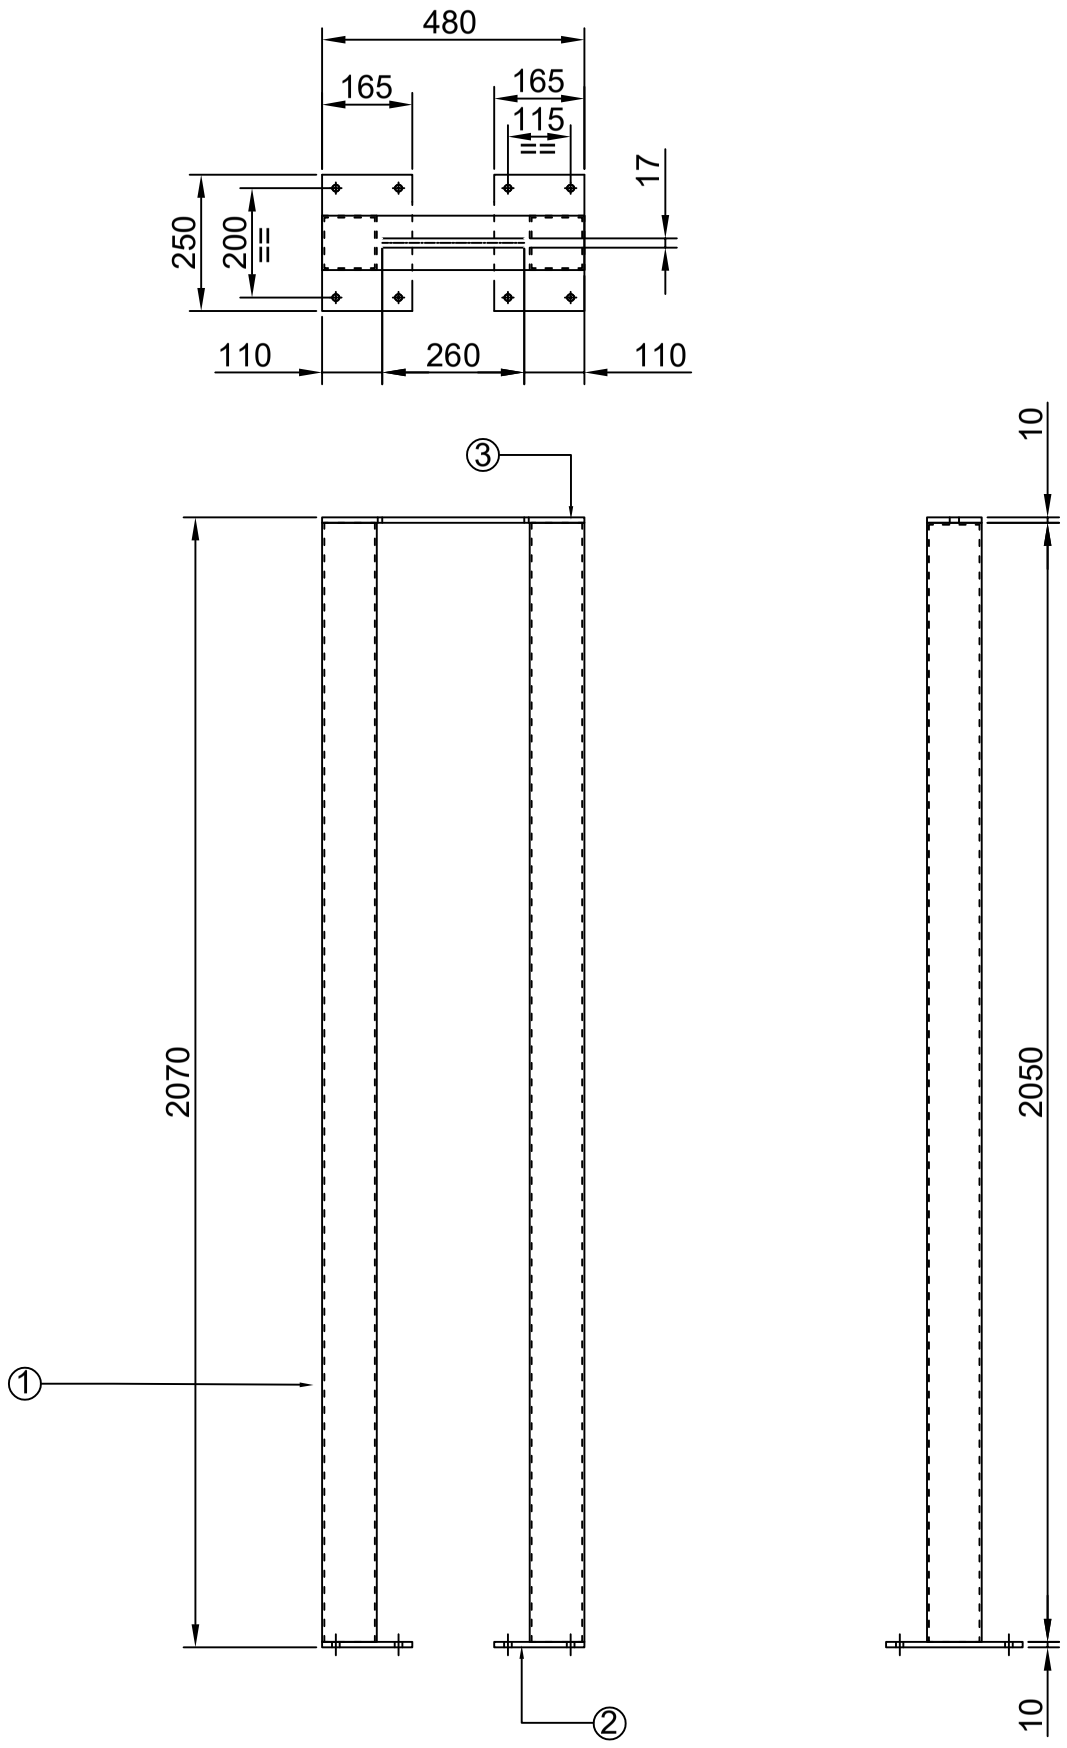

BOM FOR SINGLE POST			
SL NO.	DESCRIPTION	SPECIFICATION	QTY
1	MS SQ. TUBE	100X100X3.6X2050L	2NOS
2	POST SUPPORT PLATE	250X165X10THK	2NOS
3	ROLLER SUPPORT PLATE	480X100X10THK	1NO
4	ANCHOR BOLT	M12X150	8NOS

Rev No.	Revision	Date	Revised By

This drawing & design is the property of NIHVA TECHNOLOGIES. Not to be sold or copied to any other concern.

TITLE:- POST

	NAME	DATE	SIGN
DRAWN	SUJATA.B	16/10/2021	
CHECK	G.PATIL	16/10/2021	
APPRD.	A.KURHADE	16/10/2021	

If any queries contact : design@nihva.com

ALL DIMENSION ARE IN mm

NIHVA TECHNOLOGIES PVT. LTD.
NIHVA TECHNOLOGIES PVT. LTD. PUNE
Tel : 020 66304033
Email:- info@nihva.com
Website:- www.nihva.com

CLIENT - SCON PROJECT

LOCATION -

PRODUCT - | QTY:-2 NOS

DWG NO:-NIHVA\21-22\VDR\0252 | REV- 0

SCALE: NTS | SCALE:-- 1:1 | SHEET: 01 OF 01