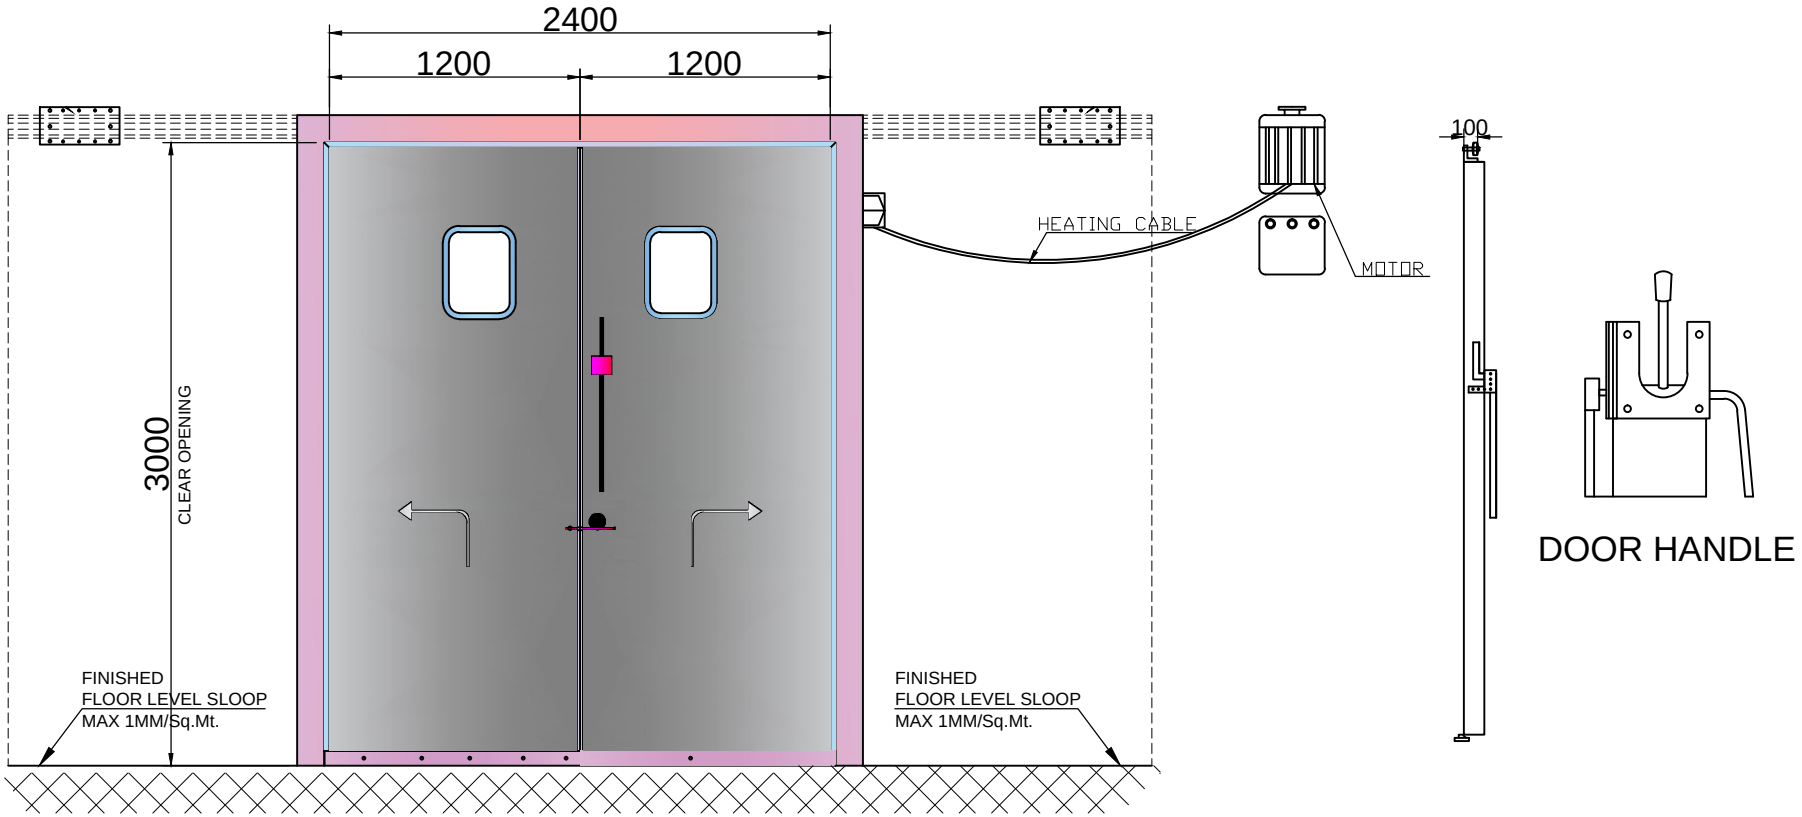


100MM DOUBLE LEAF SLIDING DOOR

1.AUTO MOTION SLIDING DOOR 100MM THICK
2.WITH PP/PP FOR BOTH SIDE,
3.SLIDING DOOR 2400X3000MM C.O.
(1200x1200 = 2 LEAFS) 2 NOS
4.DOOR WITH PPGI WALL FRAME (3 SIDED).
5.KEY LOCK, LOCK RELEASER SYSTEM,PADLOCK
6.HEATING CABLE REQUIRED

Sr. No.	Door Size (mm) (Wx H) Clear opening	QTY.		Automation	Heater	PPGI/SS	Vision Panel	Kick Plate	Door Thickness	Wall (Panel/Brick)	Wall thickness	RHS	LHS
		Sliding door	Hinged door										
1	(1200 + 1200) x 3000 mm	2	N/A	Yes	Yes	PP/PP	300 x 400 mm	N/A	100 mm	Panel	100	NA	NA
2	(1500 + 1500) x 3000 mm	2	N/A	Yes	Yes	PP/PP	300 x 400 mm	N/A	100 mm	Panel	100	NA	NA

TOLERANCE - ±10mm

This drawing & design is the property of NIHVA TECHNOLOGIES. Not to be sold or copied to any other concern.

TITLE: SLIDING DOOR

NIHVA TECHNOLOGIES PVT. LTD.
NIHVA TECHNOLOGIES PVT. LTD. PUNE
Tel : 020 66304033
Email:- info@nihva.com
Website:- www.nihva.com

	NAME	SIGN	DATE
DRAWN	P.V.A		25.02.19
CHECK	V.M.T		25.02.19
APPRD.			

CLIENT - DYNA FILTERS PVT. LTD.
PROJECT -
SITE LOCATION - PUNE
If any queries contact : design@nihva.com
DWG. NO. : NIHVA/18-19/0277
REV- 0
ALL DIMENSION ARE IN mm
SCALE:NTS
WT:
SHEET:01 OF 01