DWG.NO: SALT_1729_STR_13_R0

CUTTING DETAIL FOR 84.00M TRUSS

PartPos	Profile	No.	Material	Length	Net Weight(kg	Gross Weight(kg
M28	SHS72.0X72.0X3.2	6	IS2062	1930	12.47	74.82
M29	SHS72.0X72.0X3.2	10	IS2062	1947	12.57	125.7
M30	SHS72.0X72.0X3.2	1	IS2062	1350	9.05	9.05
M33	SHS150*4.5	1	IS2062	3728	76.61	76.61
M33	SHS150*4.5	1	IS2062	3728	76.62	76.62
M34	SHS150*4.5	1	IS2062	3616	74.32	74.32
M34	SHS150*4.5	1	IS2062	3617	74.33	74.33
M35	SHS150*4.5	1	IS2062	6467	132.93	132.93
M35	SHS150*4.5	2	IS2062	6467	132.94	265.88
M35	SHS150*4.5	1	IS2062	6468	132.95	132.95
M36	SHS150*4.5	1	IS2062	6579	135.22	135.22
M36	SHS150*4.5	1	IS2062	6579	135.23	135.23
M37	SHS150*4.5	1	IS2062	2815	57.87	57.87
M38	SHS150*4.5	8	IS2062	8174	168.05	1344.4
M39	SHS150*4.5	1	IS2062	4528	93.08	93.08
M40	SHS150*4.5	1	IS2062	4628	95.14	95.14
M42	SHS150*4.5	2	IS2062	6690	137.51	275.02
M52	SHS150*4.5	1	IS2062	22955	471.94	471.94
M53	SHS150*4.5	1	IS2062	3981	81.84	81.84
M54	SHS150*4.5	2	IS2062	1490	30.64	61.28
M55	SHS150*4.5	2	IS2062	3001	61.66	123.32
M56	SHS150*4.5	1	IS2062	35057	720.74	720.74
M57	SHS150*4.5	1	IS2062	4501	92.5	92.5
M58	SHS150*4.5	1	IS2062	3991	82.05	82.05
M59	SHS150*4.5	1	IS2062	22976	472.37	472.37
M60	SHS150*4.5	1	IS2062	35078	721.18	721.18
M61	SHS150*4.5	1	IS2062	4491	92.3	92.3
M64	SHS150.0X150.0X6.0	1	IS2062	1703	44.95	44.95
M65	SHS150.0X150.0X6.0	1	IS2062	8174	215.79	215.79
M66	SHS150.0X150.0X6.0	1	IS2062	1750	46.2	46.2
M67	SHS150.0X150.0X6.0	2	IS2062	1777	46.9	93.8
M68	SHS150.0X150.0X6.0	2	IS2062	2953	77.95	155.9
M72	SHS150.0X150.0X6.0	2	IS2062	1591	41.99	83.98
M73	SHS150.0X150.0X6.0	1	IS2062	1640	43.3	43.3
M73	SHS150.0X150.0X6.0	1	IS2062	1640	43.31	43.31
M78	SHS150.0X150.0X6.0	1	IS2062	8635	224.55	224.55
M79	SHS150.0X150.0X6.0	1	IS2062	8721	226.87	226.87
M81	SHS50*3.6	1	IS2062	1250	6.56	6.56
M83	SHS50*3.6	1	IS2062	1623	8.35	8.35
M84	SHS50*3.6	2	IS2062	2178	11.11	22.22
M85	SHS50*3.6	1	IS2062	1891	9.67	9.67
M86	SHS50*3.6	1	IS2062	1250	6.56	6.56
M89	SHS50*3.6	52	IS2062	1350	7.08	368.16
M98	SHS50*3.6	68	IS2062	1350	7.08	481.44
M99	SHS50*3.6	6	IS2062	1880	9.61	57.66
M100	SHS50*3.6	24	IS2062	1926	9.85	236.4
M101	SHS50*3.6	1	IS2062	1688	8.67	8.67
M102	SHS50*3.6	1	IS2062	1697	8.71	8.71
M103	SHS50*3.6	5	IS2062	1910	9.77	48.85
M104	SHS50*3.6	1	IS2062	1868	9.56	9.56
M105	SHS50*3.6	4	IS2062	1884	9.64	38.56
M106	SHS50*3.6	1	IS2062	1796	9.2	9.2
M107	SHS50*3.6	1	IS2062	2010	10.27	10.27
M108	SHS50*3.6	1	IS2062	2017	10.3	10.3
M109	SHS50*3.6	1	IS2062	1802	9.23	9.23
M110	SHS50*3.6	1	IS2062	1852	9.48	9.48
M111	SHS50*3.6	1	IS2062	1893	9.69	9.69
M112	SHS50*3.6	1	IS2062	2096	10.7	10.7
M113	SHS50*3.6	1	IS2062	1767	9.06	9.06
M114	SHS50*3.6	8	IS2062	1320	6.92	55.36
M115	SHS50*3.6	13	IS2062	1250	6.56	85.28
M116	SHS50*3.6	2	IS2062	1350	7.08	14.16
M123	SHS220*8	1	IS2062	8660	451.46	451.46
M127	SHS150*8	2	IS2062	1330	47.34	94.68
M128	SHS150*8	4	IS2062	1330	46.38	185.52
M141	SHS150*8	1	IS2062	4371	152.58	152.58
M143	SHS150*8	1	IS2062	3821	134.3	134.3
M144	SHS150*8	1	IS2062	3772	132.94	132.94
M146	SHS150*8	1	IS2062	6398	228.18	228.18
M146	SHS150*8	1	IS2062	6399	228.2	228.2
M149	SHS150*8	1	IS2062	2953	105.32	105.32
M150	SHS150*8	1	IS2062	1777	63.37	63.37
M159	SHS150*8	2	IS2062	2891	103.11	206.22
M160	SHS150*8	2	IS2062	1240	44.24	88.48
M161	SHS150*8	2	IS2062	5138	183.26	366.52
M162	SHS150*8	2	IS2062	5169	184.36	368.72
M163	SHS150*8	1	IS2062	1350	48.16	48.16
M172	SHS180.0X180.0X6.0	1	IS2062	8661	272.64	272.64
M173	SHS180.0X180.0X6.0	1	IS2062	8745	275.43	275.43
M174	SHS180.0X180.0X6.0	1	IS2062	8819	277.88	277.88
M175	SHS180.0X180.0X6.0	1	IS2062	8627	271.59	271.59
M177	SHS180.0X180.0X6.0	4	IS2062	10739	335.01	1340.04
M178	SHS180.0X180.0X6.0	2	IS2062	10476	326.71	653.42
M179	SHS180.0X180.0X6.0	1	IS2062	3781	119.41	119.41
M181	SHS180.0X180.0X6.0	1	IS2062	2953	94.64	94.64
M192	SHS72*5	6	IS2062	2131	21.55	129.3
M193	SHS180.0X180.0X5.0	1	IS2062	3851	104.56	104.56
M194	SHS180.0X180.0X5.0	1	IS2062	3840	104.25	104.25
M194	SHS180.0X180.0X5.0	1	IS2062	3840	104.25	104.25
M195	SHS180.0X180.0X5.0	1	IS2062	3951	107.28	107.28
M196	SHS180.0X180.0X5.0	2	IS2062	7139	193.87	387.74
M200	SHS72.0X72.0X3.2	1	IS2062	1933	12.48	12.48
M201	SHS72.0X72.0X3.2	1	IS2062	1887	12.18	12.18
M202	SHS72.0X72.0X3.2	4	IS2062	1900	12.27	49.08
M203	SHS72.0X72.0X3.2	6	IS2062	1947	12.57	75.42
M204	SHS72.0X72.0X3.2	1	IS2062	1930	12.47	12.47
M205	SHS72.0X72.0X3.2	1	IS2062	1884	12.17	12.17
M206	SHS72.0X72.0X3.2	2	IS2062	1350	9.05	18.1
M207	SHS72.0X72.0X3.2	1	IS2062	2049	13.21	13.21
M208	SHS72.0X72.0X3.2	1	IS2062	2795	17.89	17.89
M209	SHS72.0X72.0X3.2	1	IS2062	2579	16.53	16.53
M210	SHS72.0X72.0X3.2	1	IS2062	1997	12.88	12.88
M211	SHS72.0X72.0X3.2	2	IS2062	2168	13.95	27.9
M212	SHS72.0X72.0X3.2	1	IS2062	1895	12.25	12.25
M213	SHS100.0X100.0X6.0	1	IS2062	3834	64.4	64.4
M214	SHS100.0X100.0X6.0	32	IS2062	1350	22.92	733.44
M216	SHS100.0X100.0X6.0	1	IS2062	1737	28.21	28.21
M217	SHS100.0X100.0X6.0	1	IS2062	1842	29.79	29.79
M218	SHS100.0X100.0X6.0	1	IS2062	2243	35.94	35.94
M219	SHS100.0X100.0X6.0	1	IS2062	1868	30.19	30.19
M221	SHS100.0X100.0X6.0	1	IS2062	1350	22.92	22.92
M235	SHS100.0X100.0X6.0	1	IS2062	2265	36.21	36.21
M236	SHS100.0X100.0X6.0	1	IS2062	2208	35.41	35.41
M237	SHS100.0X100.0X6.0	2	IS2062	2780	44.27	88.54
M238	SHS100.0X100.0X6.0	1	IS2062	2540	40.54	40.54
M239	SHS100.0X100.0X6.0	1	IS2062	2722	43.28	43.28
M240	SHS100.0X100.0X6.0	2	IS2062	2081	33.2	66.4
M241	SHS100.0X100.0X6.0	1	IS2062	1817	29.17	29.17
M242	SHS100.0X100.0X6.0	1	IS2062	1990	32.05	32.05
M243	SHS100.0X100.0X6.0	2	IS2062	2163	34.71	69.42
M244	SHS100.0X100.0X6.0	1	IS2062	1887	30.48	30.48
M250	SHS72*5	1	IS2062	2111	21.36	21.36
M255	SHS72*5	1	IS2062	3457	34.67	34.67
M256	SHS72*5	2	IS2062	3208	32.2	64.4
M257	SHS72*5	1	IS2062	3294	33.06	33.06
M258	SHS72*5	2	IS2062	3481	34.91	69.82
M259	SHS72*5	1	IS2062	3226	32.38	32.38
M260	SHS72*5	1	IS2062	3321	34.16	34.16
M261	SHS72*5	1	IS2062	2031	20.57	20.57
M262	SHS72*5	2	IS2062	2816	28.32	56.64
M263	SHS72*5	1	IS2062	2579	25.97	25.97
M264	SHS72*5	3	IS2062	1997	20.23	60.69
M265	SHS72*5	2	IS2062	2168	21.91	43.82
M266	SHS72*5	1	IS2062	1895	19.24	19.24
M267	SHS72*5	3	IS2062	1863	18.93	56.79
M268	SHS72*5	1	IS2062	1624	16.62	16.62
M270	SHS72*5	3	IS2062	1900	19.28	57.84
M271	SHS72*5	1	IS2062	1947	19.75	19.75
M272	SHS72*5	1	IS2062	1884	19.12	19.12
M273	SHS72*5	1	IS2062	2121	21.46	21.46
M274	SHS72*5	1	IS2062	2228	22.5	22.5
M276	SHS72*5	3	IS2062	1350	14.2	42.6
M282	SHS250*10	2	IS2062	15516	1169.13	2338.26
M282	SHS250*10	2	IS2062	15517	1169.17	2338.34
M283	SHS250*10	8	IS2062	8174	615.99	4927.92
M285	SHS250*10	16	IS2062	1250	94.2	1507.2
M286	SHS250*10	1	IS2062	10707	774.51	774.51
M287	SHS250*10	1	IS2062	10407	753.82	753.82
M288	SHS250*10	1	IS2062	10408	753.83	753.83
M289	SHS250*10	2	IS2062	3779	279.22	558.44
M290	SHS250*10	1	IS2062	2303	150.14	150.14
M291	SHS250*10	2	IS2062	2490	161.44	322.88
M292	SHS250*10	2	IS2062	2250	146.99	293.98
M293	SHS250*10	1	IS2062	2262	147.71	147.71
M294	SHS250*10	6	IS2062	1880	125.17	751.02
M295	SHS250*10	2	IS2062	1683	113.97	227.94
M296	SHS250*10	2	IS2062	8120	558.05	1116.1
M297	SHS250*10	1	IS2062	3996	262.21	262.21
M298	SHS250*10	1	IS2062	8108	556.56	556.56
M302	SHS132.0X132.0X4.8	2	IS2062	1603	28.55	57.1
M303	SHS132.0X132.0X4.8	1	IS2062	2183	37.97	37.97
M304	SHS132.0X132.0X4.8	1	IS2062	2164	37.66	37.66
M305	SHS132.0X132.0X4.8	2	IS2062	1350	25.25	50.5
M307	SHS132.0X132.0X4.8	1	IS2062	4236	77.22	77.22
M308	SHS132.0X132.0X4.8	1	IS2062	3669	66.43	66.43
M309	SHS132.0X132.0X4.8	2	IS2062	3791	70.15	140.3
M310	SHS132.0X132.0X4.8	1	IS2062	3849	71.01	71.01
M324	SHS132.0X132.0X4.8	2	IS2062	4346	74.28	148.56
M325	SHS132.0X132.0X4.8	1	IS2062	4066	69.55	69.55
M326	SHS132.0X132.0X4.8	1	IS2062	3958	67.72	67.72
M327	SHS132.0X132.0X4.8	1	IS2062	2297	39.76	39.76
M328	SHS132.0X132.0X4.8	2	IS2062	2587	44.69	89.38
M329	SHS132.0X132.0X4.8	1	IS2062	2122	36.98	36.98
M330	SHS132.0X132.0X4.8	1	IS2062	2227	38.71	38.71
M331	SHS132.0X132.0X4.8	1	IS2062	2287	39.59	39.59
M332	SHS132.0X132.0X4.8	1	IS2062	2567	44.35	44.35
M333	SHS132.0X132.0X4.8	1	IS2062	2546	44	44
M334	SHS132.0X132.0X4.8	2	IS2062	2775	47.72	95.44
M335	SHS132.0X132.0X4.8	1	IS2062	2534	43.7	43.7
M336	SHS132.0X132.0X4.8	1	IS2062	2577	44.42	44.42
M337	SHS132.0X132.0X4.8	1	IS2062	2003	35.04	35.04
M338	SHS132.0X132.0X4.8	2	IS2062	2200	38.26	76.52
M339	SHS132.0X132.0X4.8	1	IS2062	1898	33.33	33.33
M340	SHS132.0X132.0X4.8	2	IS2062	1932	33.53	67.06
M341	SHS132.0X132.0X4.8	4	IS2062	2120	36.6	146.4
M342	SHS132.0X132.0X4.8	1	IS2062	1847	32.16	32.16
M343	SHS132.0X132.0X4.8	2	IS2062	1831	31.89	63.78
M344	SHS132.0X132.0X4.8	2	IS2062	4029	72.71	145.42
M345	SHS132.0X132.0X4.8	2	IS2062	3789	68.34	136.68
M346	SHS132.0X132.0X4.8	2	IS2062	3808	68.69	137.38
M347	SHS132.0X132.0X4.8	3	IS2062	7295	135.17	405.51
M347	SHS132.0X132.0X4.8	1	IS2062	7296	135.18	135.18
M348	SHS132.0X132.0X4.8	2	IS2062	4043	72.99	145.98
M362	SHS180.0X180.0X8.0	2	IS2062	1330	56.48	112.96
M363	SHS180.0X180.0X8.0	1	IS2062	8744	364.95	364.95
M366	SHS180.0X180.0X8.0	1	IS2062	10749	442.91	442.91
M367	SHS180.0X180.0X8.0	2	IS2062	10739	443.96	887.92
M368	SHS180.0X180.0X8.0	2	IS2062	10476	432.96	865.92
M369	SHS180.0X180.0X8.0	1	IS2062	3781	158.24	158.24
M370	SHS180.0X180.0X8.0	2	IS2062	3759	157.31	314.62
M374	SHS180.0X180.0X8.0	2	IS2062	6802	288.8	577.6
M375	SHS180.0X180.0X8.0	2	IS2062	6915	293.59	587.18
M377	SHS180.0X180.0X8.0	2	IS2062	2953	125.4	250.8
M378	SHS180.0X180.0X8.0	1	IS2062	3053	129.64	129.64
M389	SHS150.0X150.0X5.0	2	IS2062	2991	66.58	133.16
M390	SHS150.0X150.0X5.0	2	IS2062	1490	33.18	66.36
M391	SHS150.0X150.0X5.0	2	IS2062	1990	44.31	88.62
M392	SHS150.0X150.0X5.0	1	IS2062	2214	45.4	45.4
M393	SHS150.0X150.0X5.0	1	IS2062	2137	43.9	43.9
M394	SHS150.0X150.0X5.0	1	IS2062	1924	39.77	39.77
M395	SHS150.0X150.0X5.0	1	IS2062	2118	43.53	43.53
M396	SHS150.0X150.0X5.0	1	IS2062	2195	45.03	45.03
M397	SHS150.0X150.0X5.0	2	IS2062	1320	29.39	58.78
M398	SHS150.0X150.0X5.0	3	IS2062	1250	27.83	83.49
M399	SHS150.0X150.0X5.0	3	IS2062	1350	30.05	90.15
M400	SHS150.0X150.0X5.0	4	IS2062	1330	29.55	118.2
M401	SHS150.0X150.0X5.0	2	IS2062	1350	29.68	59.36
M403	SHS150.0X150.0X5.0	1	IS2062	6676	147.59	147.59
M404	SHS150.0X150.0X5.0	1	IS2062	6685	147.79	147.79
M405	SHS150.0X150.0X5.0	1	IS2062	6901	152.53	152.53
M406	SHS150.0X150.0X5.0	1	IS2062	3772	82.95	82.95
M413	SHS150.0X150.0X5.0	8	IS2062	8174	181.97	1455.76
M414	SHS150.0X150.0X5.0	2	IS2062	1850	41.19	82.38
M418	SHS150.0X150.0X5.0	1	IS2062	2953	65.73	65.73
M419	SHS150.0X150.0X5.0	3	IS2062	6350	141.34	424.02
M419	SHS150.0X150.0X5.0	1	IS2062	6350	141.34	141.34
M420	SHS150.0X150.0X5.0	1	IS2062	6398	142.41	142.41
M420	SHS150.0X150.0X5.0	1	IS2062	6399	142.42	142.42
M447	SHS150.0X150.0X5.0	3	IS2062	2560	52	156
M448	SHS150.0X150.0X5.0	1	IS2062	2678	54.3	54.3
M449	SHS150.0X150.0X5.0	1	IS2062	2379	48.47	48.47
M450	SHS150.0X150.0X5.0	1	IS2062	2720	55.12	55.12
M451	SHS150.0X150.0X5.0	1	IS2062	1832	37.65	37.65
M452	SHS150.0X150.0X5.0	1	IS2062	2068	42.15	42.15
M453	SHS150.0X150.0X5.0	1	IS2062	1799	37.03	37.03
M454	SHS150.0X150.0X5.0	2	IS2062	4137	84.57	169.14
M462	SHS150.0X150.0X5.0	1	IS2062	8820	193.57	193.57
M463	SHS150.0X150.0X5.0	2	IS2062	8780	192.93	385.86
M464	SHS150.0X150.0X5.0	1	IS2062	8720	191.32	191.32
M465	SHS250*16	1	IS2062	3813	437.51	437.51
M466	SHS250*16	1	IS2062	3813	437.5	437.5
M467	SHS150*4	4	IS2062	30907	566.75	2267
M468	SHS150*4	2	IS2062	36075	661.53	1323.06
M469	SHS150*4	2	IS2062	12250	224.64	449.28
M470	SHS150*4	2	IS2062	36044	660.96	1321.92
M471	SHS150*4	2	IS2062	8904	161.08	322.16
M471	SHS150*4	2	IS2062	8905	161.09	322.18
M472	SHS150*4	1	IS2062	9217	166.79	166.79
M472	SHS150*4	1	IS2062	9217	166.8	166.8
M472	SHS150*4	1	IS2062	9217	166.81	166.81
M473	SHS150*4	1	IS2062	8821	159.51	159.51
M475	SHS150*4	2	IS2062	8778	158.94	317.88
M476	SHS150*4	1	IS2062	8796	159.08	159.08
M477	SHS250*10	1	IS2062	3784	279.54	279.54
M478	SHS250*10	1	IS2062	3998	262.42	262.42
M479	SHS250*10	1	IS2062	8099	555.93	555.93
M481	ISMC150	4	IS2062	33486	559.91	2239.64
M482	ISMC150	2	IS2062	12250	204.83	409.66
M483	ISMC150	28	IS2062	1100	18.39	514.92
M487	SHS132.0X132.0X4.8	1	IS2062	2066	35.71	35.71
M488	SHS150.0X150.0X5.0	1	IS2062	6901	152.53	152.53
M489	SHS150.0X150.0X5.0	1	IS2062	2397	48.83	48.83
M497	SHS100.0X100.0X6.0	1	IS2062	1500	25.47	25.47
M498	SHS100.0X100.0X6.0	1	IS2062	1425	24.2	24.2
M500	SHS72*5	2	IS2062	1839	18.69	37.38
M501	SHS72*5	15	IS2062	1882	19.1	286.5
M501	SHS72*5	2	IS2062	1882	19.11	38.22
M502	SHS72*5	2	IS2062	1881	19.09	38.18
M503	SHS72*5	2	IS2062	1955	19.82	39.64
M504	SHS72*5	2	IS2062	1811	18.42	36.84
M505	SHS72*5	2	IS2062	1885	19.13	38.26
M506	SHS72*5	2	IS2062	1782	18.13	36.26
M507	SHS72*5	2	IS2062	1989	20.15	40.3
M508	SHS72*5	2	IS2062	1878	19.07	38.14
M509	SHS72*5	4	IS2062	1786	18.17	72.68
M510	SHS72*5	2	IS2062	1983	20.09	40.18
M510	SHS72*5	2	IS2062	1984	20.1	40.2
M511	SHS72*5	1	IS2062	1950	20.17	20.17
M512	SHS72*5	2	IS2062	1786	18.18	36.36
M512	SHS72*5	2	IS2062	1787	18.19	36.38
M513	SHS72*5	2	IS2062	1983	20.09	40.18
M514	SHS72*5	2	IS2062	2173	21.96	43.92
M515	SHS72*5	2	IS2062	2086	21.1	42.2
M516	SHS72*5	2	IS2062	1761	17.93	35.86
M516	SHS72*5	2	IS2062	1761	17.94	35.88
M517	SHS72*5	24	IS2062	1350	14.2	340.8
M533	SHS150*4	1	IS2062	9218	166.81	166.81
M535	ISA75X75X6	22	IS2062	150	1.02	22.44
M536	SHS50*3.6	2	IS2062	1340	7.03	14.06
PL153	PL10*180	8	IS2062	420	5.93	47.44
PL154	PL10*210	9	IS2062	510	8.41	75.69
PL155	PL10*180	3	IS2062	510	7.21	21.63
PL156	PL10*180	4	IS2062	268	3.79	15.16
PL157	PL10*250	4	IS2062	330	6.48	25.92
PL158	PL10*250	4	IS2062	450	8.83	35.32
PL159	PL10*210	2	IS2062	780	12.86	25.72
PL160	PL10*210	2	IS2062	540	8.9	17.8
PL161	PL10*210	1	IS2062	580	9.56	9.56
PL162	PL10*250	1	IS2062	580	11.38	11.38
PL163	PL10*180	24	IS2062	210	2.97	71.28
PL164	PL10*280	8	IS2062	310	6.81	54.48
PL165	PL10*180	16	IS2062	180	2.54	40.64
PL166	PL10*280	8	IS2062	280	6.15	49.2
PL167	PL10*140	1	IS2062	600	6.59	6.59
PL168	PL10*155	10	IS2062	180	2.19	21.9
PL169	PL10*180	2	IS2062	500	7.07	14.14
PL170	PL10*210	2	IS2062	210	3.46	6.92
PL171	PL10*210	1	IS2062	650	10.72	10.72
PL172	PL10*155	1	IS2062	450	5.48	5.48
PL173	PL10*155	6	IS2062	500	6.08	36.48
PL174	PL10*155	1	IS2062	550	6.69	6.69
PL175	PL10*140	1	IS2062	700	7.69	7.69
PL176	PL10*210	1	IS2062	700	11.54	11.54
PL177	PL5*145	4	IS2062	145	0.83	3.32
PLT2	PLT6*300	2	IS2062	15521	219.32	438.64
PLT2	PLT6*300	2	IS2062	15522	219.32	438.64
PLT3	PLT6*300	2	IS2062	15526	219.39	438.78
PLT3	PLT6*300	2	IS2062	15527	219.4	438.8
PLT4	PLT12*300	4	IS2062	7440	209.27	837.08
PLT5	PLT10*250	2	IS2062	310	6.08	12.16
PLT7	PLT10*300	1	IS2062	781	18.39	18.39
PLT8	PLT10*300	2	IS2062	1000	23.55	47.1
PLT9	PLT10*300	1	IS2062	440	10.36	10.36
PLT10	PLT10*100	12	IS2062	150	0.85	10.2
PLT12	PL16*280	8	IS2062	300	10.55	84.4
PLT25	PL10*180	41	IS2062	180	2.54	104.14
PLT27	PL10*210	4	IS2062	210	3.46	13.84
PLT79	PL10*210	2	IS2062	520	8.57	17.14
PLT80	PL10*180	2	IS2062	520	7.35	14.7
PLT81	PL10*180	4	IS2062	480	6.78	27.12
PLT82	PL10*210	10	IS2062	510	8.41	84.1
PLT83	PL10*330	4	IS2062	560	14.51	58.04
PLT84	PL10*210	1	IS2062	540	8.9	8.9
PLT85	PL10*250	1	IS2062	580	11.38	11.38
PLT86	PL10*180	8	IS2062	420	5.93	47.44
PLT95	PL10*330	4	IS2062	1037	26.88	107.52
PLT96	PL10*280	1	IS2062	1024	22.51	22.51
PLT96	PL10*280	1	IS2062	1025	22.53	22.53
PLT97	PL10*280	1	IS2062	1014	22.29	22.29
PLT97	PL10*280	1	IS2062	1015	22.31	22.31
PLT98	PL10*280	2	IS2062	1009	22.17	44.34
PLT109	PL10*230	1	IS2062	280	5.06	5.06
PLT110	PL10*180	1	IS2062	234	3.31	3.31
PLT110	PL10*180	2	IS2062	235	3.32	6.64
PLT111	PL10*210	2	IS2062	269	4.44	8.88
PLT111	PL10*210	2	IS2062	270	4.45	8.9
PLT112	PL10*280	2	IS2062	351	7.71	15.42
PLT113	PL10*330	1	IS2062	351	9.1	9.1
PLT114	PL10*300	1	IS2062	1044	24.59	24.59
PLT115	PL10*250	6	IS2062	838	16.45	98.7
PLT116	PL10*280	1	IS2062	1054	23.17	23.17
PLT126	PLT16*300	2	IS2062	8599	324.01	648.02
PLT127	PL5*245	4	IS2062	245	2.36	9.44
PLT128	PL5*145	8	IS2062	145	0.83	6.64
	TOTAL					**68134.18**

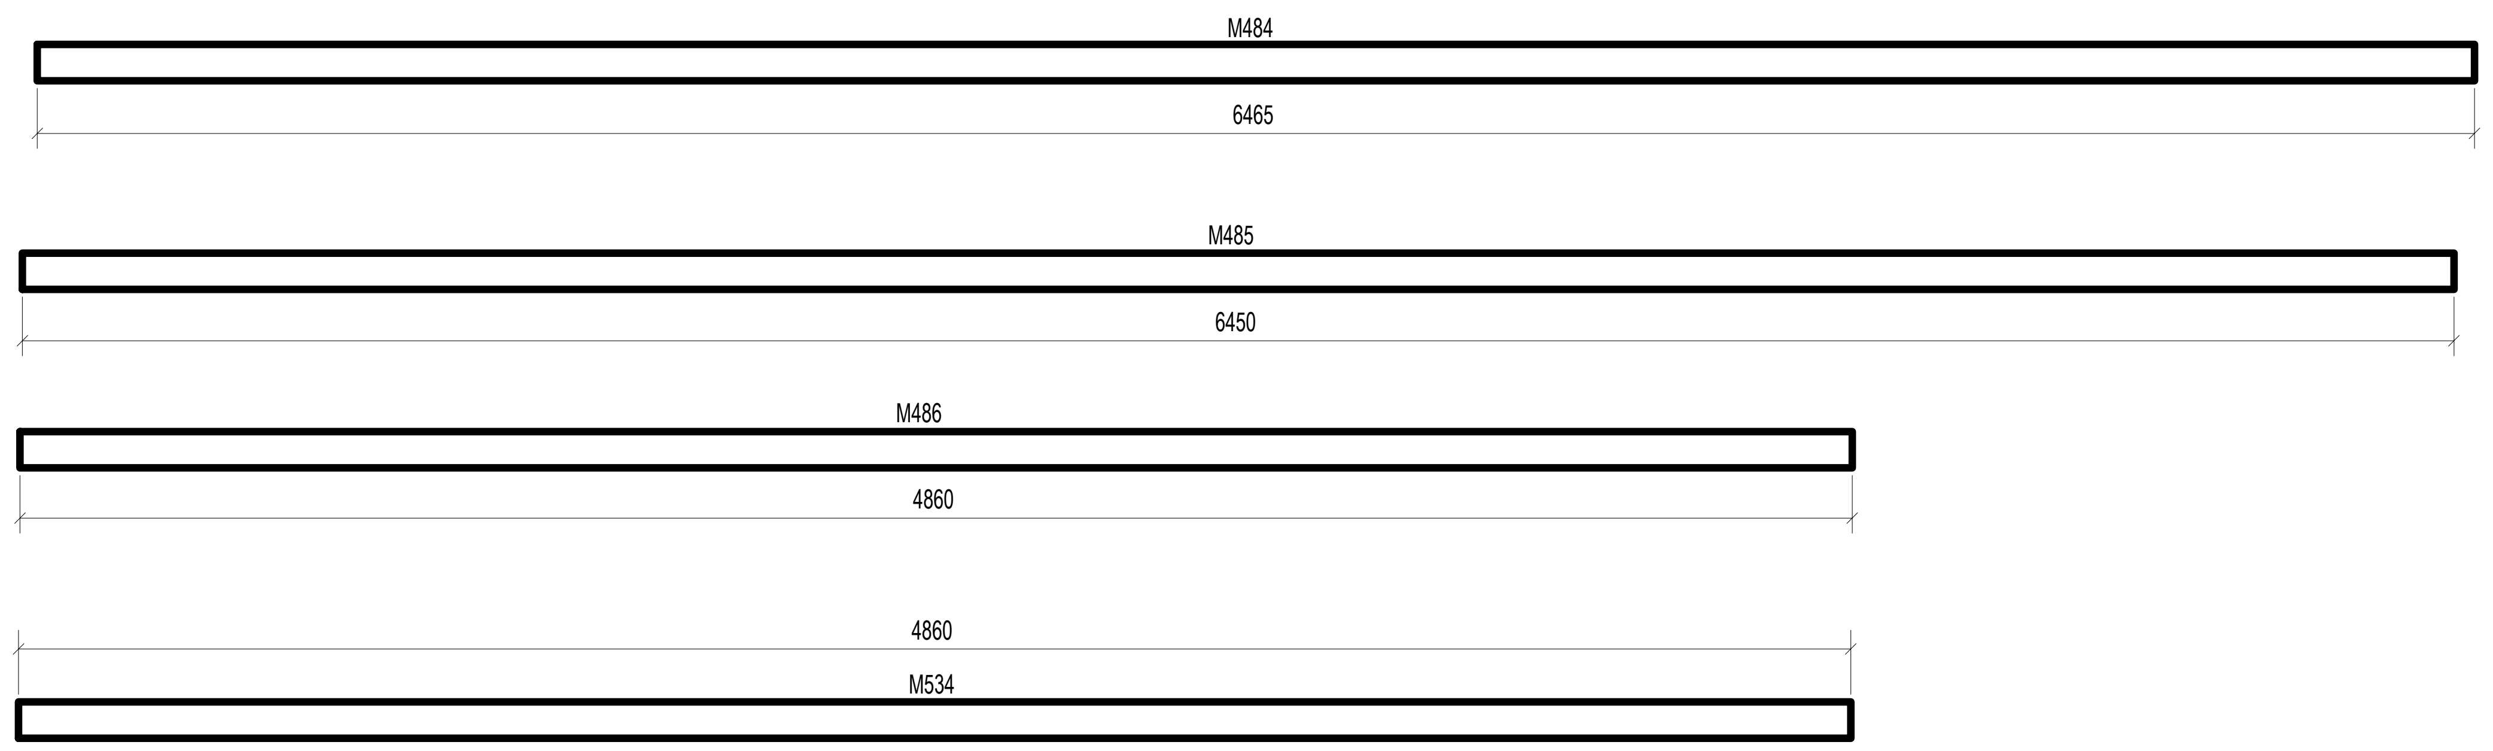

0	DRAWING FOR APPROVAL	29.12.22	AAK	HAB	HAB
REV.NO.	DESCRIPTION.	REV.DATE	DRAWN.	CHKD.	APPD.

DWG.TITLE :- CUTTING DETAILS OF PURLINS & MTO FOR 84.00M TRUSS

PROJECT	MEGADOOR INSTALLATION AT HYDRABAD AIRPORT
CLIENT	GMR

SALT DESIGN SERVICES

NIHVA TECHNOLOGIES
PVT. LTD. PUNE
Tel : 020 66304033
Email:- info@nihva.com
Website:- www.nihva.com

DRAWN :AAK	CHECKED : HAB	SCALE: 1:100
APPROVED : HAB	JOB CODE. : 1729	DATE: 29.12.2022

DWG.NO: SALT_1729_STR_13_R0 (SH-1OF1) REV. - R0 SIZE. - A0

A1 [841 x 594]