



TOP FRAME DETAILS

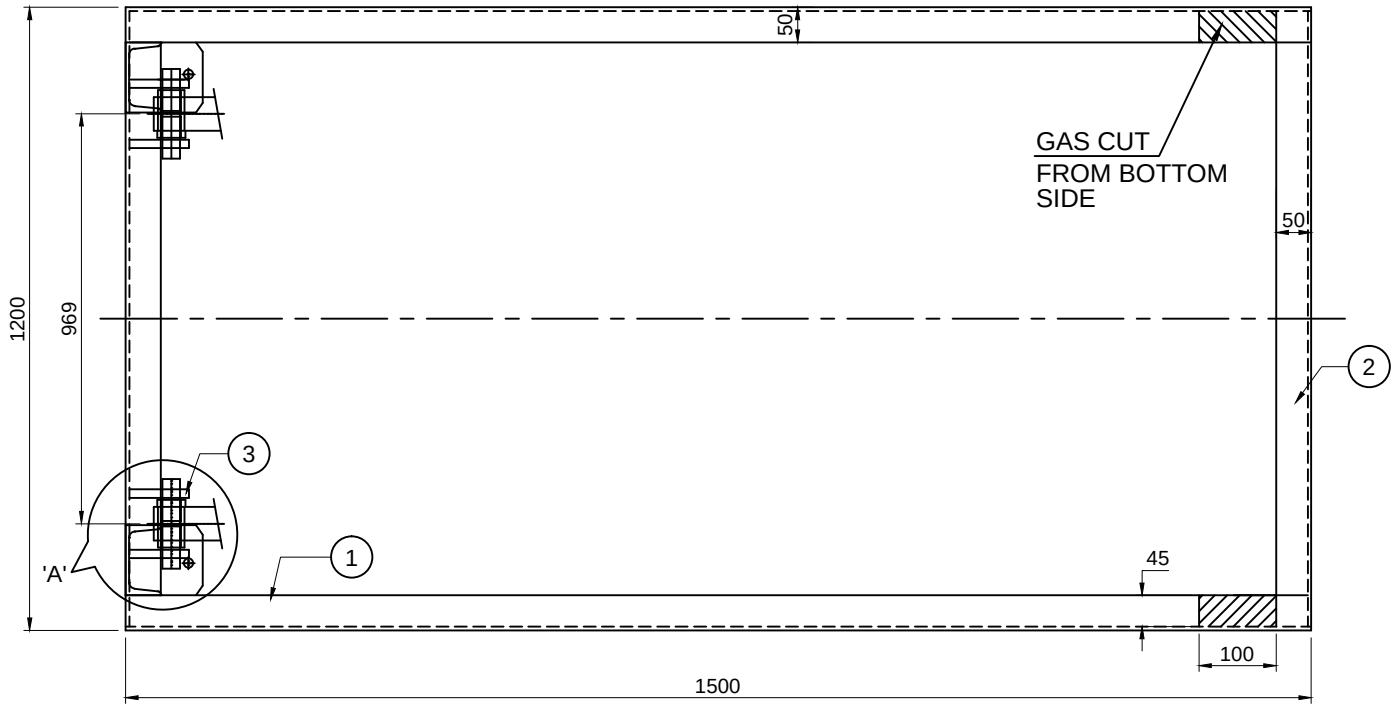

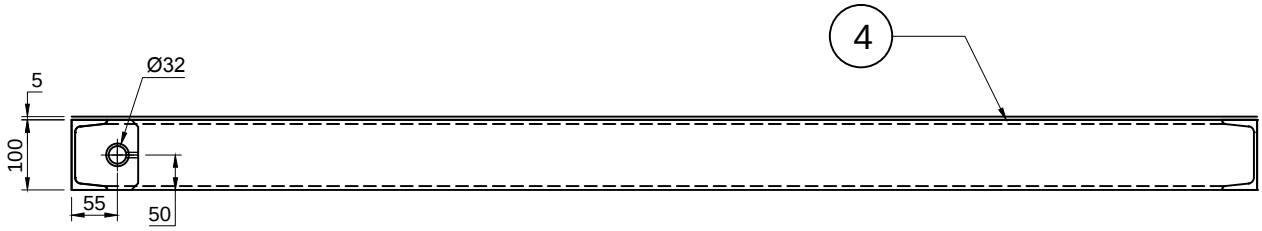

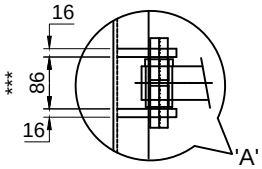

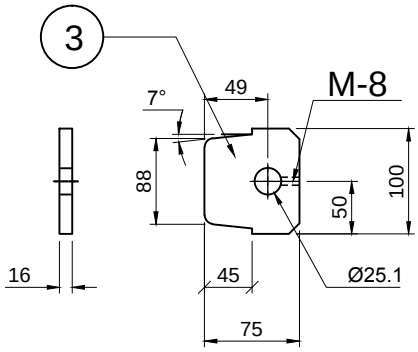

SR.NO	DESCRIPTION	QTY.
4.	CHEQ.SHEET 1200 X 3 THK X 1500L	1 NO
3.	PROFILE 100 X 16 X 75L	4NOS
2.	ISMC 100 x 50 x 1188L	2NOS
1.	ISMC 100 x 50 x 1500L	2NOS

This drawing & design is the property of NIHVA TECHNOLOGIES. Not to be sold or copied to any other concern.

TITLE : - TOP FRAME ASSLY

NIHVA TECHNOLOGIES PVT. LTD.

NIHVA TECHNOLOGIES PVT. LTD. PUNE
Tel : 020 66304033
Email:- info@nihva.com
Website:- www.nihva.com

	SIGN	DATE
DRAWN	P.A	04.10.18
CHECK	R.D	04.10.18
REV.		
APPROVAL		

CLIENT -
PROJECT -
SITE -
DWG. NO. : NIHVA/18-19/MFG/NSL/1018/002
If any queries contact : projects@nihva.com
SCALE: NTS | WT: | SHEET: 01 OF 01
ALL DIMENSION ARE IN mm