




SIDE VIEW

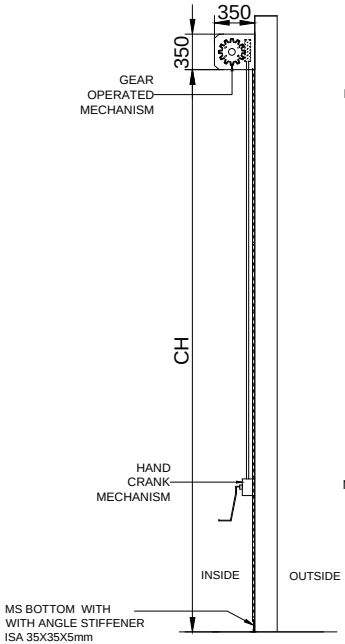


INSIDE ELEVATION

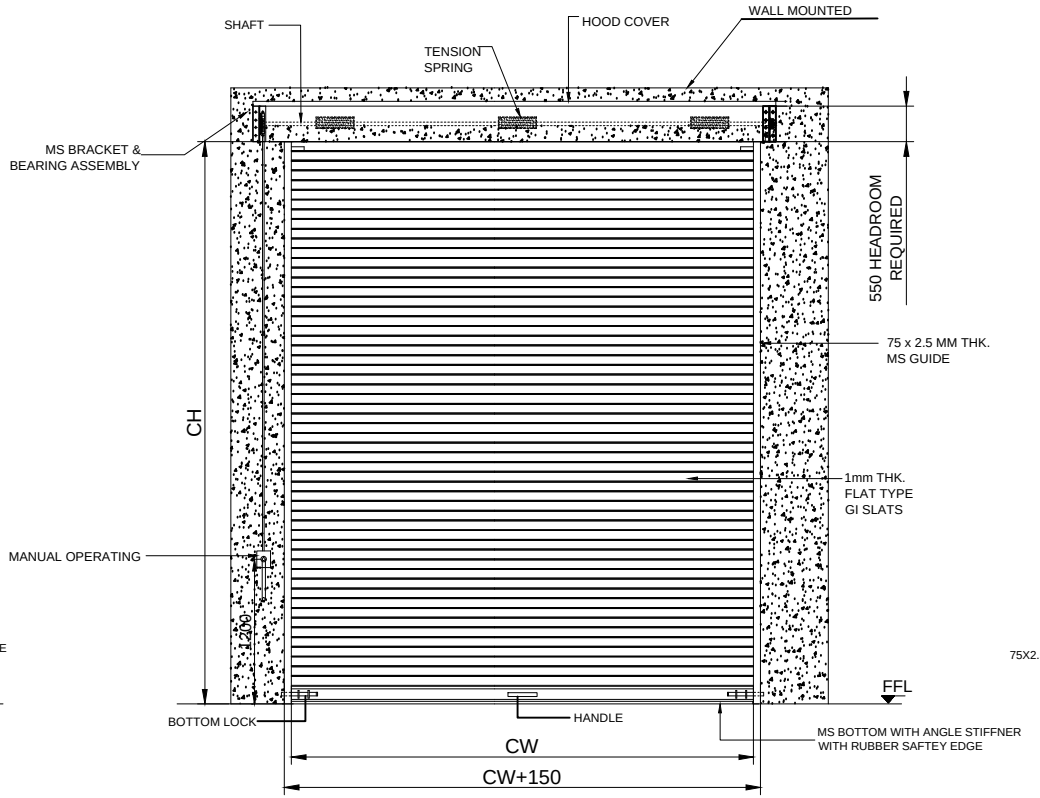

PLAN

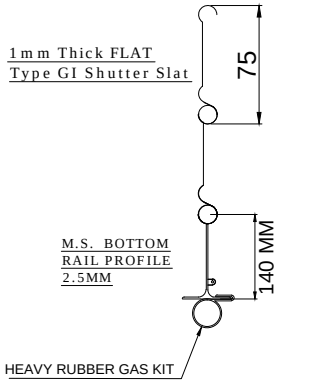

M.S. BOTTOM RAIL PROFILE 2.5MM

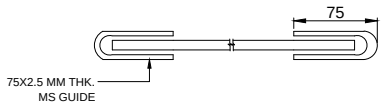

NOTE-
1. ALL CIVIL WORK WILL BE CLIENT'S SCOPE.

TOLERANCE - ±10mm

SR.NO.	RAL COLOR
01	RAL 9002 (WHITE GREY)

SR.NO.	SIZE	QUANTITY
01	2000(W) X 3000(H)	05 NOS
02	3000(W) X 2.460(H)	01 NO

This drawing & design is the property of NIHVA TECHNOLOGIES. Not to be sold or copied to any other concern.

TITLE
GEAR OPERATED ROLLING SHUTTER

	NAME	SIGN	DATE
DRAWN	P.A		14.12.2019
CHECK	G.J		14.12.2019
APPRD.			

If any queries contact : design@nihva.com

ALL DIMENSION ARE IN mm

NIHVA TECHNOLOGIES PVT. LTD.
NIHVA TECHNOLOGIES PVT. LTD. PUNE
Tel : 020 66304033
Email:- info@nihva.com
Website:- www.nihva.com

CLIENT - SYNERGY PROPERTY DEVELOPMENT SERVICES PVT LTD

PROJECT-

SITE LOCATION - CHAKAN

DWG. NO. : NIHVA/19-20/0172 | REV- 0

SCALE: NTS | WT: | SHEET: 01 OF 01