


PRODUCED BY AN AUTODESK EDUCATIONAL PRODUCT

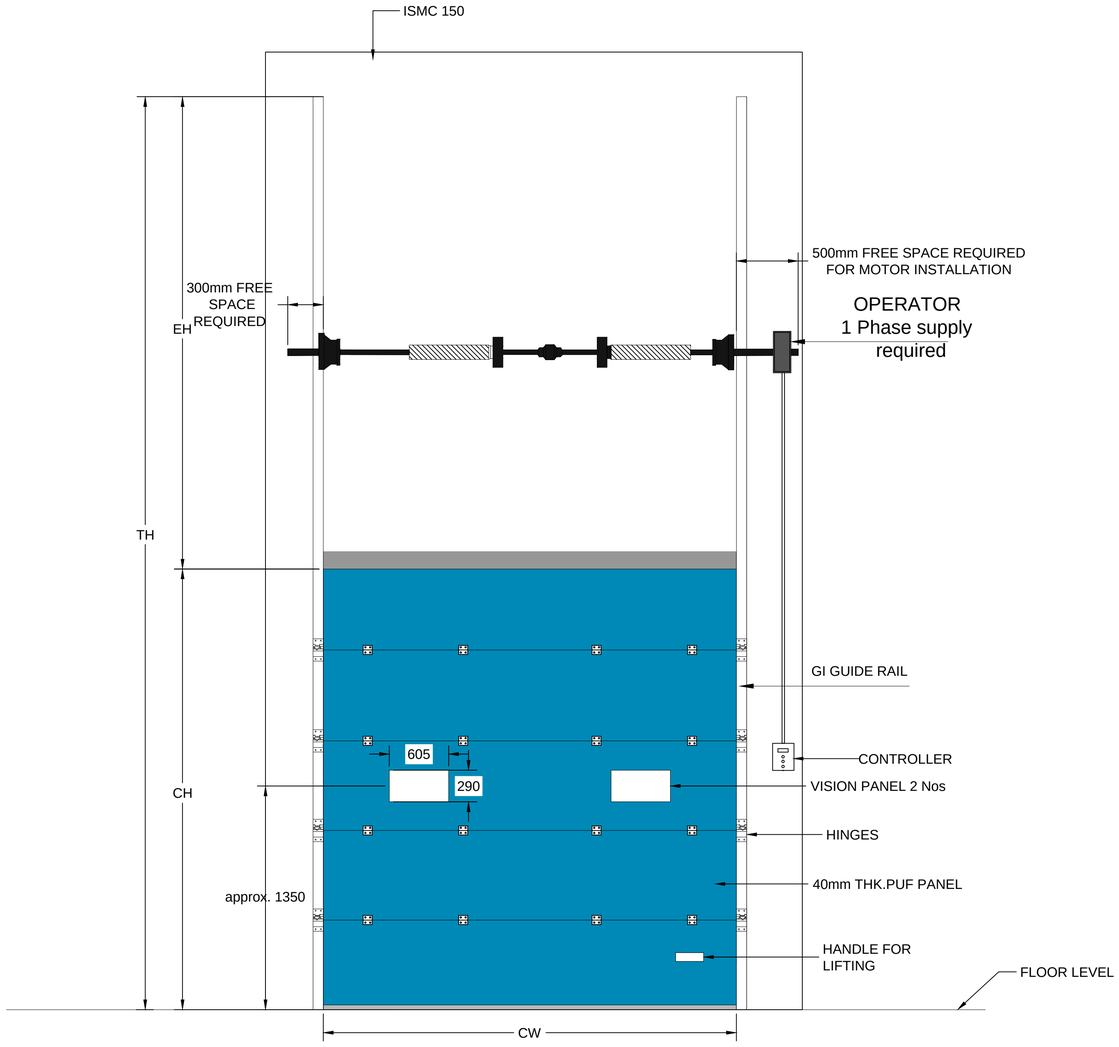


INSIDE ELEVATION

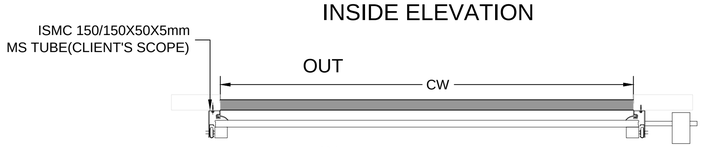

PLAN

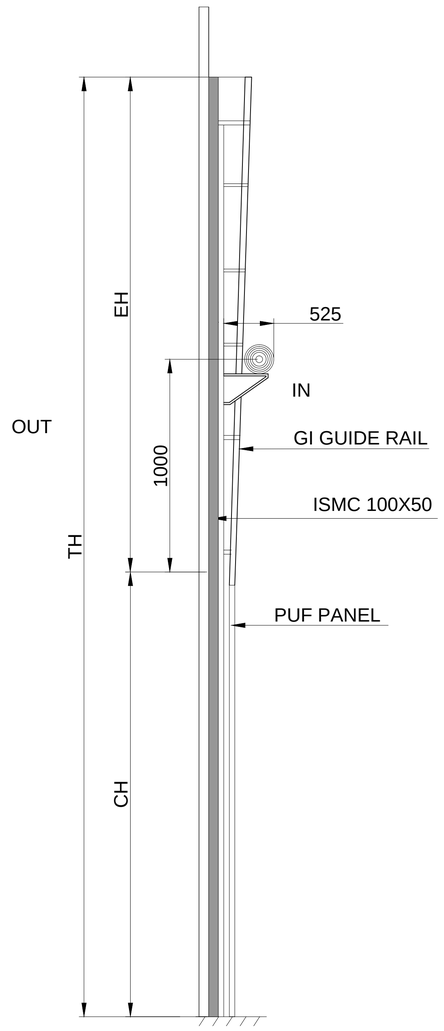

SIDE VIEW

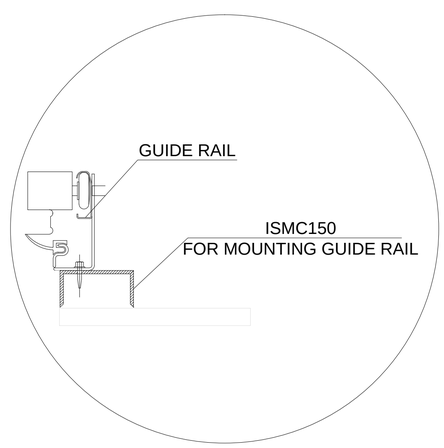

TRACK DETAILS

SR NO	CLEAR WIDTH (CW)	CLEAR HEIGHT (CH)	QUANTITY	EH	TH	LOCATION
1	3000	3000	1	600	6600	

NOTE- 1. STRUCTURE REQUIRED FOR SECTIONAL DOOR SHALL BE IN CLIENT'S SCOPE.
2.COLOR FOR SECTIONAL DOOR PANEL WOULD BE RAL 5012(LIGHT BLUE)

This drawing & design is the property of NIHVA TECHNOLOGIES. Not be sold or copy to any other concern.

TITLE: SECTIONAL DOOR VL (MOTORIZED)

NIHVA TECHNOLOGIES PVT. LTD.
NIHVA TECHNOLOGIES PVT. LTD. PUNE
Tel : 020 66304033
Email:- info@nihva.com
Website:- www.nihva.com

	SIGN	DATE
DRAWN	OMKAR	31/07/17
CHECK	SHEKHAR	31/07/17
REV.		
APPROVAL		

CLIENT - SCON PROJECTS
PROJECT - BEKAERT INDUSTRIES PVT. LTD.
SITE - RAJANGAON, MIDC
DWG. NO. : NIHVA/17-18/0141
If any queries contact : projects@nihva.com
SCALE: NTS | WT: | SHEET: 01 OF 01
ALL DIMENSION ARE IN mm

PRODUCED BY AN AUTODESK EDUCATIONAL PRODUCT