


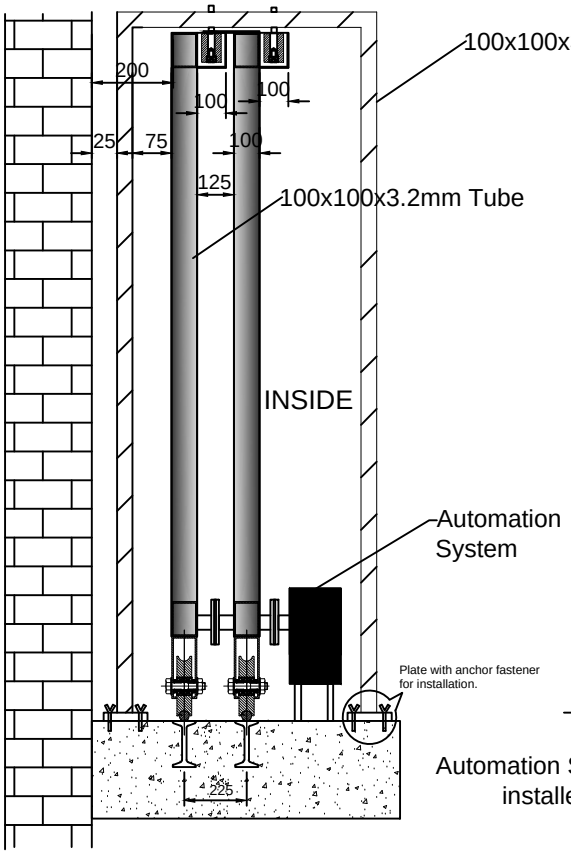



OPENING DIRECTION

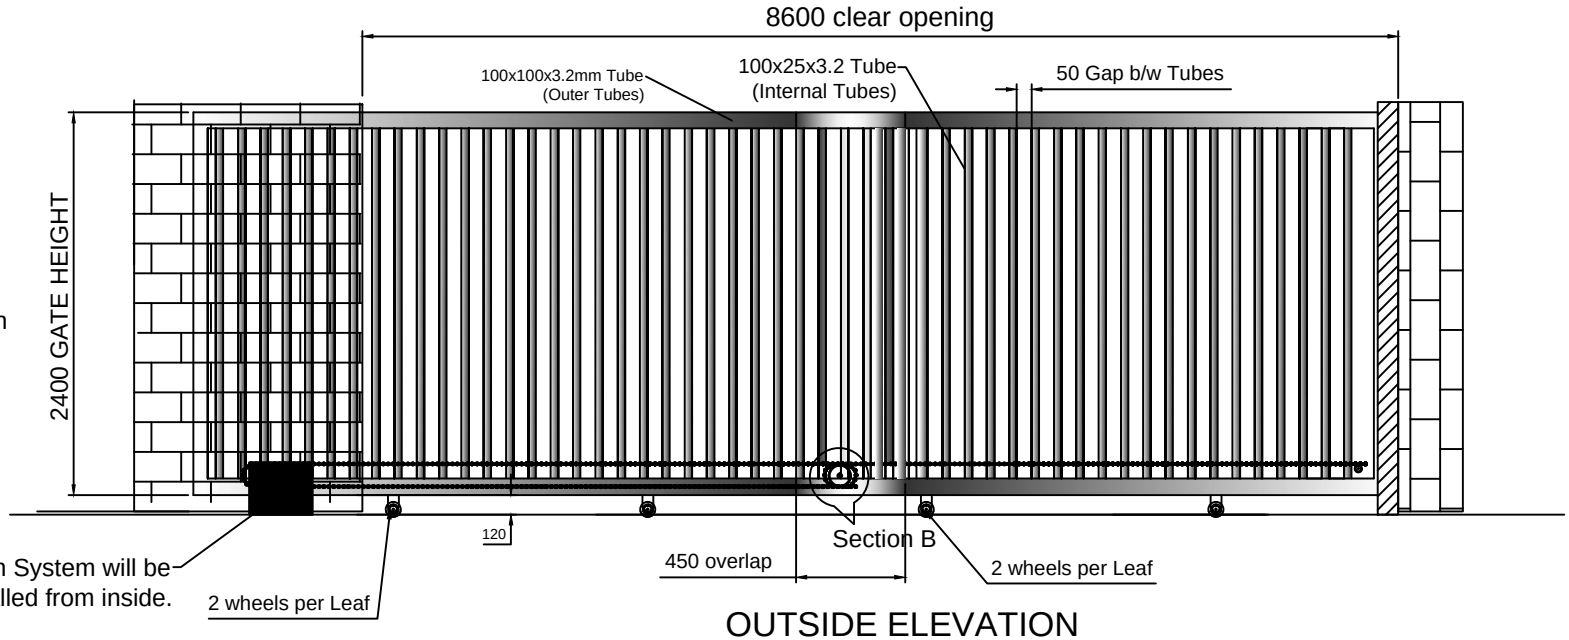


OUTSIDE ELEVATION

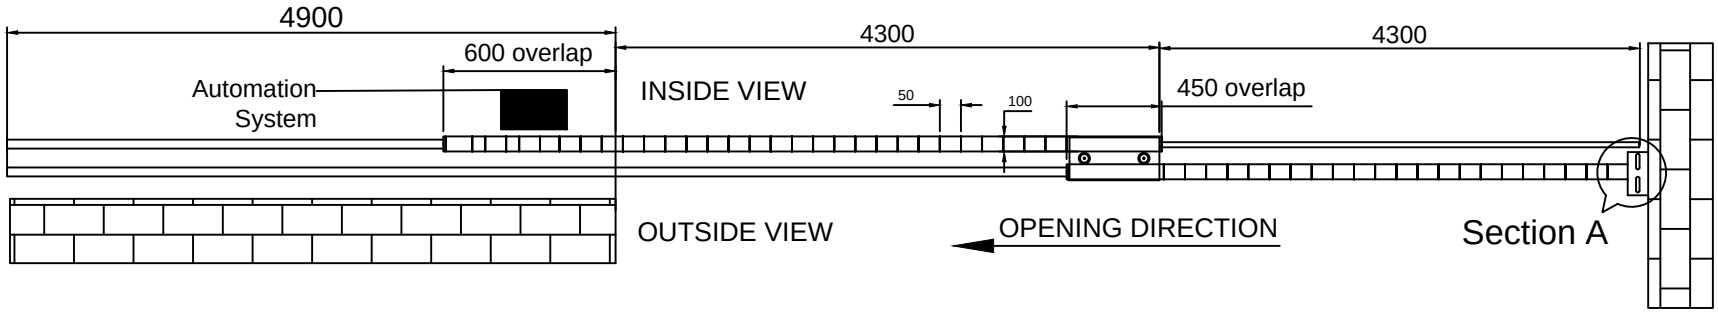

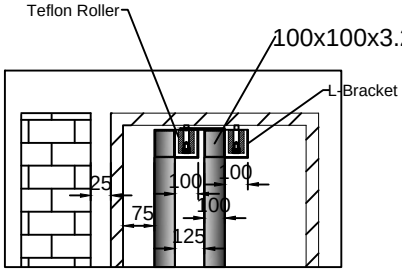


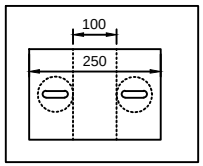

Top Section A

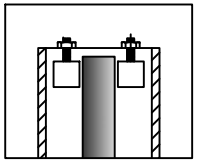

Side section A

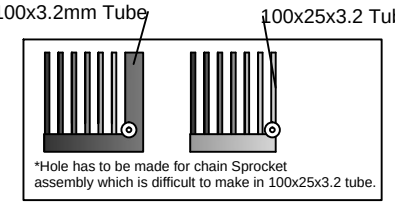

Section B

This drawing & designing is the property of NIHVA TECHNOLOGIES. Not be sold or copy to any other concern.

TITLE: TELESCOPIC SLIDING GATE LOCATION- GUARD HOUSE			NIHVA TECHNOLOGIES PVT. LTD.
	SIGN	DATE	
DRAWN	OMKAR	16/02/16	CLIENT - LUPIN
CHECK	ANIL	16/02/16	PROJECT -LUPIN
REV.	01		SITE -
APPROVAL			DWG. NO. : NIHVA/15-16/177
If any queries contact : projects@nihva.com			SCALE: 01 / WT: / SHEET: 01 OF 01
ALL DIMENSION ARE IN mm			

NIHVA TECHNOLOGY PVT. LTD. PUNE
Tel : 020 66304033
Email:- info@nihva.com
Website:- www.nihva.com