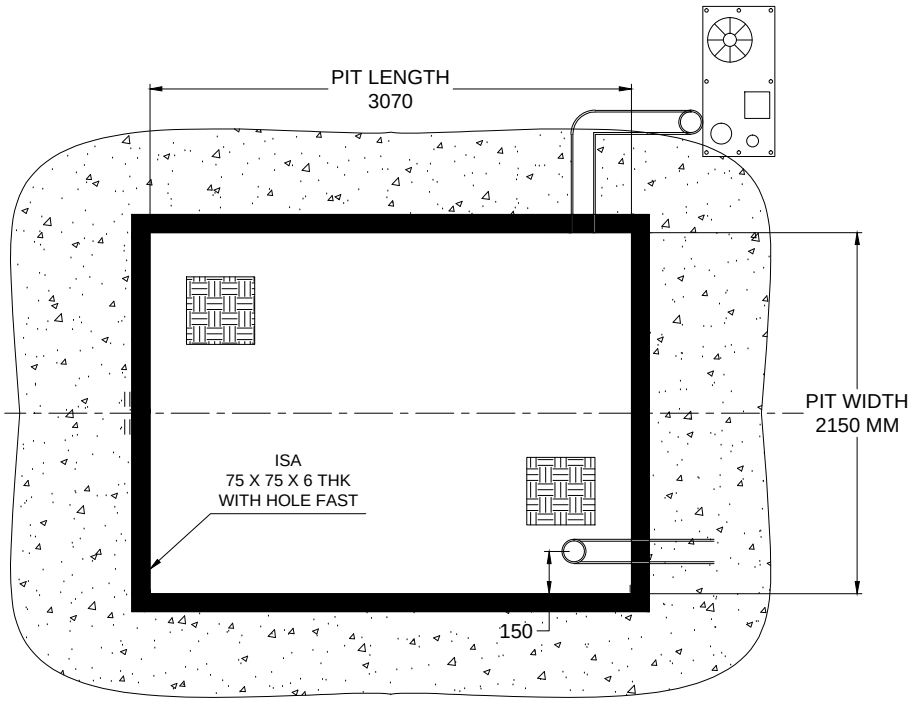

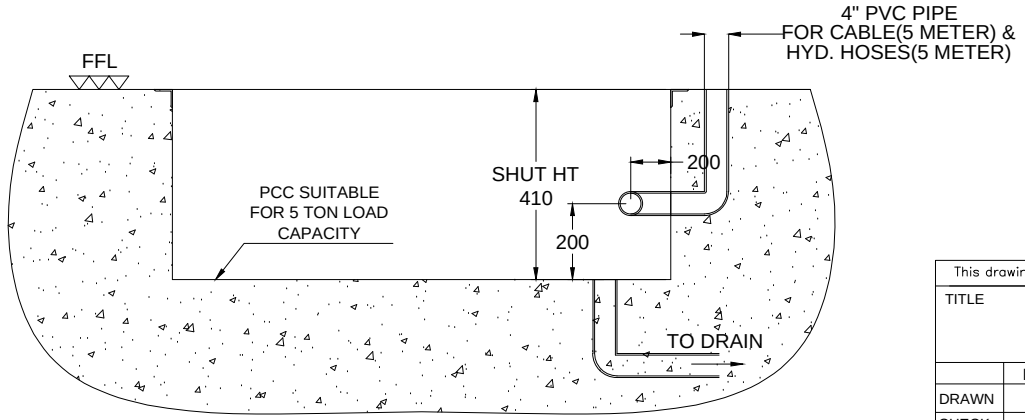

NOTE :-

1. PIT LEVEL SHOULD PARALLEL.
2. ALL CIVIL WORK IN CLIENT SCOPE.

This drawing & design is the property of NIHVA TECHNOLOGIES. Not to be sold or copied to any other concern.

TITLE	PIT DRAWING			NIHVA TECHNOLOGIES PVT. LTD. PUNE Tel : 020 66304033 Email:- info@nihva.com Website:- www.nihva.com
	NAME	SIGN	DATE	
DRAWN	S.M.S.		14.10.2020	CLIENT - STANLEY BLACK & DECKER
CHECK	P.V.A.		14.10.2020	PROJECT -
APPRD.				SITE LOCATION - PUNE
If any queries contact : projectsupport@nihva.com				DWG. NO. : NIHVA/20-21/0066 REV- 0
ALL DIMENSION ARE IN mm				SCALE: NTS WT: SHEET: 01 OF 01