
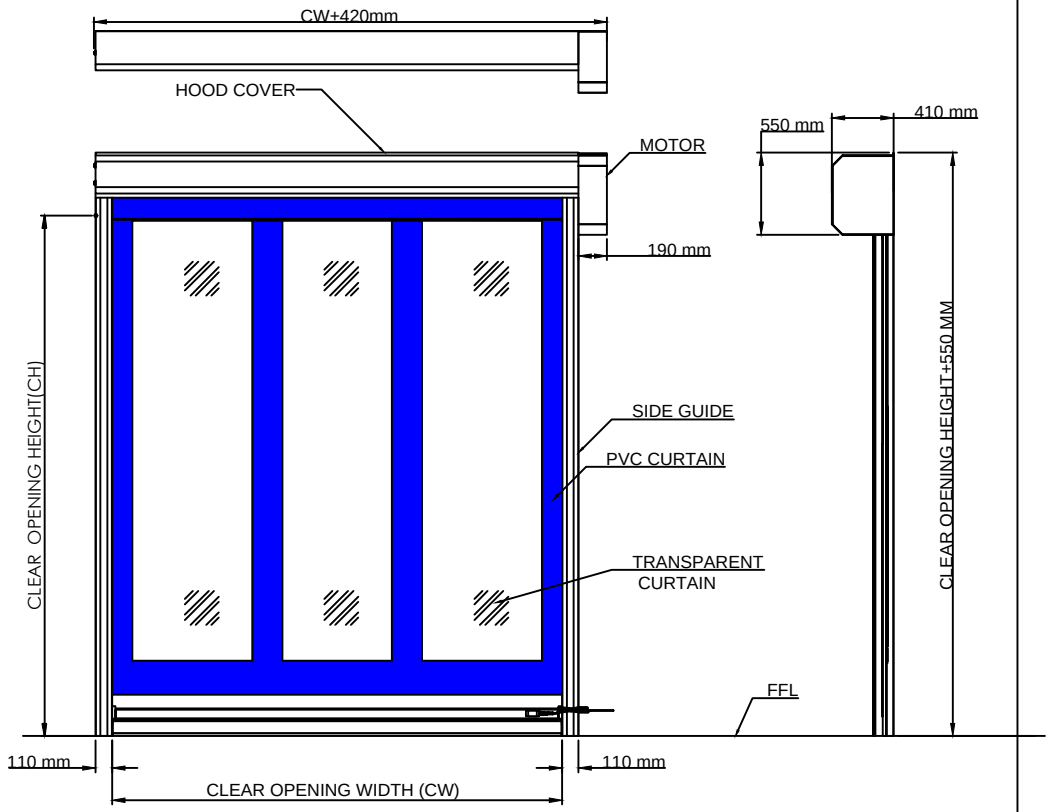


HIGH SPEED DOOR

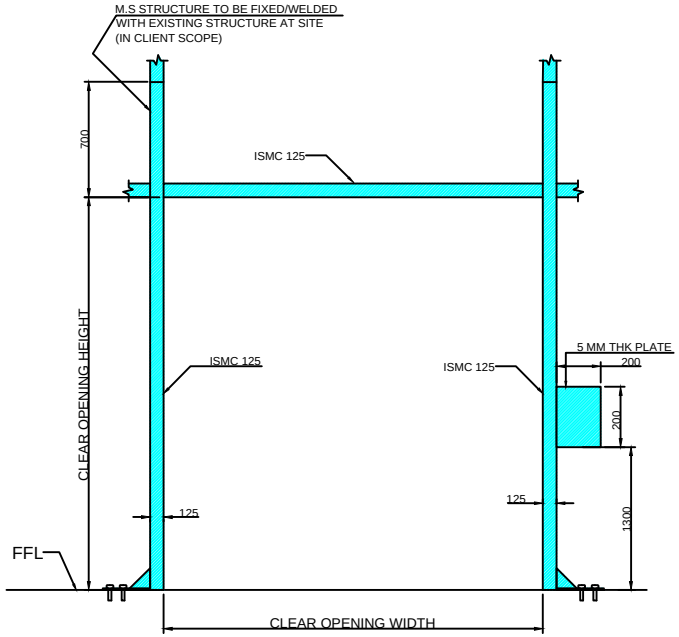

M.S. STRUCTURE(CLIENT SCOPE)

NOTE:
1. REQUIRED M.S. STRUCTURE , FITTING & ALL CIVIL WORK IS IN CLIENT SCOPE.
2. M.S. STRUCTURE SHOULD BE RIGID & NEED TO BE FIXED/WELDED WITH EXISTING STRUCTURE AT SITE(IN CLIENT SCOPE).
3. HIGH SPEED DOOR WILL BE ONLY INSTALLED AFTER READINESS OF STRUCTURE AS PER DRAWING PROVIDED.
4. MOTOR POSITION RIGHT SIDE AS STANDARD.

R01	S.M.S.	24.12.2020	M.S. STRUCTURE MOUNTING QUANTITY ADDED
REV NO	DRAWN	DATE	REMARK

3000	3000	3 NOS	
2500	2500	1 NO	
CLEAR OPENING WIDTH (CW)	CLEAR OPENING HEIGHT (CH)	QUANTITY	MOTOR POSITION (RH/LH)

RAL CODE FOR PVC CURTAIN-BLUE

This drawing & design is the property of NIHVA TECHNOLOGIES. Not to be sold or copied to any other concern.

TITLE: NIHVA MAKE HIGH SPEED DOOR

NIHVA TECHNOLOGIES PVT. LTD.
NIHVA TECHNOLOGIES PVT. PUNE
Tel : 020 66304033
Email:- info@nihva.com
Website:- www.nihva.com

	NAME	SIGN	DATE
DRAWN	S.M.S.		22.12.2020
CHECK			
APPRD.			

CLIENT - TRANS ENGINEERS INDIA PVT LTD
PROJECT - MARS INTERNATIONAL INDIA PVT LTD
SITE LOCATION - PUNE
If any queries contact : design@nihva.com
DWG. NO. : NIHVA/20-21/0115/R01 REV- R01
ALL DIMENSION ARE IN mm
SCALE: NTS WT: SHEET: A4