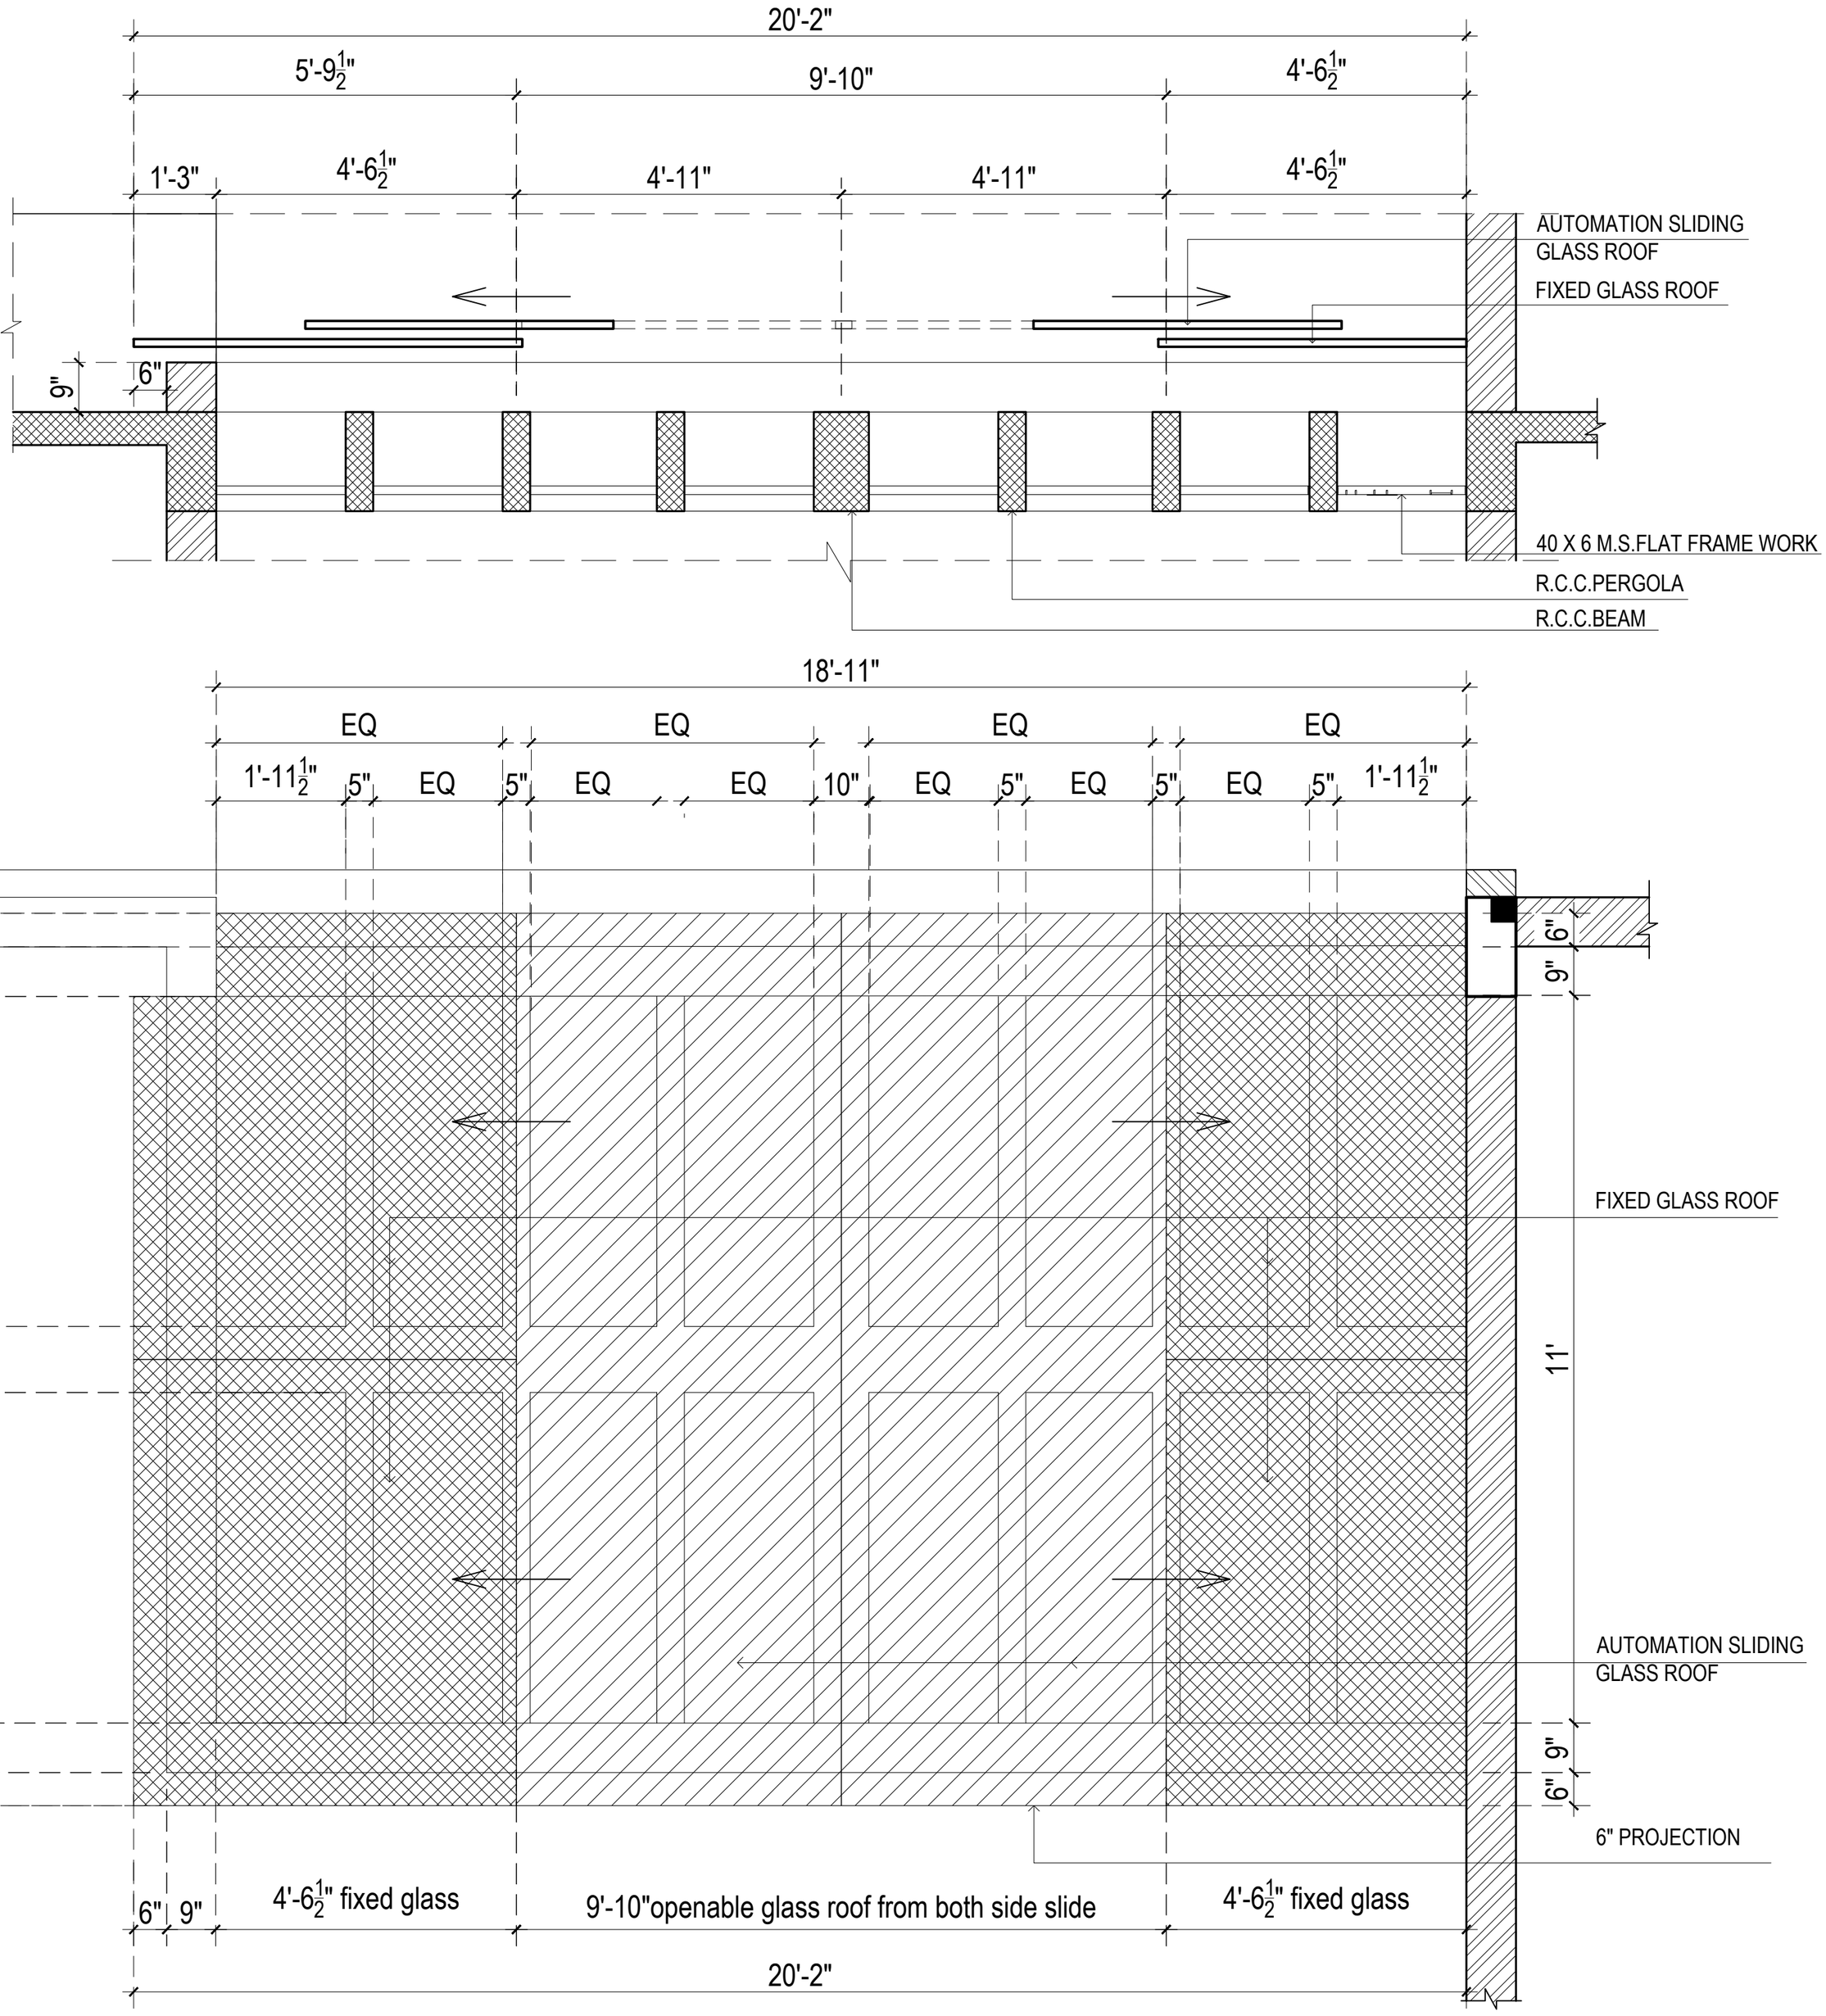



# AUTOMATION GLASS ROOF DETAILS

Date
13 08 21

Revision
00

• Project :-

Proposed Residence for,
Pragneshbhai Patel.
At., Plot no 143, Shaligram,
Bakrol.

• Notes

1. Client shall approved this drawing before sending to the site for execution.
2. All dimensions are in Feet - Inches.
3. Do not scale the drawing.
4. Refer structural drawings approved by structural engineer alongside.
5. Contact Architect or Client in case of any discrepancy.
6. All work shall be executed as per Relevant '**Indian Standards**'.
7. This drawing is property of '**Shreeji Designing**'. Usage of this drawing other then mentioned in project is strictly prohibited.


shreeji designing

**Ar. Snehal Mistri**

B.Architecture (CA/2017/87784) (S.P.U.) D.Civil Engg. (T.E.B.)
Vyas Wado, Nr. Holi Chakla, Ode 388 210
Mo : **91-97231 47466**, E-mail : arch.snehalmistri@gmail.com



F:\VVN OFFICE WORK\PROJECTS 2020\Pragneshbhai, Shaligram, Bakrol_25-06-20\WORKING\DETAILS\COURTYARD DETAILS_24-03-21_FINAL.dwg,
14-08-2021 14:43:04, AutoCAD PDF (High Quality Print).pc3