
NORTH SIDE

WEST SIDE

EAST SIDE

SOUTH SIDE

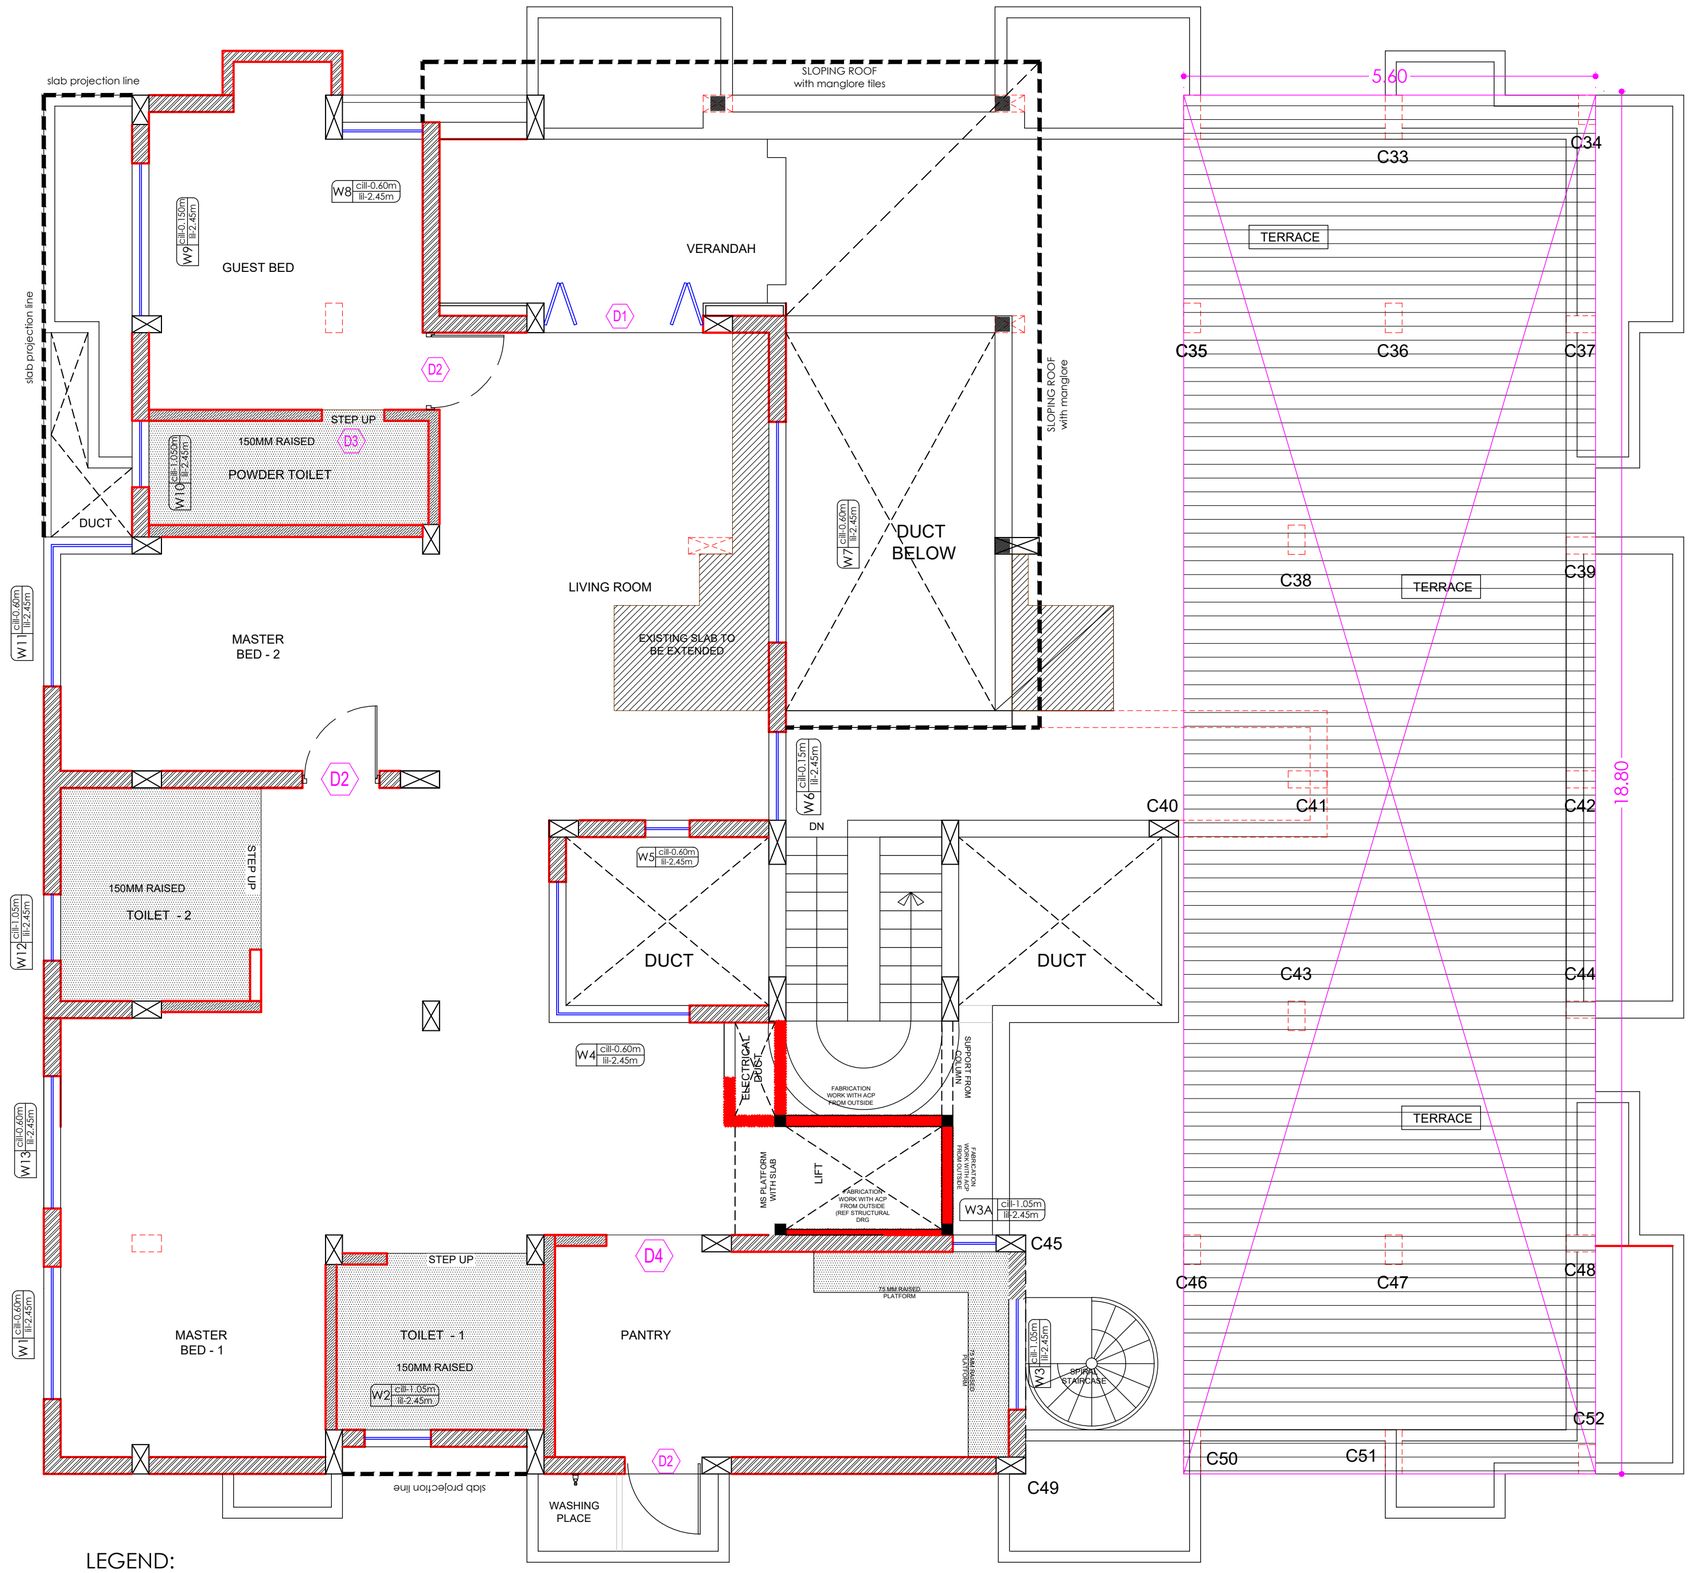

DOOR SCHEDULE	
NOS	SIZE
D1	2.17X2.475M
D2	1.05X2.475M
D3	0.85X2.475M
D4	1.30X2.475M

LEGEND:

230 thk brick wall

150 thk brick wall

DINNING AND PANTRY
GFC (20_09_2022)