Weitergabe sowie Vervielfältigung dieses Dokuments, Verwertung und Mitteilung seines Inhalts sind nur nach vorheriger ausdrücklicher schriftlicher Zustimmung von SMS Meer GmbH gestattet. Das Dokument ist vor unberechtigtem Zugriff Dritter zu schützen. Zuwiderhandlungen verpflichten zu Schadensersatz. Alle Rechte aus Patent-/Gebrauchsmuster-/Markenschutz vorbehalten.

The reproduction, distribution and utilization of this document as well as the disclosure of its content to others without prior explicit written consent of SMS Meer GmbH is prohibited. Holder has to protect this document against unauthorized withdrawal of third parties. Offenders will be held liable for the payment of damages. All rights reserved in case of patent/utility model/trademark protection.

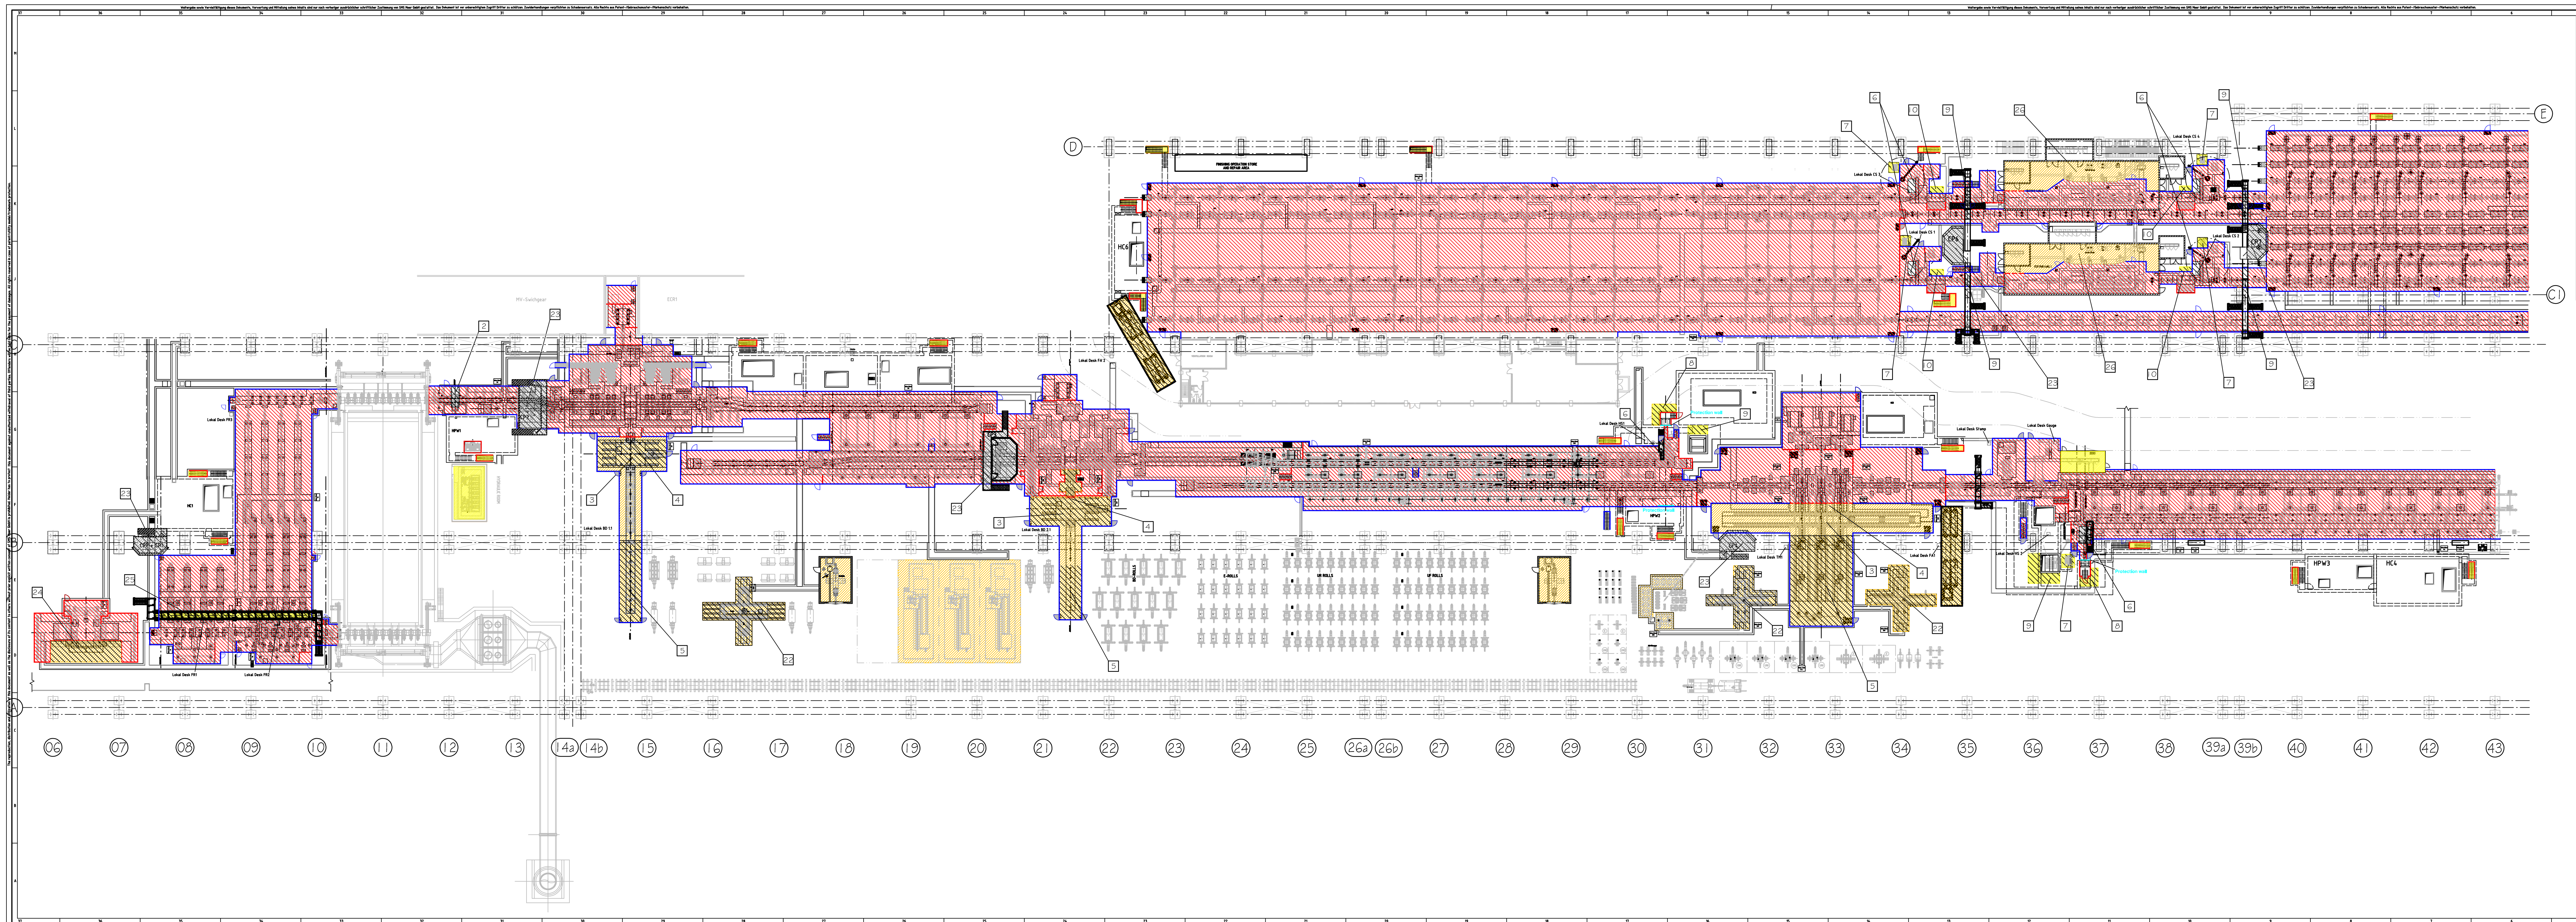

◸	GATE	▧	DANGER ZONE 1 No access while unit is in operation.
◸	GATE WITH MECH. LOCKING DEVICE	▨	DANGER ZONE 2 Access only to qualified and authorized persons possible in defined operating states. High Residual Risks Note safety instructions in operating and maintenance manual.
◸	GATE WITH ELECT. LOCKING DEVICE	▨	DANGER ZONE 3 Access only to qualified and authorized persons possible in defined operating states. Low Residual Risks Note safety instructions in operating and maintenance manual.
◸	DOOR WITH MECH. LOCKING DEVICE	▨	DANGER ZONE 4 Permanente working place: Unrestricted access possible while unit is in operation. Note general safety instructions.
◸	DOOR WITH ELECT. LOCKING DEVICE	▧	WORKING PLACE Part of no access zone, that can be entered by trained operators under particular conditions only Note safety instructions in operating and maintenance manual.
◸	DOOR	▩	SAFETY CONSIDERATION BY CUSTOMER
◸	DOOR WITH MECH. LOCKING DEVICE		
◸	DOOR WITH ELECT. LOCKING DEVICE		

➡	ESCAPE ROUTES
━	RAILING
━ · ━	REMOVABLE RAILING
━	FENCE
━ · ━	REMOVABLE FENCE
●-·-●	REMOVABLE CHAIN
╍╍	LIGHT BARRIER
✕✕✕	EXPANDING BARRIER
◎	REQUEST-/ ACKNOWLEDGEMENT BUTTON
●	EMERGENCY STOP

Working Areas

1	loading of beams and blanks	16	
2	change of spraying rings	17	
3	Activities during mill stand changing	18	
4	Inspection under load	19	finished products
5	preparation works for mill stand changing	20	removal of short length
6	change of saw blade	21	repairing of beams
7	preparation saw blade	22	preparation of rolls, chocks and guides
8	change of chip bucket	23	operating and control
9	change of scrap bucket	24	surface defect removal
10	handling of sample	25	inspection of bloom
11	testing of sample (laboratory)	26	testcenter
12	preparation straightening rolls	27	removal of rejected rails
13	activities during straight.roll changing	28	change of drill
14	inspection products	29	manuell handling of products
15			

Positions of crossovers must be in correspondence with the General Routing Plan (by Customer)

This safety layout must be considered in coherence with safety Instructions in Operation and Maintenance Manual. (Especially Chapter A2)

9463 0000 / RAILBHIL

CATEGORY OF DRWG.	APPROVAL	INFORMATION	REFERENCE	RECORD	CONSTRUCTION

SAIL

BHILAI STEEL PLANT, BHILAI, CHATTISGARH
7,0 MTPA EXPANSION

मेकॉन लिमिटेड
MECON LIMITED

VENSDOR'S NAME: SMS Meer/SMS Meer India/ABB
PACKAGE DESCRIPTION: UNIVERSAL RAIL MILL (Pkg No-047)
TITLE OF DRAWING. SAFETY LAYOUT, ±0,00
SCALE-
VENDOR'S DRG NO.-
PROJECT DRG. NO. BSP-SMS Meer-08-047-21-120-50-BE-06603

Fertigungsvorschriften
Manufacturing Instructions
SN 200

Ursprung / Origin
Fertiggewicht
Finished weight
kg
Modell-Nr.
Pattern-No.
Werkstoff / Material
Projektionsmethode 1
First angle projection method
ISO 128

	Datum Date	Name
Bearb. Drawn	30.03.12	Fryen
Geprüft Checked	30.03.12	Prätzel
Norm Stand		

Aus- gabe Issue	Änderung Revision	Datum Date	Name

Typ
Type
SAFETY LAYOUT
Benennung
Sicherheitslayout, ±0.00
Title
SAFETY LAYOUT ±0.00
Maßstab
Scale
1:200
Sach-Nr.
Drawing-No.
0100133-00.603
Blatt
Sheet
1
4
Blätter
Sheets
Ersatz für:/Supersedes:
Ersetzt durch:/Superseded by:

SMS MEER
SMS group

Diese Zeichnung und alle darauf enthaltenen Informationen sind vertraulich. This drawing and all information on it is confidential.

A0