


DRAWING


REV DESCRIPTION	DATE	REV NO
03. AIR TIGHTENING & DUST PROOF RUBBER IS ADDED	00-00-2025	REV 03
04. SECTION 2 PANEL MODIFICATION	10-07-2025	REV 04
05. SECTION 2 SAME UNIT ANTHOER THREE PANEL MODIFICATION	15-07-2025	REV 05
06. MIDDLE PANEL MOTOR POSITION CHANGE	24-07-2025	REV 06
06. SECTION 1 PANEL MODIFICATION	30-07-2025	REV 07

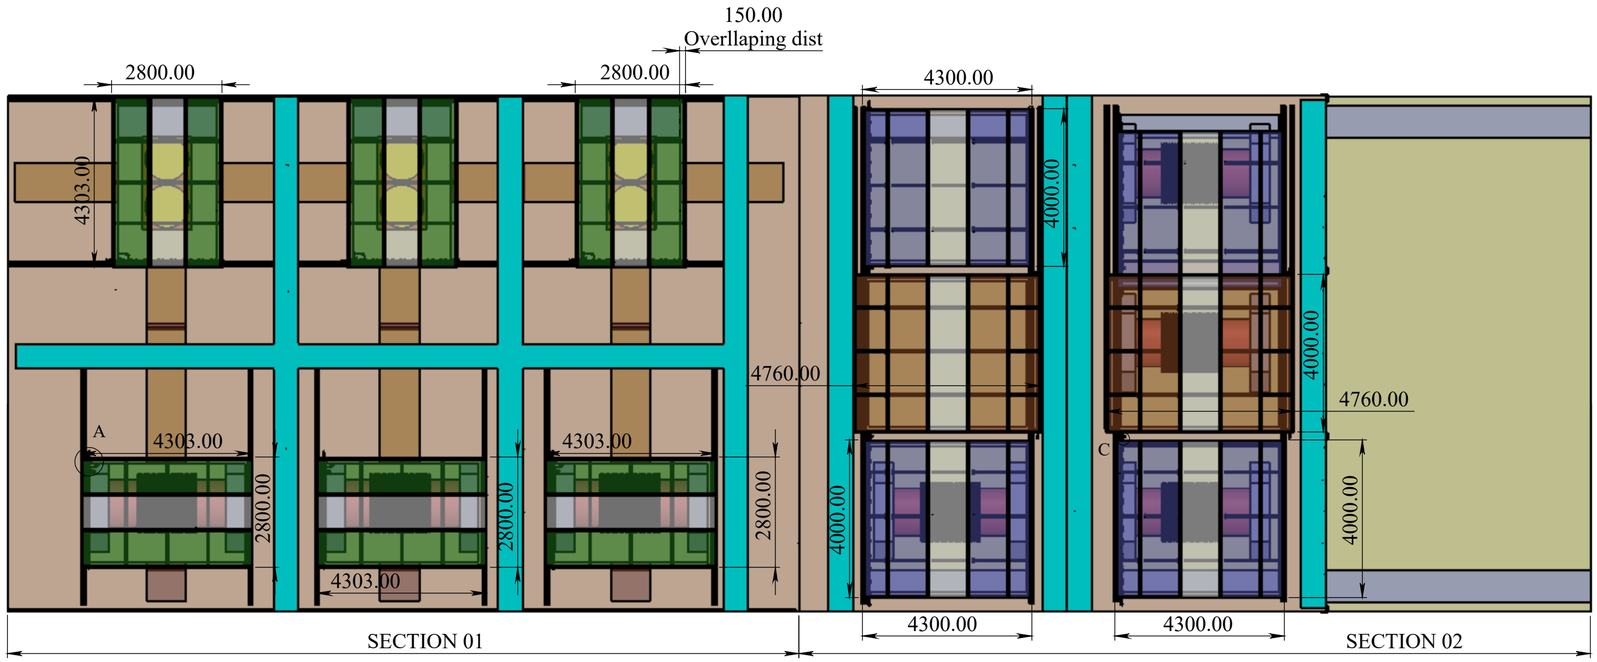

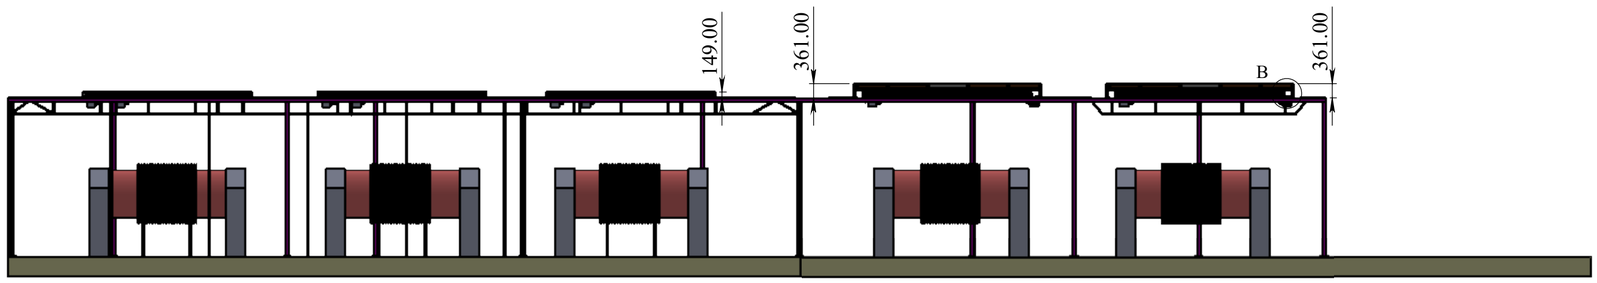


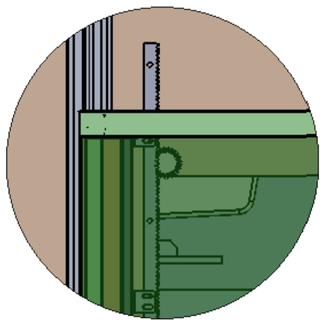

DETAIL A
SCALE 1 : 10

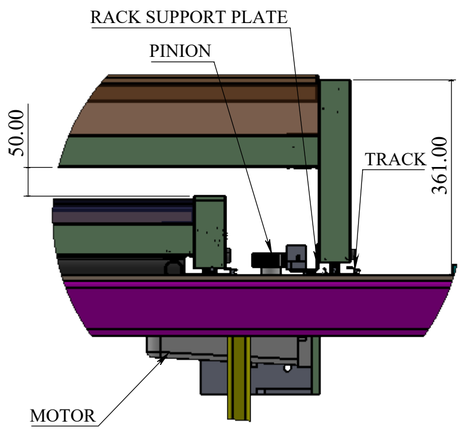

DETAIL B
SCALE 1 : 8

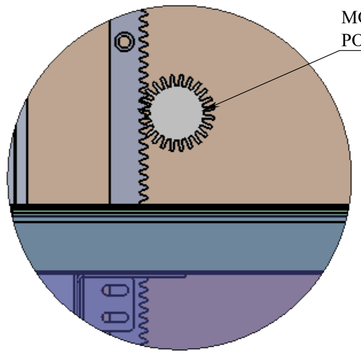

DETAIL C
SCALE 1 : 4

NOTE :

SPECIAL INSTRUCTION'S :

TITLE - ROOF AUTOMATION

DWG NO - NTPL-244-PM-001-00-00-00

NIHVA Technologies Pvt. Ltd.

NIHVA TECHNOLOGIES PVT.LTD.PUNE
Website - www.nihva.com

	NAME	SIGNATURE	DATE		
DRAWN	V.W.		30-07-2025	PROJECT NO - NTPL-244-PM	REVISION - 07
CHK'D	S.P.		31-07-2025	SITE LOCATION - AHMEDABAD	WEIGHT -
APPV'D	V.T.		31-07-2025	MATRIAL -	QTY - 1

If any queries contact - design.nihva@gmail.com


ALL DIMENSION ARE IN mm | A2

PROJECTION METHOD:

SCALE :


SHEET 1 OF 9


DRAWING

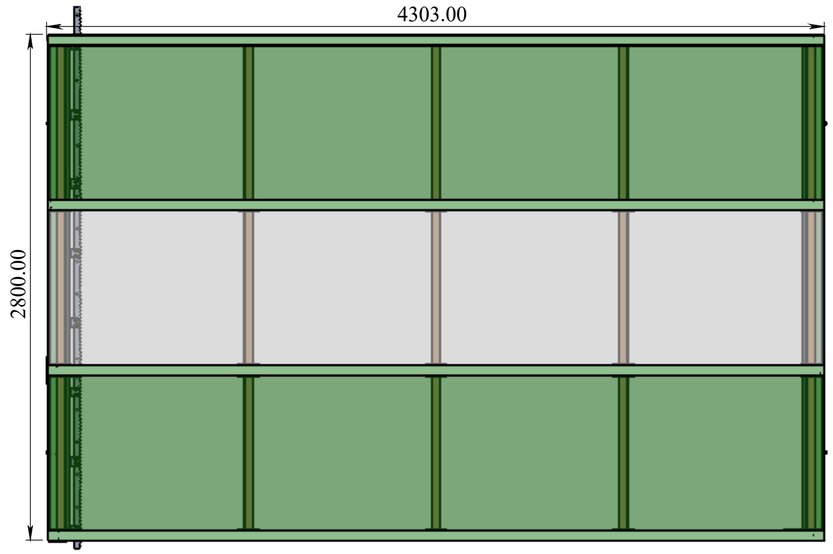


ITEM NO.	PART NUMBER	DESCRIPTION	QTY.
1	.rev0202paneel modify-03.		1
2	.Rev_02_panel modifiy-03 intermediate support assembly.		15
3	.Rev_02_SS WHEEL.	SS WHEEL ∅65X18	4
4	NP-PROF01	MS50X50X4T	1
5	T PLATE	156X91X3 MM THK	1
6	L PLATE	91X106X3 MM THK	1
7	.Rev_02_AL INSIDE CORNER WELD PLATE.	196X40X3 MM THK	1
8	C-MSBL12-35.SLDASM	SHOULDER BOLT	4
9	RACK SUPPORT PLATE.		8
10	.Rev_02_RACK..		3

REV DESCRIPTION	DATE	REV NO
	30-07-2025	REV 07
1.		

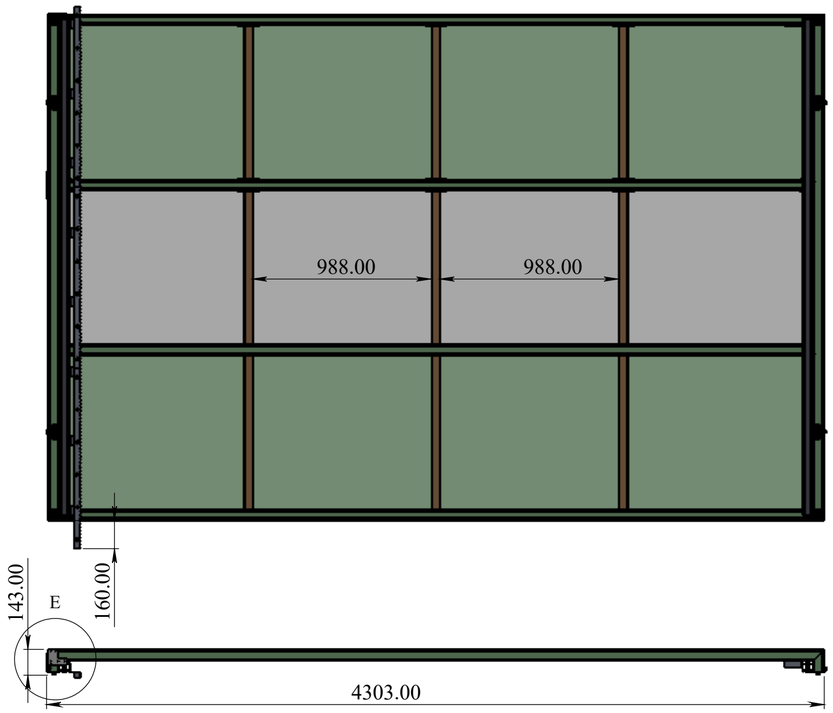


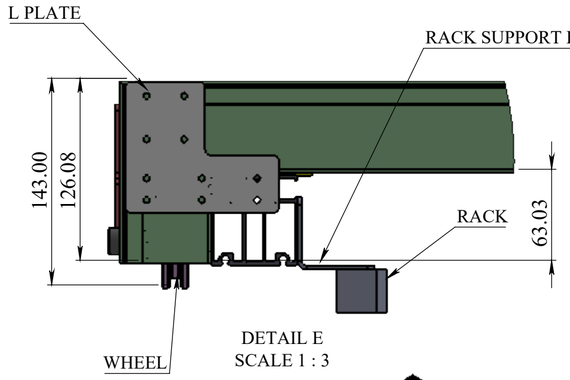

DETAIL E
SCALE 1 : 3

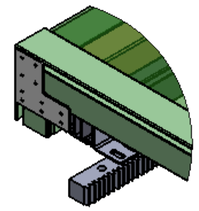

DETAIL F
SCALE 1 : 6

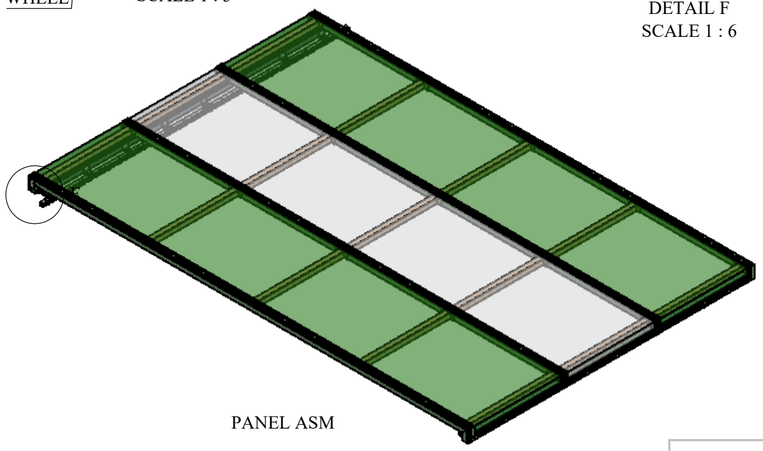

PANEL ASM

NOTE :

SECTION NO 1 PANEL ASM
QTY - 06 No'S.

SPECIAL INSTRUCTION'S :

TITLE - ROOF AUTOMATION

DWG NO - NTPL-244-PM-001-00-00-00

NIHVA Technologies Pvt. Ltd.

NIHVA TECHNOLOGIES PVT.LTD.PUNE
Website - www.nihva.com


	NAME	SIGNATURE	DATE
DRAWN	V.W.		30-07-2025
CHK'D	S.P.		31-07-2025
APPV'D	V.T.		31-07-2025


PRODUCT - RETRACTABLE ROOF
PROJECT NO - NTPL-244-PM | REVISION - 07
SITE LOCATION - AHMEDABAD | WEIGHT -
MATRIAL - | QTY - 01
If any queries contact - design.nihva@gmail.com
PROJECTION METHOD:
SCALE :
ALL DIMENSION ARE IN mm | A2
SHEET 2 OF 9

DRAWING


ITEM NO.	PART NUMBER	DESCRIPTION	QTY.
1	.rev0202paneel modify-03.		1


REV DESCRIPTION	DATE	REV NO
	30-07-2025	REV 07
1.		

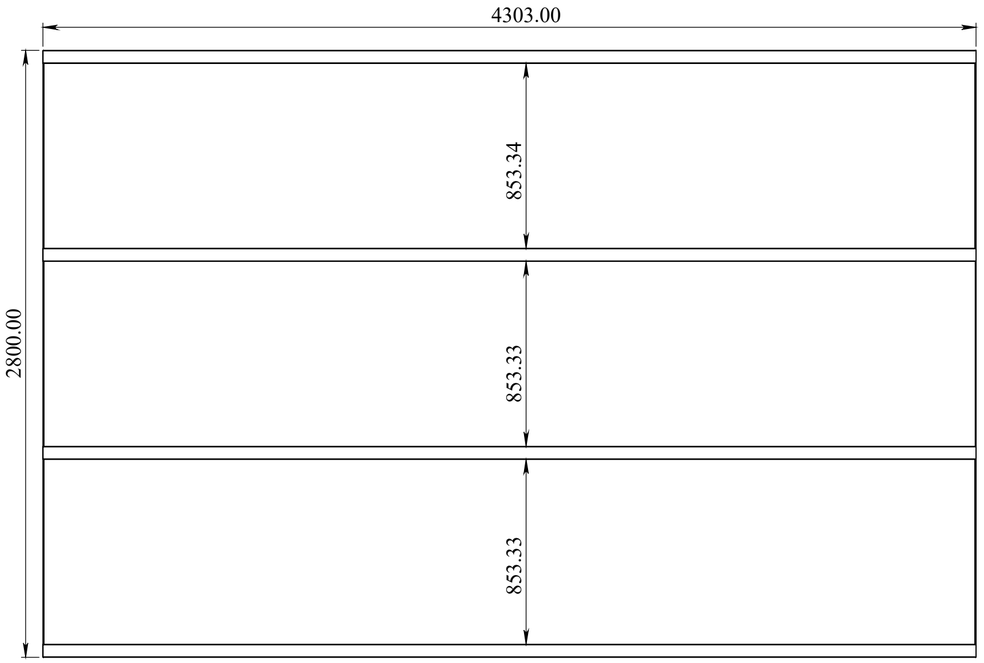

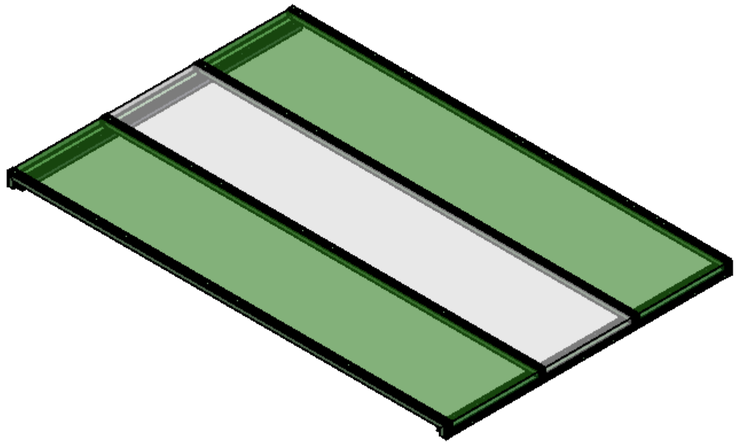

DETAIL G
SCALE 1 : 4

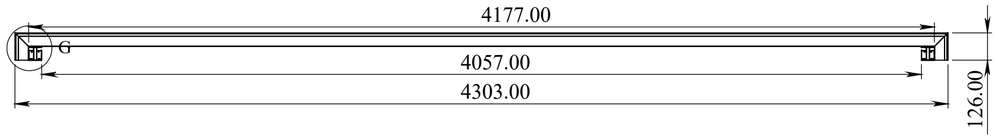

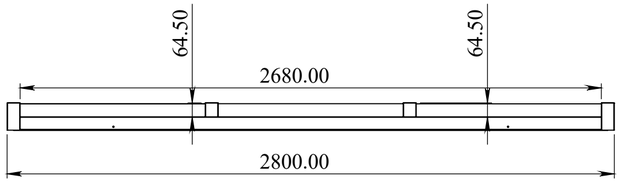

NOTE :

SECTION NO 01 PANEL
ALL PROFILE IN AL GNT-006
QTY - 6 No'S.

SPECIAL INSTRUCTION'S :

ALL PROFILE IN GNT-006

TITLE - ROOF AUTOMATION

DWG NO - NTPL-244-PM-001-00-00-00

NIHVA TECHNOLOGIES PVT.LTD.PUNE
Website - www.nihva.com

	NAME	SIGNATURE	DATE
DRAWN	V.W.		30-07-2025
CHK'D	S.P.		31-07-2025
APPV'D	V.T.		31-07-2025


PRODUCT - RETRACTABLE ROOF
PROJECT NO - NTPL-244-PM
REVISION - 07
SITE LOCATION - AHMEDABAD
WEIGHT -
MATRIAL -
QTY - 01


If any queries contact - design.nihva@gmail.com
ALL DIMENSION ARE IN mm
A2
PROJECTION METHOD:
SCALE :
SHEET 3 OF 9


DRAWING

REV DESCRIPTION	DATE	REV NO
	30-07-2025	REV 07
1.		

ITEM NO.	PART NUMBER	DESCRIPTION	QTY.
1	INTERMEDIATE SUPPORT TUBE - 960 MM L	SQ - 50X50X2 THK	14

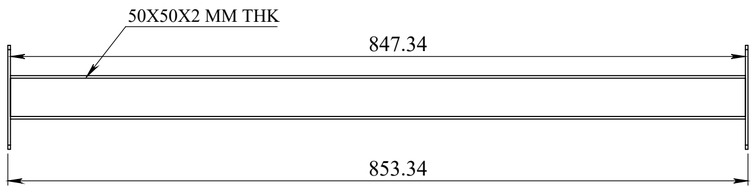

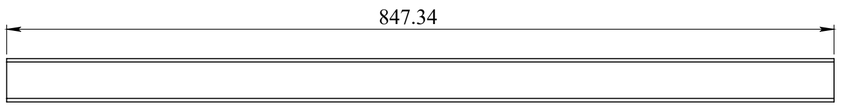

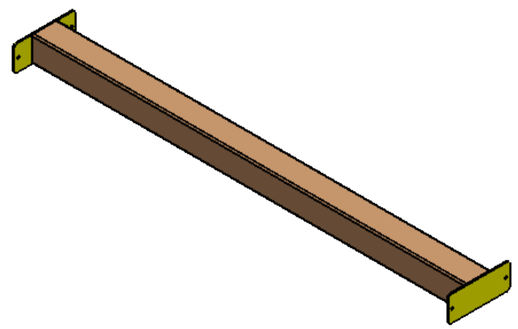

NOTE :

INTERMEDIATE SUPPORT TUBE - 50X50X2 MM THK - 960 MM L
ONE PANEL REQ QTY - 14No'S
TOTAL REQ QTY - 84 No'S
MTL - AL

SPECIAL INSTRUCTION'S :

TITLE - ROOF AUTOMATION

DWG NO - NTPL-244-PM-001-00-00-00

NIHVA TECHNOLOGIES PVT.LTD.PUNE
Website - www.nihva.com

	NAME	SIGNATURE	DATE
DRAWN	V.W.		30-07-2025
CHK'D	S.P.		31-07-2025
APPV'D	V.T.		31-07-2025

If any queries contact - design.nihva@gmail.com


ALL DIMENSION ARE IN mm | A2


PRODUCT - RETRACTABLE ROOF
PROJECT NO - NTPL-244-PM | REVISION - 07
SITE LOCATION - AHMEDABAD | WEIGHT -
MATRIAL - | QTY - 01
PROJECTION METHOD: | SCALE :


DRAWING

REV DESCRIPTION	DATE	REV NO
	30-07-2025	REV 07
1.		

ITEM NO.	PART NUMBER	DESCRIPTION	QTY.
1	NYLON WHEEL	NYLON WHEEL ∅65X18	04

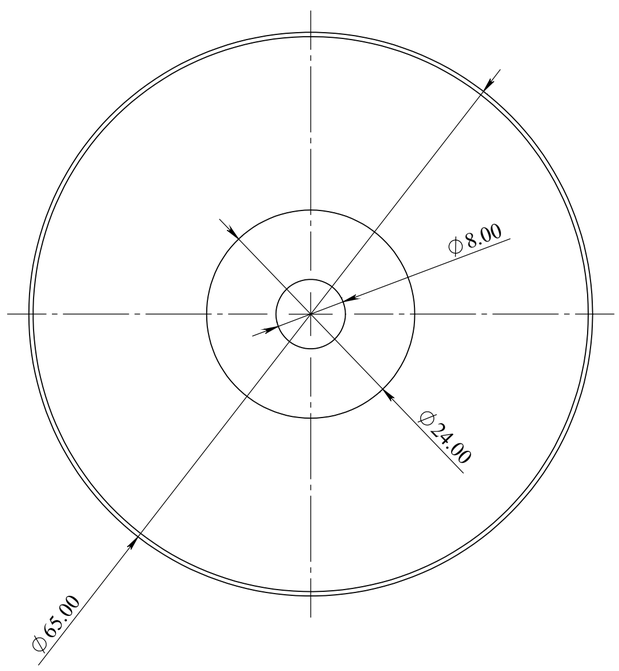

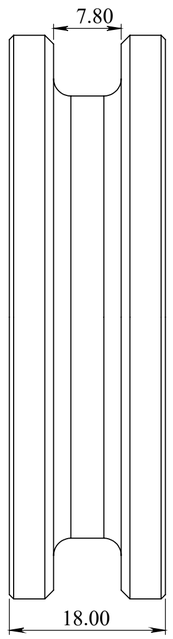

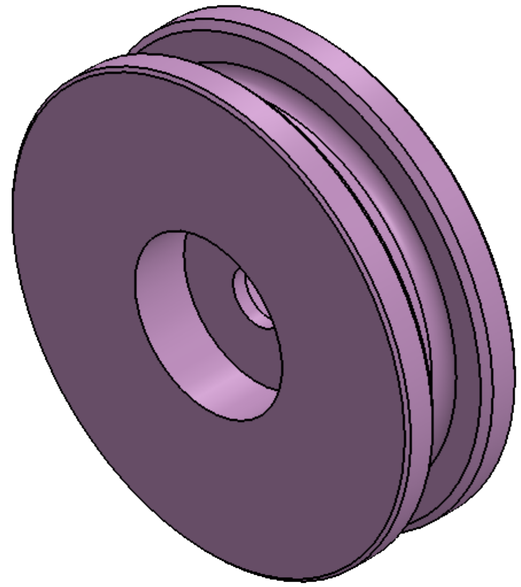

NOTE :

NYLON WHEEL - DIA 65X W 18 MM
ONE PANEL REQ QTY - 04 No'S.
TOTAL REQ QTY - 24 No'S

SPECIAL INSTRUCTION'S :

TITLE - ROOF AUTOMATION

DWG NO - NTPL-244-PM-001-00-00-00

NIHVA TECHNOLOGIES PVT.LTD.PUNE
Website - www.nihva.com


	NAME	SIGNATURE	DATE
DRAWN	V.W.		30-07-2025
CHK'D	S.P.		31-07-2025
APPV'D	V.T.		31-07-2025


PRODUCT - RETRACTABLE ROOF
PROJECT NO - NTPL-244-PM | REVISION - 07
SITE LOCATION - AHMEDABAD | WEIGHT -
MATRIAL - | QTY - 01
If any queries contact - design.nihva@gmail.com
ALL DIMENSION ARE IN mm | A2
PROJECTION METHOD:
SCALE :

DRAWING

REV DESCRIPTION	DATE	REV NO
	30-07-2025	REV 07
1.		

ITEM NO.	PART NUMBER	DESCRIPTION	QTY.
1	L PLATE	91X106X3 MM THK	04

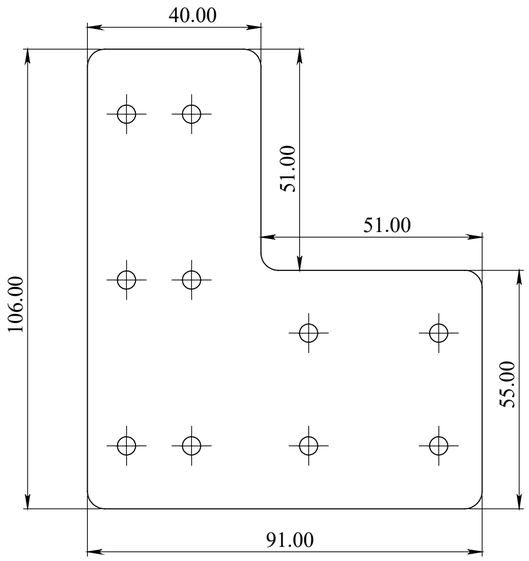

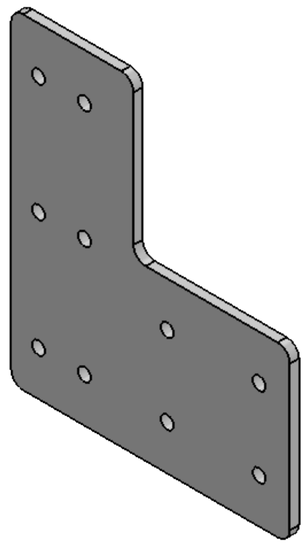

NOTE :

NAME - L PLATE
SIZE - 106X91X3 MM THK
THK - 3 MM
ONE PANEL REQ QTY - 4 No'S
TOTAL REQ QTY - 24 No'S
MTL - SS.

SPECIAL INSTRUCTION'S :

TITLE - ROOF AUTOMATION

DWG NO - NTPL-244-PM-001-00-00-00

NIHVA TECHNOLOGIES PVT.LTD.PUNE
Website - www.nihva.com


	NAME	SIGNATURE	DATE
DRAWN	V.W.		30-07-2025
CHK'D	S.P.		31-07-2025
APPV'D	V.T.		31-07-2025


PRODUCT - RETRACTABLE ROOF
PROJECT NO - NTPL-244-PM | REVISION - 07
SITE LOCATION - AHMEDABAD | WEIGHT -
MATRIAL - | QTY - 01
If any queries contact - design.nihva@gmail.com
PROJECTION METHOD: | SCALE :
ALL DIMENSION ARE IN mm | A2
SHEET 6 OF 9

DRAWING

REV DESCRIPTION	DATE	REV NO
	30-07-2025	REV 07
1.		

ITEM NO.	PART NUMBER	DESCRIPTION	QTY.
1	L ANGLE PLATE	17X52X3 MM THK	08

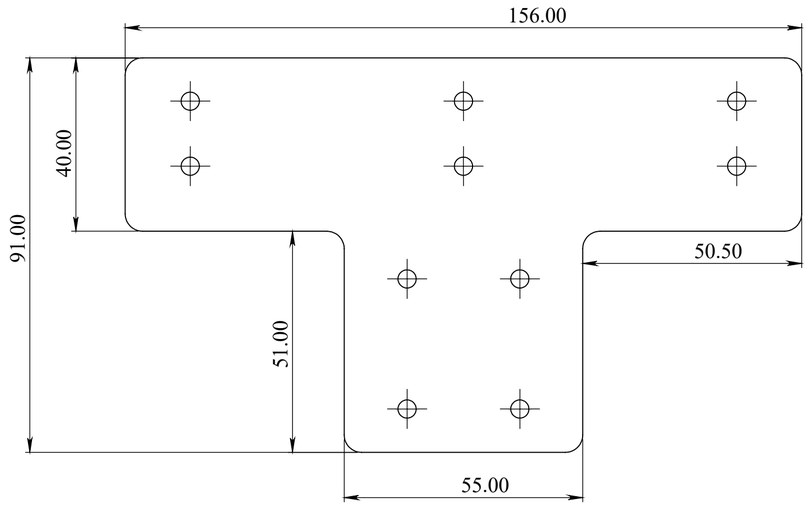

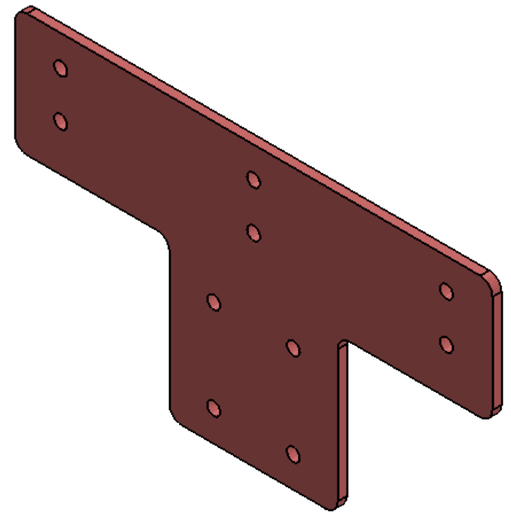

NOTE :

NAME - T PLATE
SIZE - 156X91X3 MM THK
THK - 3 MM
MTL - SS
ONE PANEL REQ QTY - 04 No'S
TOTAL REQ QTY - 26 No'S.

SPECIAL INSTRUCTION'S :

TITLE - ROOF AUTOMATION

DWG NO - NTPL-244-PM-001-00-00-00

NIHVA Technologies Pvt. Ltd.

NIHVA TECHNOLOGIES PVT.LTD.PUNE
Website - www.nihva.com

	NAME	SIGNATURE	DATE		
DRAWN	V.W.		30-07-2025	PROJECT NO - NTPL-244-PM	REVISION - 07
CHK'D	S.P.		31-07-2025	SITE LOCATION - AHMEDABAD	WEIGHT -
APPV'D	V.T.		31-07-2025	MATRIAL -	QTY - 01

If any queries contact - design.nihva@gmail.com

ALL DIMENSION ARE IN mm | A2


PROJECTION METHOD:


SCALE :


DRAWING


REV DESCRIPTION	DATE	REV NO
	30-07-2025	REV 07
1.		

ITEM NO.	PART NUMBER	DESCRIPTION	QTY.
1	RACK SUPPORT PLATE.		08

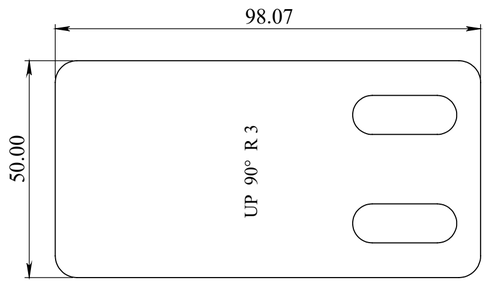

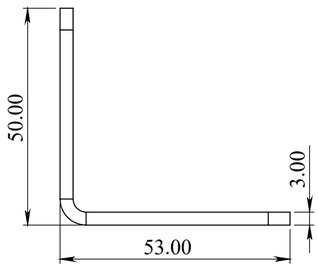

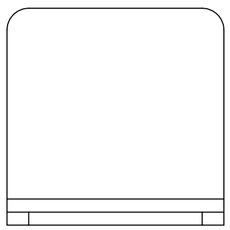

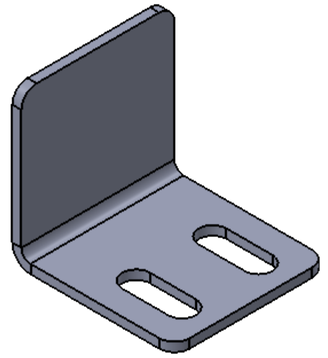

NOTE :

NAME - RACK SUPPORT PLATE
SIZE - 98.07X50X3 MM THK
THK - 3 MM
MTL - AL
ONE PANEL PANEL REQ QTY -8 No'S
TOTAL REQ QTY - 48 No'S.

SPECIAL INSTRUCTION'S :

TITLE - ROOF AUTOMATION

DWG NO - NTPL-244-PM-001-00-00-00

NIHVA Technologies Pvt. Ltd.

NIHVA TECHNOLOGIES PVT.LTD.PUNE
Website - www.nihva.com


	NAME	SIGNATURE	DATE
DRAWN	V.W.		30-07-2025
CHK'D	S.P.		31-07-2025
APPV'D	V.T.		31-07-2025


PRODUCT - RETRACTABLE ROOF
PROJECT NO - NTPL-244-PM | REVISION - 07
SITE LOCATION - AHMEDABAD | WEIGHT -
MATRIAL - | QTY - 01
If any queries contact - design.nihva@gmail.com
ALL DIMENSION ARE IN mm | A2
PROJECTION METHOD:
SCALE :
SHEET 8 OF 9

DRAWING

REV DESCRIPTION	DATE	REV NO
	30-07-2025	REV 07
1.		

ITEM NO.	PART NUMBER	DESCRIPTION	QTY.
1	.Rev_02_RACK..		3

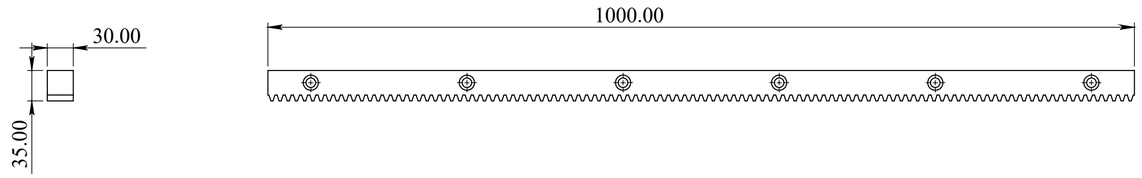

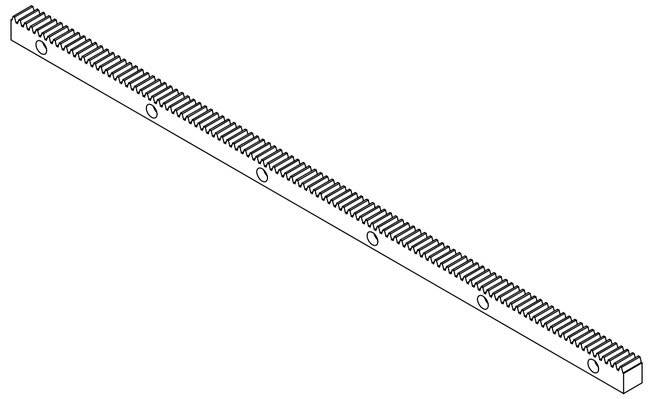

NOTE :

NAME - RACK
ONE PANEL REQ QTY - 3 No'S
TOTAL REQ QTY - 18 No'S.

SPECIAL INSTRUCTION'S :

TITLE - ROOF AUTOMATION

DWG NO - NTPL-244-PM-001-00-00-00

NIHVA TECHNOLOGIES PVT.LTD.PUNE
Website - www.nihva.com

	NAME	SIGNATURE	DATE	
DRAWN	V.W.		30-07-2025	PRODUCT - RETRACTABLE ROOF
CHK'D	S.P.		31-07-2025	PROJECT NO - NTPL-244-PM / REVISION - 07
APPV'D	V.T.		31-07-2025	SITE LOCATION - AHMEDABAD / WEIGHT -
				MATRIAL - / QTY - 01

If any queries contact - design.nihva@gmail.com

ALL DIMENSION ARE IN mm | A2

PROJECTION METHOD:

SCALE :