

DRAWING

REV DESCRIPTION	DATE	REV NO
	25-07-2025	REV 00
1.		

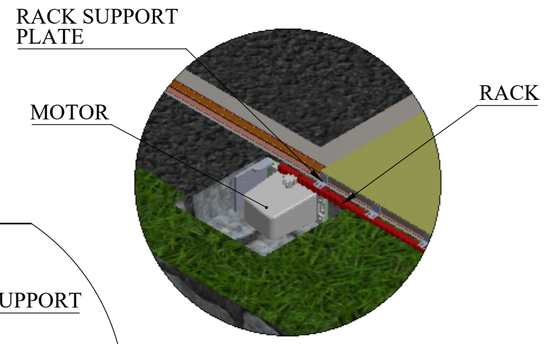


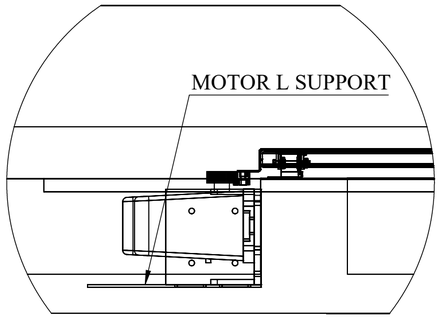


DETAIL A
SCALE 1 : 20



DETAIL B
SCALE 1 : 10

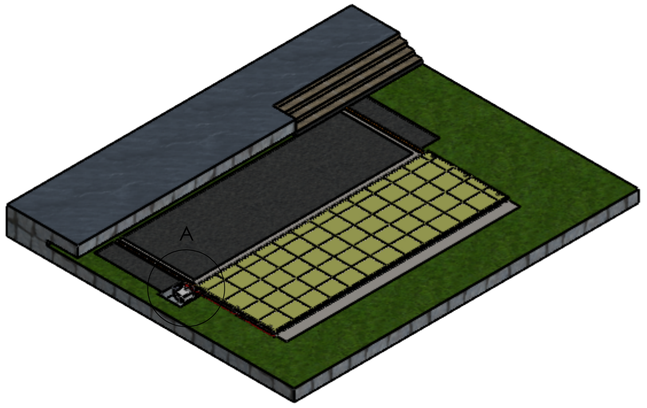



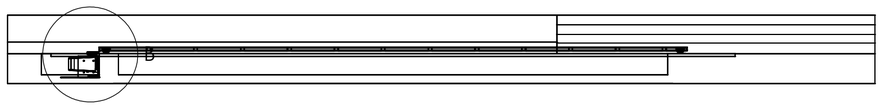

NOTE :

SPECIAL INSTRUCTION'S :

TITLE - SWIMMING POOL ENCLOSER

DWG NO - NTPL-000-PM-001-00-00-00

NIHVA Technologies Pvt. Ltd.

NIHVA TECHNOLOGIES PVT.LTD.PUNE
Website - www.nihva.com

	NAME	SIGNATURE	DATE
DRAWN	V.W.		25-07-2025
CHK'D	P.M.		27-07-2025
APPV'D	V.T.		27-07-2025

PRODUCT - SWIMMING POOL DECK

PROJECT NO - NTPL-000-PM | REVISION - 00

SITE LOCATION - | WEIGHT -

MATRIAL - | QTY - 1


If any queries contact - design.nihva@gmail.com


ALL DIMENSION ARE IN mm | A2

PROJECTION METHOD:

SCALE :


DRAWING

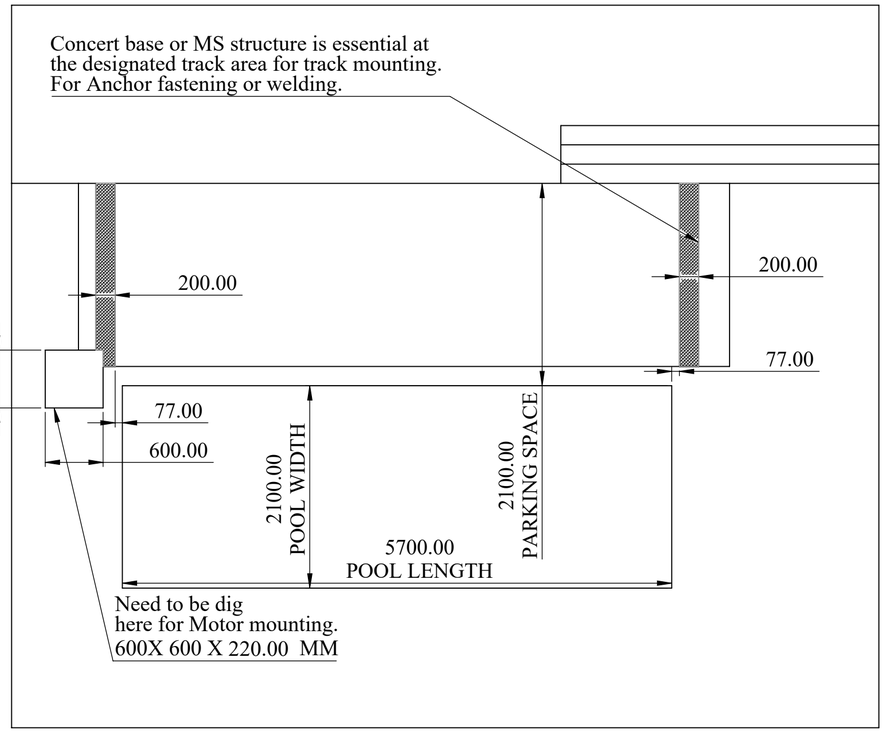


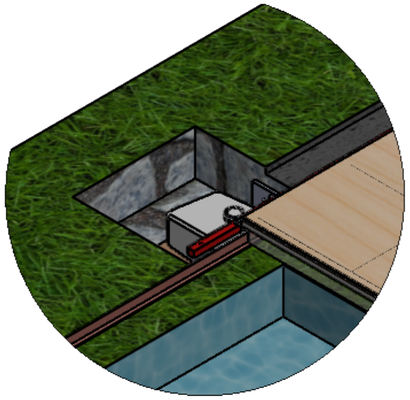


DETAIL G
SCALE 1 : 15

MOTOR ARRANGEMENT

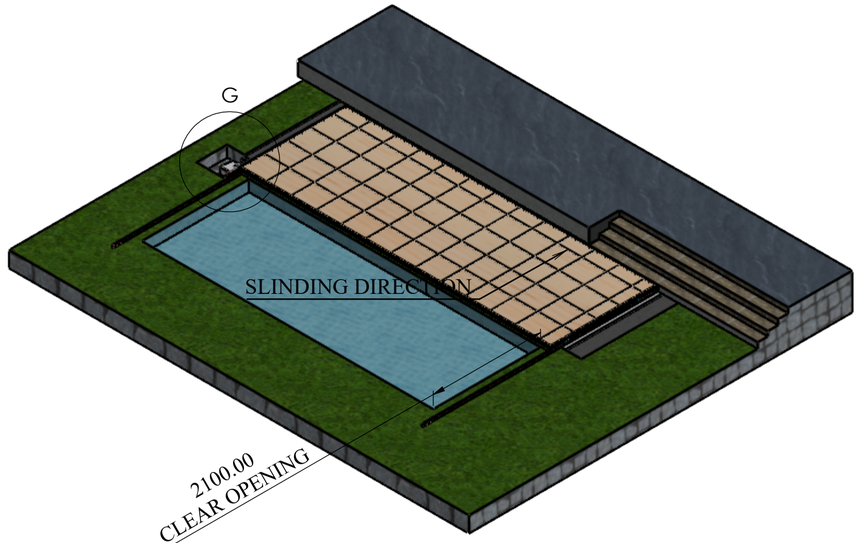

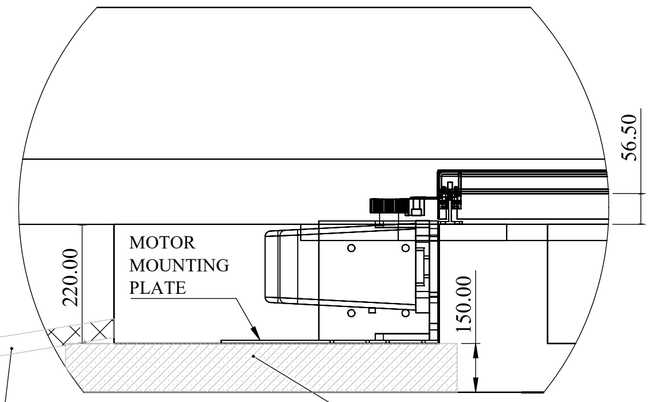

DETAIL K
SCALE 1 : 8

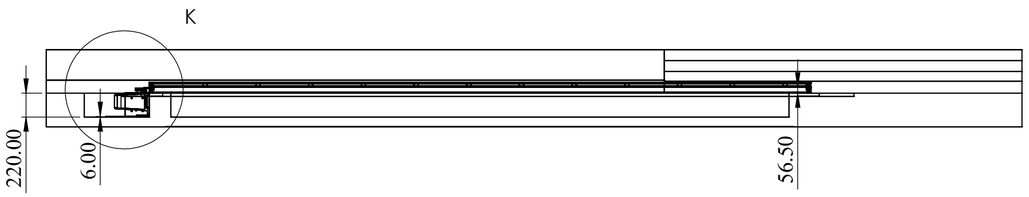

REV DESCRIPTION	DATE	REV NO
	25-07-2025	REV 00
1.		

NOTE :

All civil work is under the end client scope.

SPECIAL INSTRUCTION'S :

TITLE - SWIMMING POOL ENCLOSER

DWG NO - NTPL-000-PM-001-00-00-00

NIHVA Technologies Pvt. Ltd.

NIHVA TECHNOLOGIES PVT.LTD.PUNE
Website - www.nihva.com

	NAME	SIGNATURE	DATE
DRAWN	V.W.		25-07-2025
CHK'D	P.M.		27-07-2025
APPV'D	V.T.		27-07-2025

PRODUCT - SWIMMING POOL DECK

PROJECT NO - NTPL-000-PM | REVISION - 00

SITE LOCATION - | WEIGHT -

MATRIAL - | QTY - 1

If any queries contact - design.nihva@gmail.com

ALL DIMENSION ARE IN mm | A2

PROJECTION METHOD:

SCALE :