

DRAWING

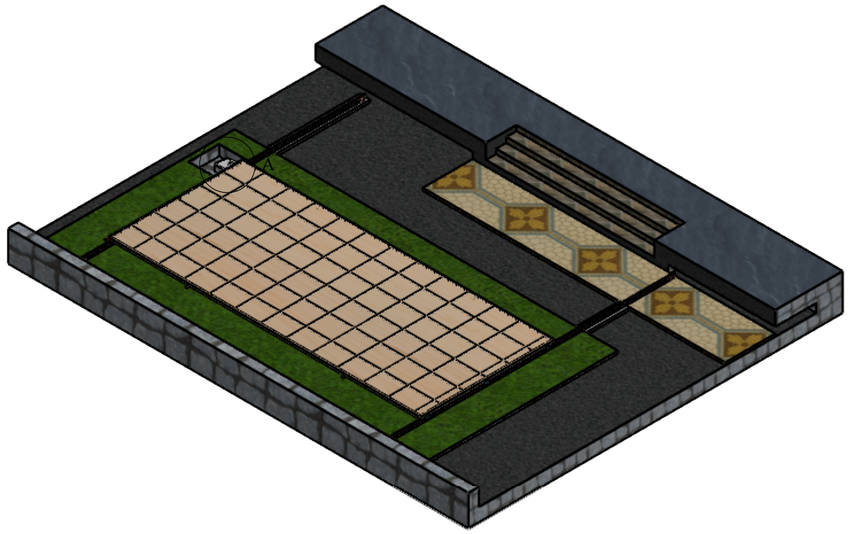






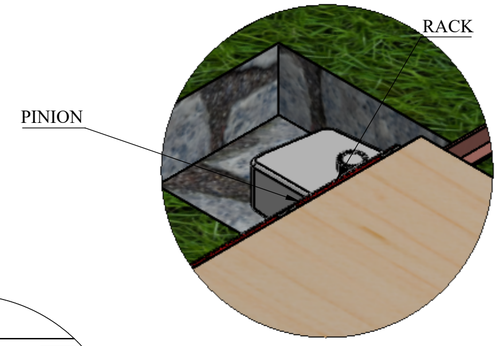

DETAIL A
SCALE 1 : 10

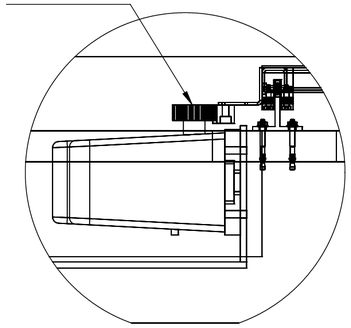

DETAIL B
SCALE 1 : 7



REV DESCRIPTION	DATE	REV NO
	25-08-2025	REV 00
1.		

NOTE :

Main Assembly

SPECIAL INSTRUCTION'S :

TITLE - SWIMMING POOL ENCLOSER

DWG NO - NTPL-294-PM-001-00-00-00

NIHVA Technologies Pvt. Ltd.

NIHVA TECHNOLOGIES PVT.LTD.PUNE
Website - www.nihva.com

	NAME	SIGNATURE	DATE
DRAWN	V.W.		25-08-2025
CHK'D	B.S.		29-08-2025
APPV'D	V.T.		30-08-2025

PRODUCT - SWIMMING POOL DECK

PROJECT NO - NTPL-294-PM | REVISION - 00

SITE LOCATION - PUNE | WEIGHT -

MATRIAL - | QTY - 1

If any queries contact - Design@nihva.com


ALL DIMENSION ARE IN mm | A2


PROJECTION METHOD:

SCALE :

DRAWING

ITEM NO.	PART NUMBER	DESCRIPTION	QTY.
1	LIFT TRACK -(T GUIDE) , SIZE -50X50X8 MM THK		2
2	PANEL ASM WITH BEARING BLOCK		1
3	closing sheet...		2
4	CLOSING SHEET 2...		2
5	Chemical Anchor Bolt_M8x100 MM L	Anker_M8x80	16
6	MOTOR MOUNTING ASM		1
7	50 mm Caster Wheel - Copy - Copy		4
8	CIVIL BASE.._.		1

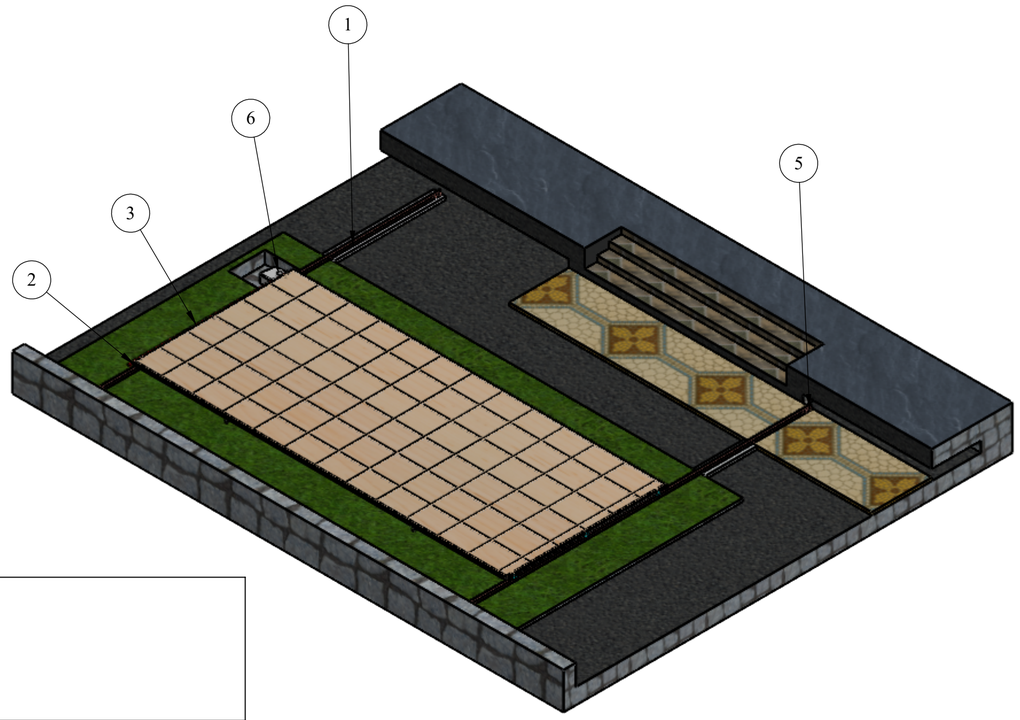

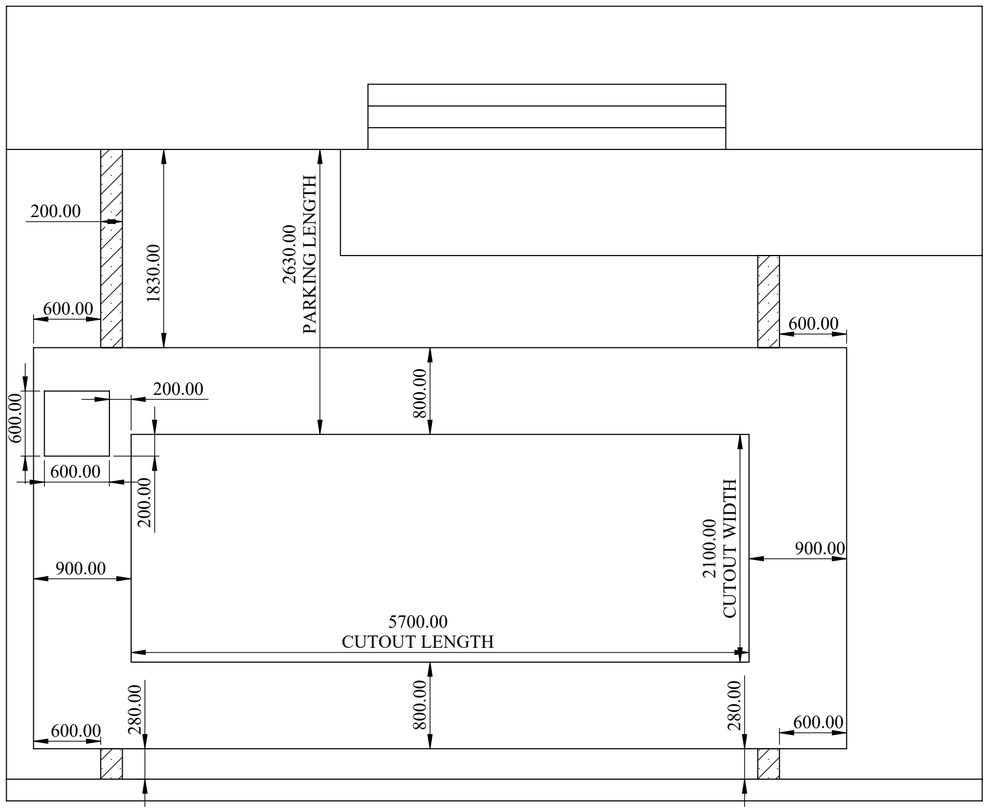

REV DESCRIPTION	DATE	REV NO
	25-08-2025	REV 00
1.		

NOTE :

Main Assembly

SPECIAL INSTRUCTION'S :

TITLE - SWIMMING POOL ENCLOSER

DWG NO - NTPL-294-PM-001-00-00-00

NIHVA Technologies Pvt. Ltd.

NIHVA TECHNOLOGIES PVT.LTD.PUNE
Website - www.nihva.com

	NAME	SIGNATURE	DATE
DRAWN	V.W.		25-08-2025
CHK'D	B.S.		29-08-2025
APPV'D	V.T.		30-08-2025

PRODUCT - SWIMMING POOL DECK

PROJECT NO - NTPL-294-PM | REVISION - 00

SITE LOCATION - PUNE | WEIGHT -

MATRIAL - | QTY - 1


If any queries contact - Design@nihva.com


ALL DIMENSION ARE IN mm | A2

PROJECTION METHOD:


SCALE :

DRAWING

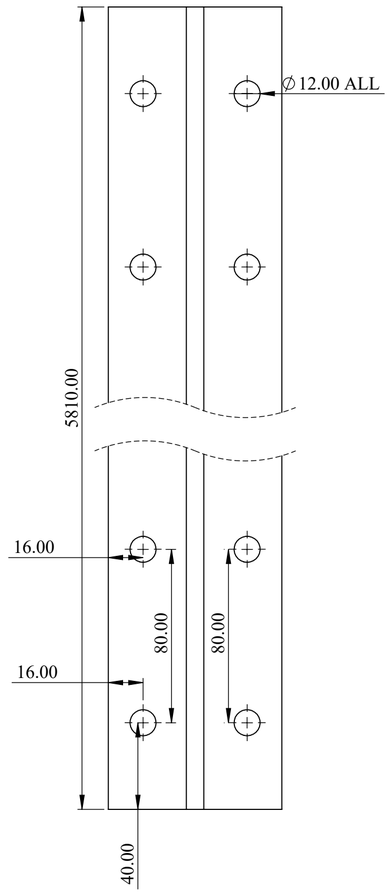

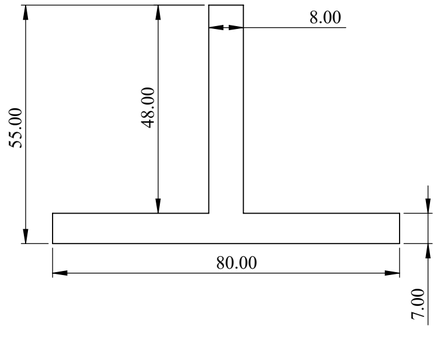

ITEM NO.	PART NUMBER	DESCRIPTION	QTY.
1	LIFT TRACK -(T GUIDE) , SIZE - 50X50X8 MM THK		2

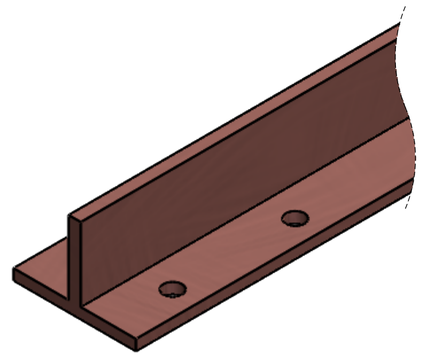

REV DESCRIPTION	DATE	REV NO
	25-08-2025	REV 00
1.		

NOTE :

Name: Lift Track
Size : T-GUIDE, 80x55x8 mm
Mtl : SS
Qty : 02 No's

SPECIAL INSTRUCTION'S :

TITLE - SWIMMING POOL ENCLOSER

DWG NO - NTPL-294-PM-001-00-00-00

NIHVA Technologies Pvt. Ltd.


NIHVA TECHNOLOGIES PVT.LTD.PUNE
Website - www.nihva.com

	NAME	SIGNATURE	DATE
DRAWN	V.W.		25-08-2025
CHK'D	B.S.		29-08-2025
APPV'D	V.T.		30-08-2025

PRODUCT - SWIMMING POOL DECK
PROJECT NO - NTPL-294-PM | REVISION - 00
SITE LOCATION - PUNE | WEIGHT -
MATRIAL - | QTY - 1
If any queries contact - Design@nihva.com | PROJECTION METHOD: | SCALE :
ALL DIMENSION ARE IN mm | A2 | SHEET 3 OF 19

DRAWING

ITEM NO.	PART NUMBER	DESCRIPTION	QTY.
1	PANEL...	SS	1
2	BEARING BLOCK ASM - T45-A		6
3	SS PLATE 6100 X 2630 X 3 MM THK...	SS	1
4	RACK...	STD (M4 RACK, 30x8x1000 mm, ZINC COATED WITH SPACERS AND SCREWS.)	2
5	RACK CUT PART...	STD (M4 RACK, 30x8x1000 mm, ZINC COATED WITH SPACERS AND SCREWS.)	1
6	RACK SUPPORT PLATE 50x87.85x4mm thk	ss	8

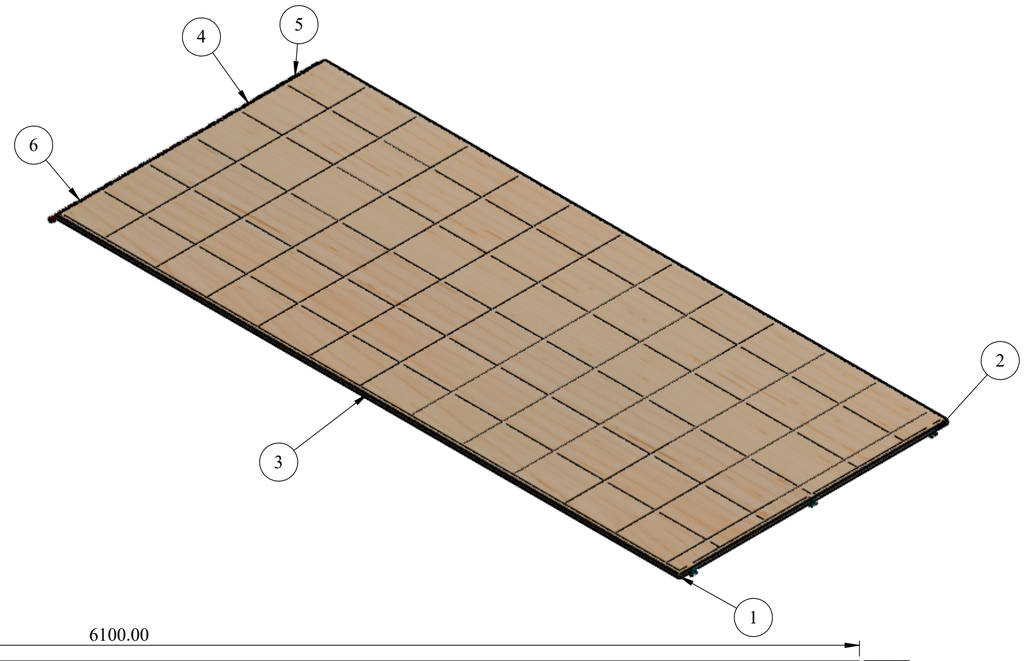



REV DESCRIPTION	DATE	REV NO
	25-08-2025	REV 00
1.		

NOTE :

Name : Panel ASM

SPECIAL INSTRUCTION'S :

TITLE - SWIMMING POOL ENCLOSER

DWG NO - NTPL-294-PM-001-00-00-00

NIHVA Technologies Pvt. Ltd.

NIHVA TECHNOLOGIES PVT.LTD.PUNE
Website - www.nihva.com

	NAME	SIGNATURE	DATE
DRAWN	V.W.		25-08-2025
CHK'D	B.S.		29-08-2025
APPV'D	V.T.		30-08-2025

PRODUCT - SWIMMING POOL DECK

PROJECT NO - NTPL-294-PM | REVISION - 00

SITE LOCATION - PUNE | WEIGHT -

MATRIAL - | QTY - 1

If any queries contact - Design@nihva.com


ALL DIMENSION ARE IN mm | A2

PROJECTION METHOD:

SCALE :

DRAWING

ITEM NO.	PART NUMBER	DESCRIPTION	QTY.
1	PANEL...	SS	1

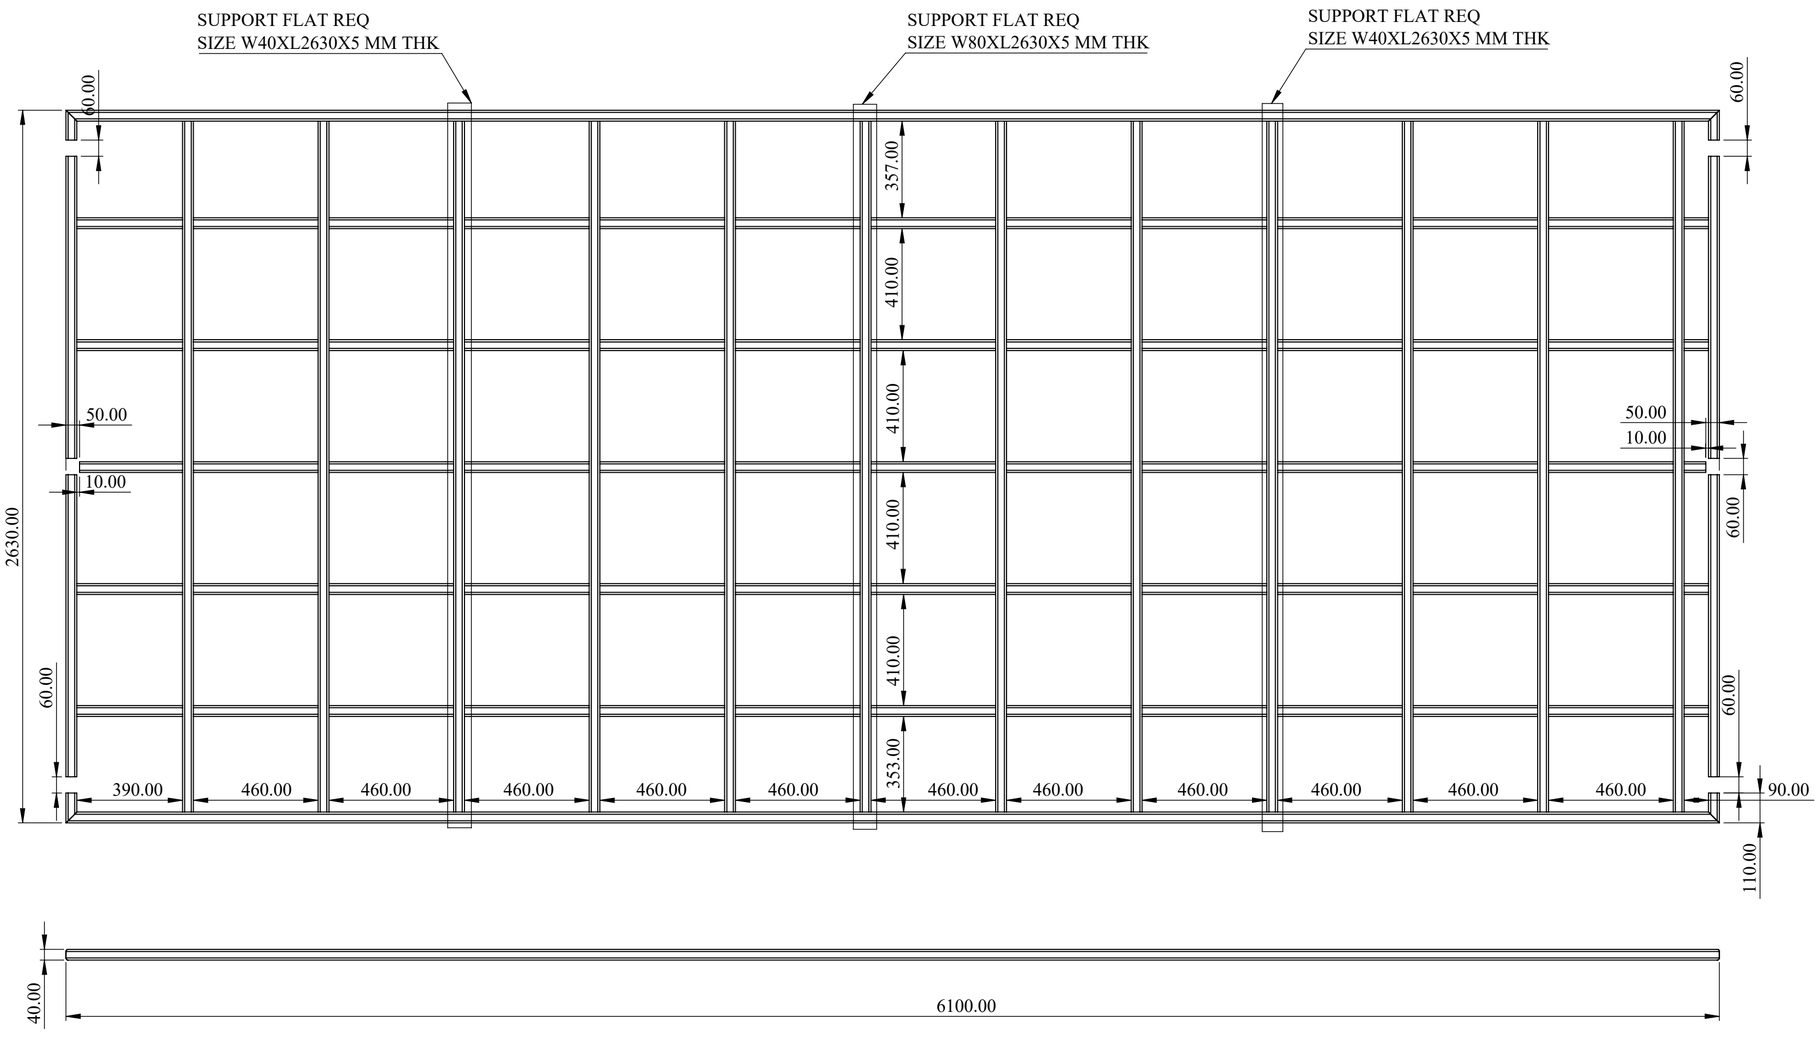

REV DESCRIPTION	DATE	REV NO
	25-08-2025	REV 00
1.		

NOTE :

Name : Deck Panel
Mtl : SS
Size : 2630X6100 mm L

SPECIAL INSTRUCTION'S :

TITLE - SWIMMING POOL ENCLOSER

DWG NO - NTPL-294-PM-001-00-00-00

NIHVA Technologies Pvt. Ltd.

NIHVA TECHNOLOGIES PVT.LTD.PUNE
Website - www.nihva.com


	NAME	SIGNATURE	DATE
DRAWN	V.W.		25-08-2025
CHK'D	B.S.		29-08-2025
APPV'D	V.T.		30-08-2025


PRODUCT - SWIMMING POOL DECK
PROJECT NO - NTPL-294-PM | REVISION - 00
SITE LOCATION - PUNE | WEIGHT -
MATRIAL - | QTY - 1
If any queries contact - Design@nihva.com | PROJECTION METHOD: | SCALE :
ALL DIMENSION ARE IN mm | A2 | SHEET 5 OF 19


DRAWING


ITEM NO.	PART NUMBER	DESCRIPTION	QTY.
1	BEARING BLOCK (T-GUIDE)	68X60X50 MM (VMC PART)	1
2	SKF BALL BEARING SKF 6000-2Z/C3		2
3	SHOULDER BOLT 10 X 50 MM L	SS	2
4	SKF BALL BEARING 8 SIZE 8X19X7 MM THK	SS	2
5	SHOULDER BOLT 8 X 40 MM L	SS	2

REV DESCRIPTION	DATE	REV NO
	25-08-2025	REV 00
1.		

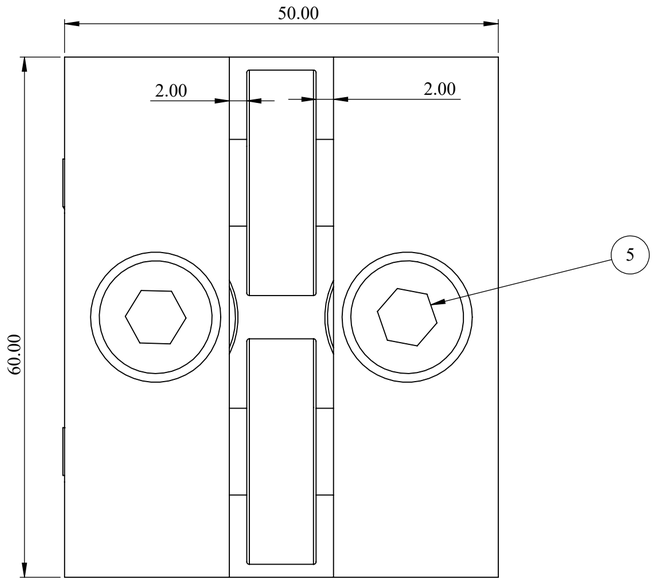

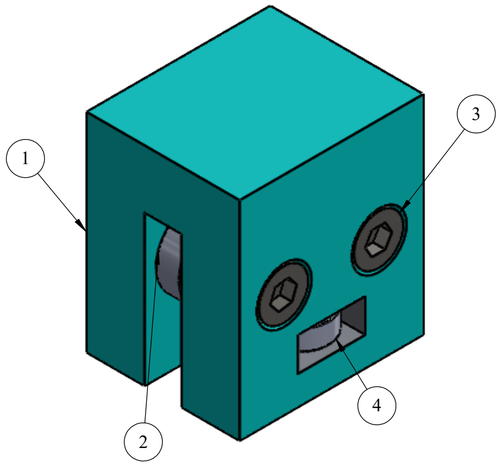

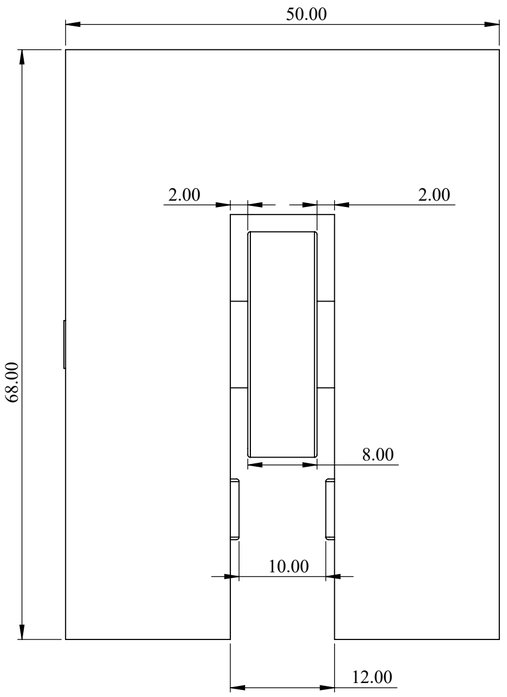

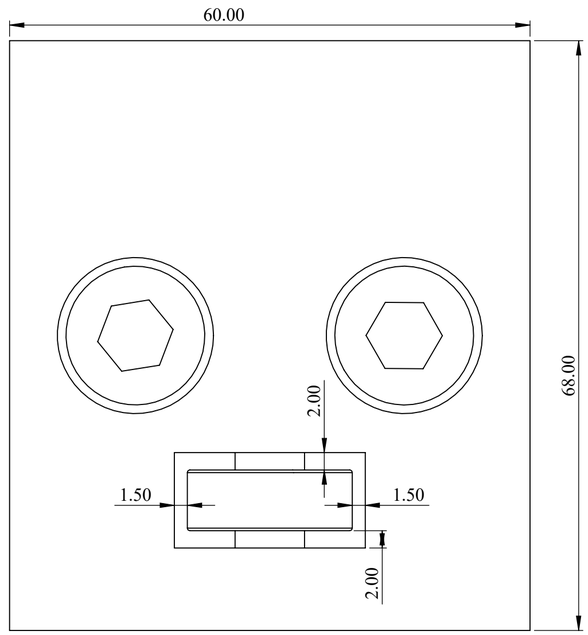

NOTE :

Name : Bearing Block ASM
Qty : 06 No's

SPECIAL INSTRUCTION'S :

TITLE - SWIMMING POOL ENCLOSER

DWG NO - NTPL-294-PM-001-00-00-00

NIHVA Technologies Pvt. Ltd.

NIHVA TECHNOLOGIES PVT.LTD.PUNE
Website - www.nihva.com


	NAME	SIGNATURE	DATE
DRAWN	V.W.		25-08-2025
CHK'D	B.S.		29-08-2025
APPV'D	V.T.		30-08-2025


PRODUCT - SWIMMING POOL DECK
PROJECT NO - NTPL-294-PM
REVISION - 00
SITE LOCATION - PUNE
WEIGHT -
MATRIAL -
QTY - 1
SCALE :
PROJECTION METHOD:
If any queries contact - Design@nihva.com
ALL DIMENSION ARE IN mm
A2


DRAWING


ITEM NO.	PART NUMBER	DESCRIPTION	QTY.
1	BEARING BLOCK (T-GUIDE)	68X60X50 MM (VMC PART)	06

REV DESCRIPTION	DATE	REV NO
	25-08-2025	REV 00
1.		

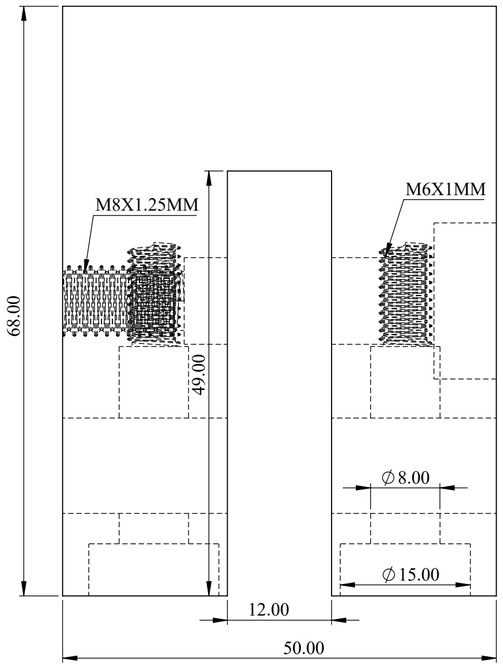

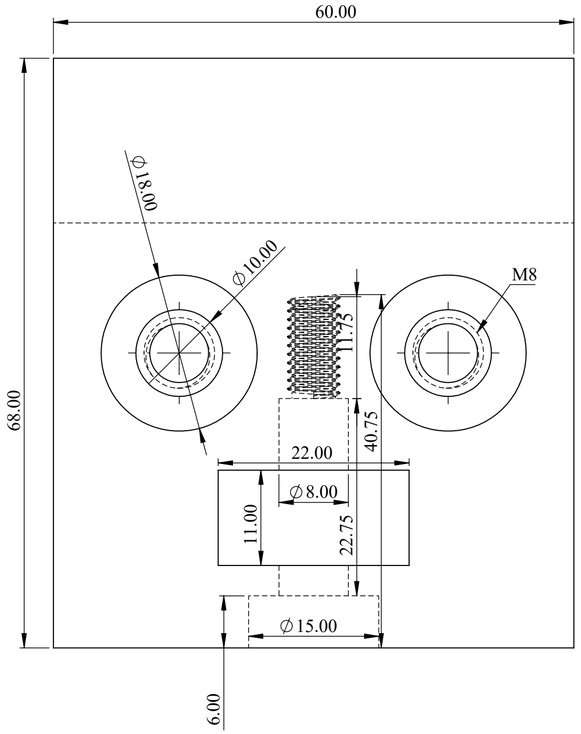

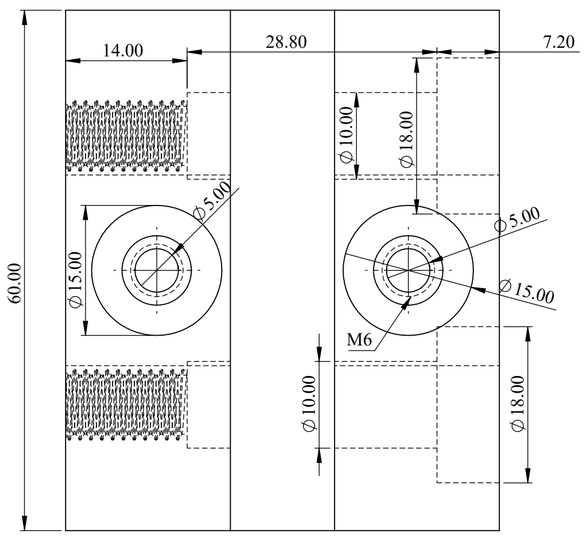

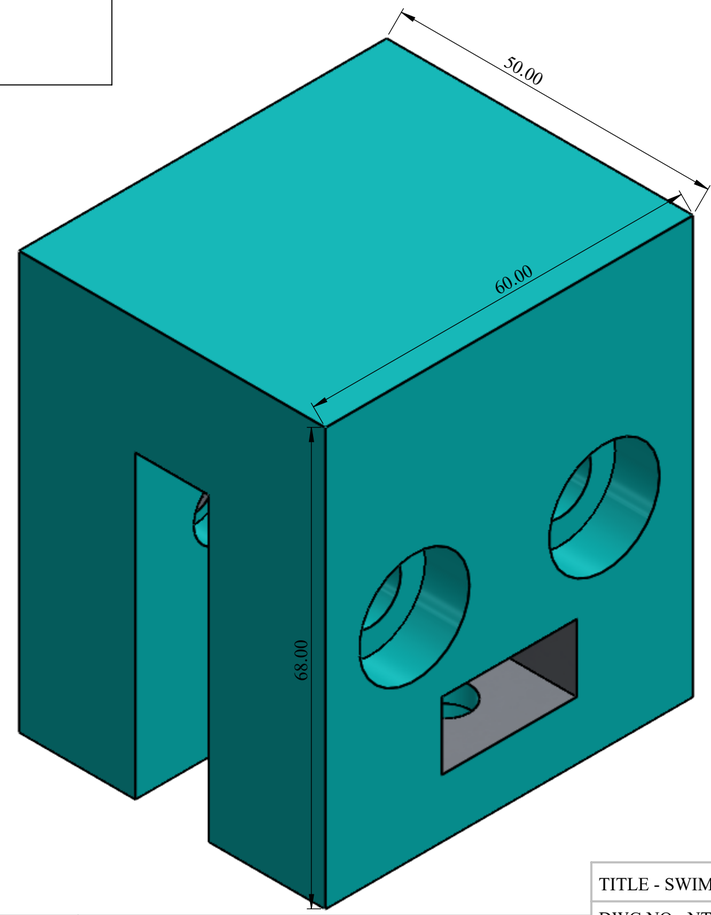

NOTE :

Name: Bearing Block
Size : 68X60X50 (VMC MACHININING)
Mtl : SS
Qty : 06 no's.

SPECIAL INSTRUCTION'S :

TITLE - SWIMMING POOL ENCLOSER

DWG NO - NTPL-294-PM-001-00-00-00

NIHVA Technologies Pvt. Ltd.

NIHVA TECHNOLOGIES PVT.LTD.PUNE
Website - www.nihva.com

	NAME	SIGNATURE	DATE
DRAWN	V.W.		25-08-2025
CHK'D	B.S.		29-08-2025
APPV'D	V.T.		30-08-2025


PRODUCT - SWIMMING POOL DECK
PROJECT NO - NTPL-294-PM
REVISION - 00
SITE LOCATION - PUNE
WEIGHT -
MATRIAL -
QTY - 1
SCALE :

If any queries contact - Design@nihva.com
ALL DIMENSION ARE IN mm
A2
PROJECTION METHOD:


DRAWING

ITEM NO.	PART NUMBER	DESCRIPTION	QTY.
1	SKF BALL BEARING SKF 6000-2Z/C3		8

REV DESCRIPTION	DATE	REV NO
	25-08-2025	REV 00
1.		

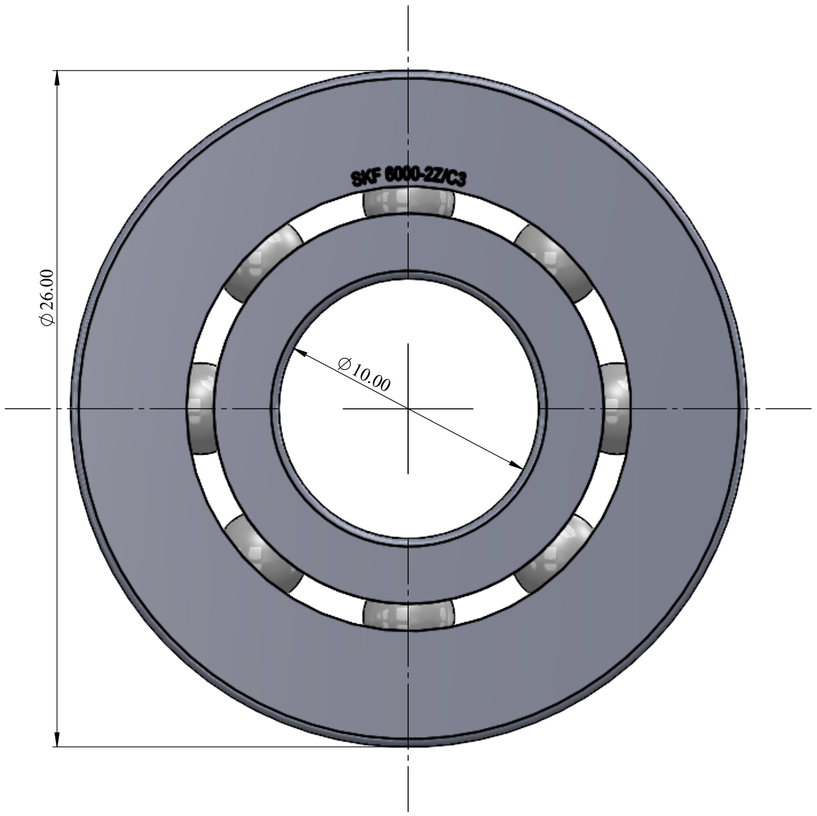



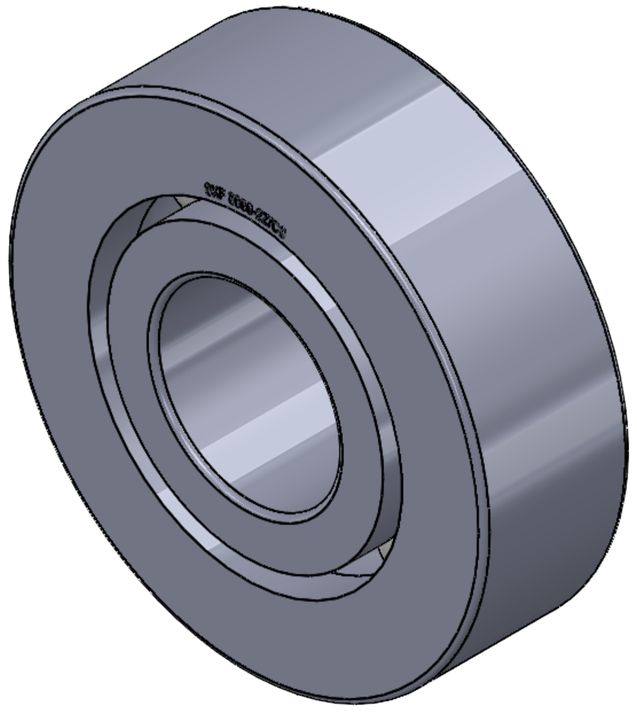

NOTE :

Name: SKF 6000-2Z/C3
Size : 10X26X8 MM THK
Qty : 12 No's.

SPECIAL INSTRUCTION'S :

TITLE - SWIMMING POOL ENCLOSER

DWG NO - NTPL-294-PM-001-00-00-00

NIHVA Technologies Pvt. Ltd.

NIHVA TECHNOLOGIES PVT.LTD.PUNE
Website - www.nihva.com


	NAME	SIGNATURE	DATE
DRAWN	V.W.		25-08-2025
CHK'D	B.S.		29-08-2025
APPV'D	V.T.		30-08-2025


PRODUCT - SWIMMING POOL DECK
PROJECT NO - NTPL-294-PM
REVISION - 00
SITE LOCATION - PUNE
WEIGHT -
MATRIAL -
QTY - 1
If any queries contact - Design@nihva.com
PROJECTION METHOD:
SCALE :
ALL DIMENSION ARE IN mm
A2


DRAWING

REV DESCRIPTION	DATE	REV NO
	25-08-2025	REV 00
1.		

ITEM NO.	PART NUMBER	DESCRIPTION	QTY.
1	SHOULDER BOLT 10 X 50 MM L	SS	8

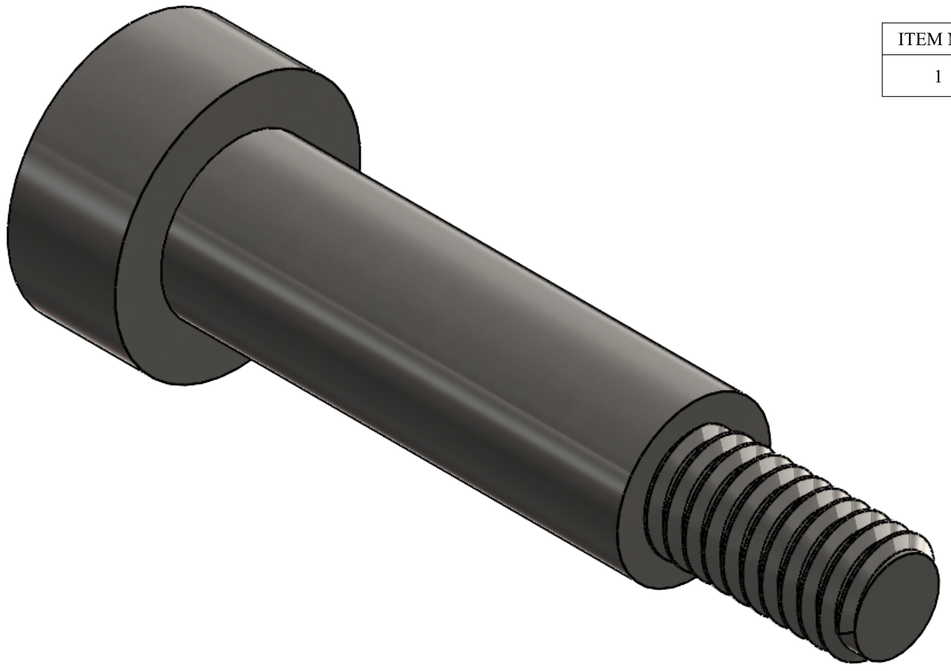

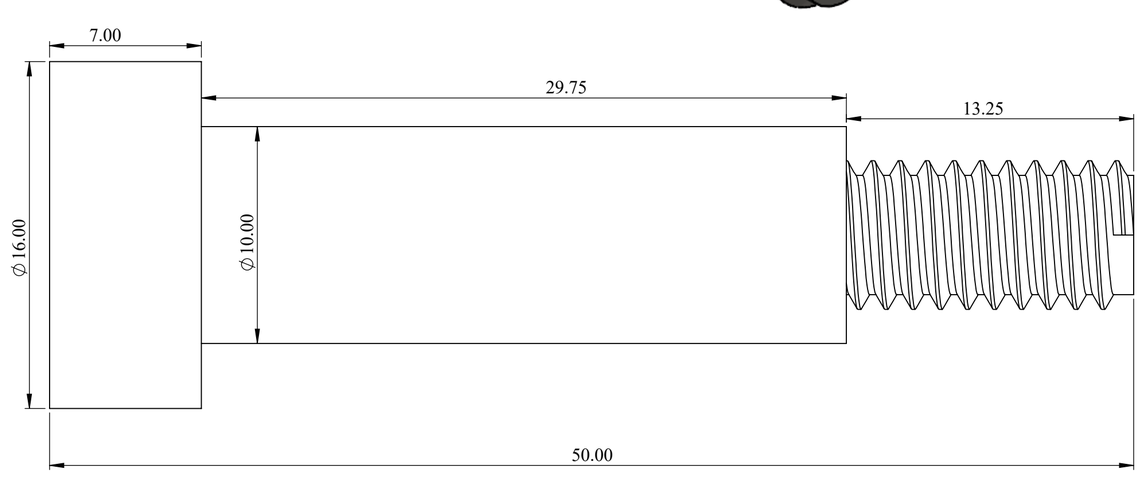

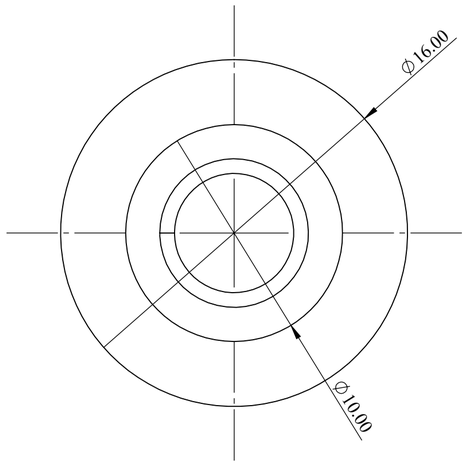

NOTE :

Name: Shoulder Bolt NATR 10
Size : 10x50 mm L & Thread length 13.25mm
Mtl : SS
Qty : 12 No's.

SPECIAL INSTRUCTION'S :

TITLE - SWIMMING POOL ENCLOSER

DWG NO - NTPL-294-PM-001-00-00-00

NIHVA Technologies Pvt. Ltd.

NIHVA TECHNOLOGIES PVT.LTD.PUNE
Website - www.nihva.com


	NAME	SIGNATURE	DATE
DRAWN	V.W.		25-08-2025
CHK'D	B.S.		29-08-2025
APPV'D	V.T.		30-08-2025

PRODUCT - SWIMMING POOL DECK
PROJECT NO - NTPL-294-PM
REVISION - 00
SITE LOCATION - PUNE
WEIGHT -
MATRIAL -
QTY - 1
If any queries contact - Design@nihva.com
PROJECTION METHOD:
SCALE :
ALL DIMENSION ARE IN mm
A2


DRAWING

ITEM NO.	PART NUMBER	DESCRIPTION	QTY.
1	SKF BALL BEARING 8 SIZE 8X19X7 MM THK	SS	8

REV DESCRIPTION	DATE	REV NO
	25-08-2025	REV 00
1.		

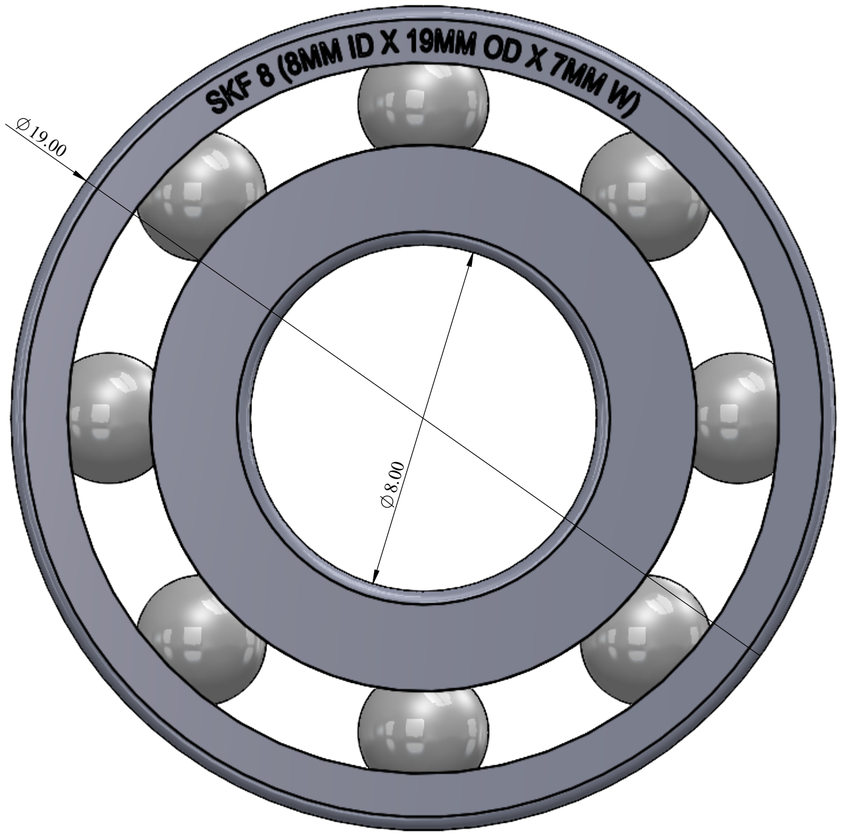



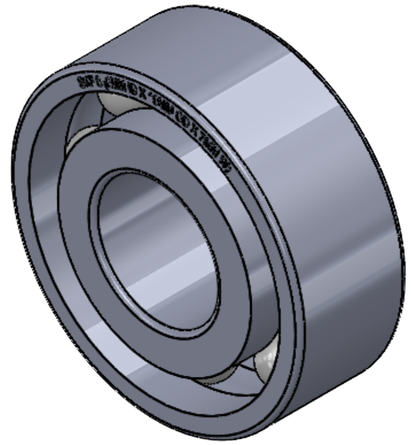

NOTE :

Name: SKF Bearing 8
Size : 8X19X7 MM THK
Qty : 12 No's

SPECIAL INSTRUCTION'S :

TITLE - SWIMMING POOL ENCLOSER

DWG NO - NTPL-294-PM-001-00-00-00

NIHVA Technologies Pvt. Ltd.

NIHVA TECHNOLOGIES PVT.LTD.PUNE
Website - www.nihva.com

	NAME	SIGNATURE	DATE	PRODUCT - SWIMMING POOL DECK	
DRAWN	V.W.		25-08-2025	PROJECT NO - NTPL-294-PM	REVISION - 00
CHK'D	B.S.		29-08-2025	SITE LOCATION - PUNE	WEIGHT -
APPV'D	V.T.		30-08-2025	MATRIAL -	QTY - 1


If any queries contact - Design@nihva.com

ALL DIMENSION ARE IN mm | A2

PROJECTION METHOD:


SCALE :


DRAWING

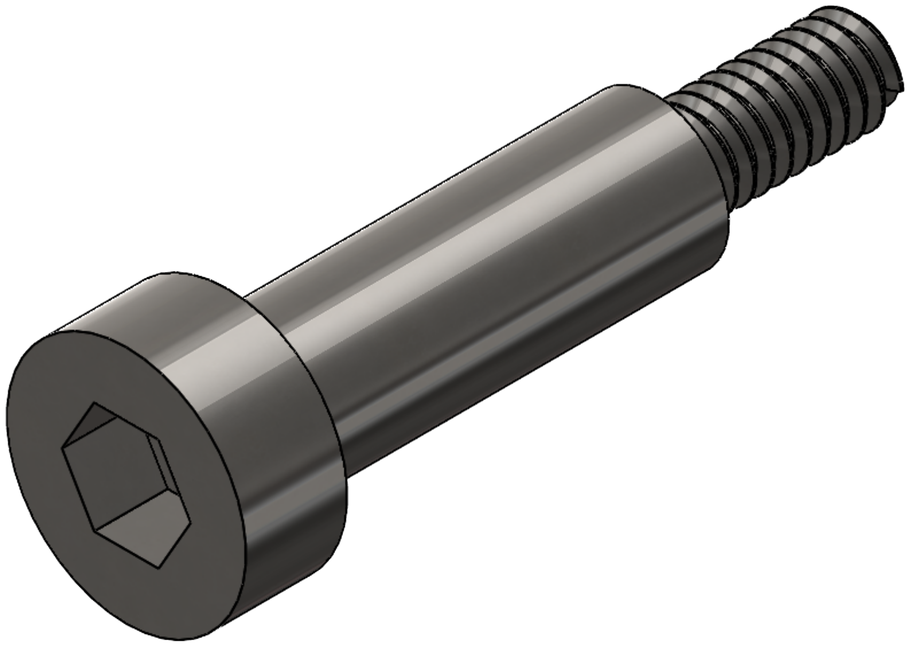

ITEM NO.	PART NUMBER	DESCRIPTION	QTY.
1	SHOULDER BOLT 8 X 40 MM L	SS	8

REV DESCRIPTION	DATE	REV NO
	25-08-2025	REV 00
1.		

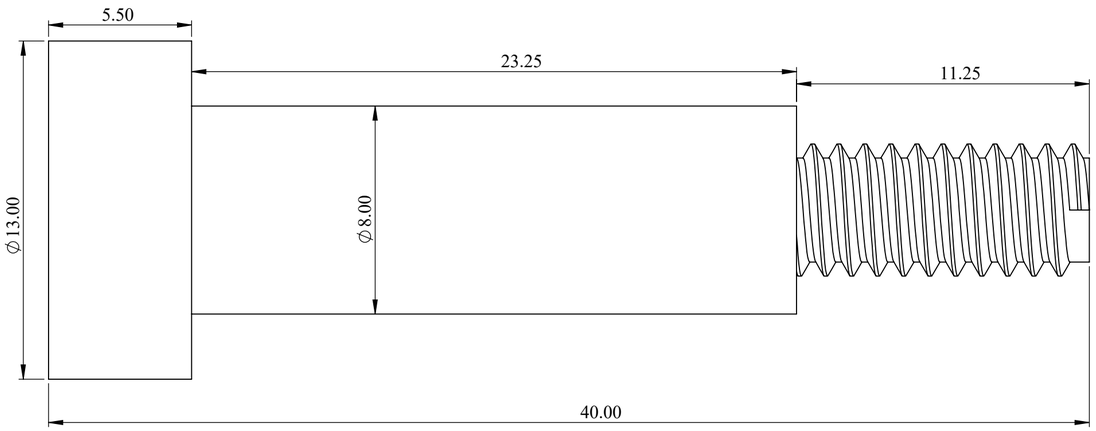

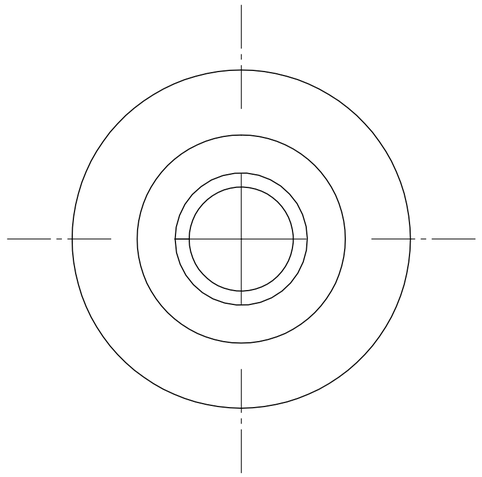

NOTE :

Name: Shoulder Bolt NATR 8
Size :8x40 mm L & Thread length 11.25mm
Mtl : SS
Qty : 12 No's.

SPECIAL INSTRUCTION'S :

TITLE - SWIMMING POOL ENCLOSER

DWG NO - NTPL-294-PM-001-00-00-00

NIHVA Technologies Pvt. Ltd.

NIHVA TECHNOLOGIES PVT.LTD.PUNE
Website - www.nihva.com


	NAME	SIGNATURE	DATE
DRAWN	V.W.		25-08-2025
CHK'D	B.S.		29-08-2025
APPV'D	V.T.		30-08-2025

PRODUCT - SWIMMING POOL DECK
PROJECT NO - NTPL-294-PM | REVISION - 00
SITE LOCATION - PUNE | WEIGHT -
MATRIAL - | QTY - 1

If any queries contact - Design@nihva.com
ALL DIMENSION ARE IN mm | A2
PROJECTION METHOD:
SCALE :

DRAWING

ITEM NO.	PART NUMBER	DESCRIPTION	QTY.
1	SS PLATE 6100 X 2630 X 3 MM THK...	SS	1

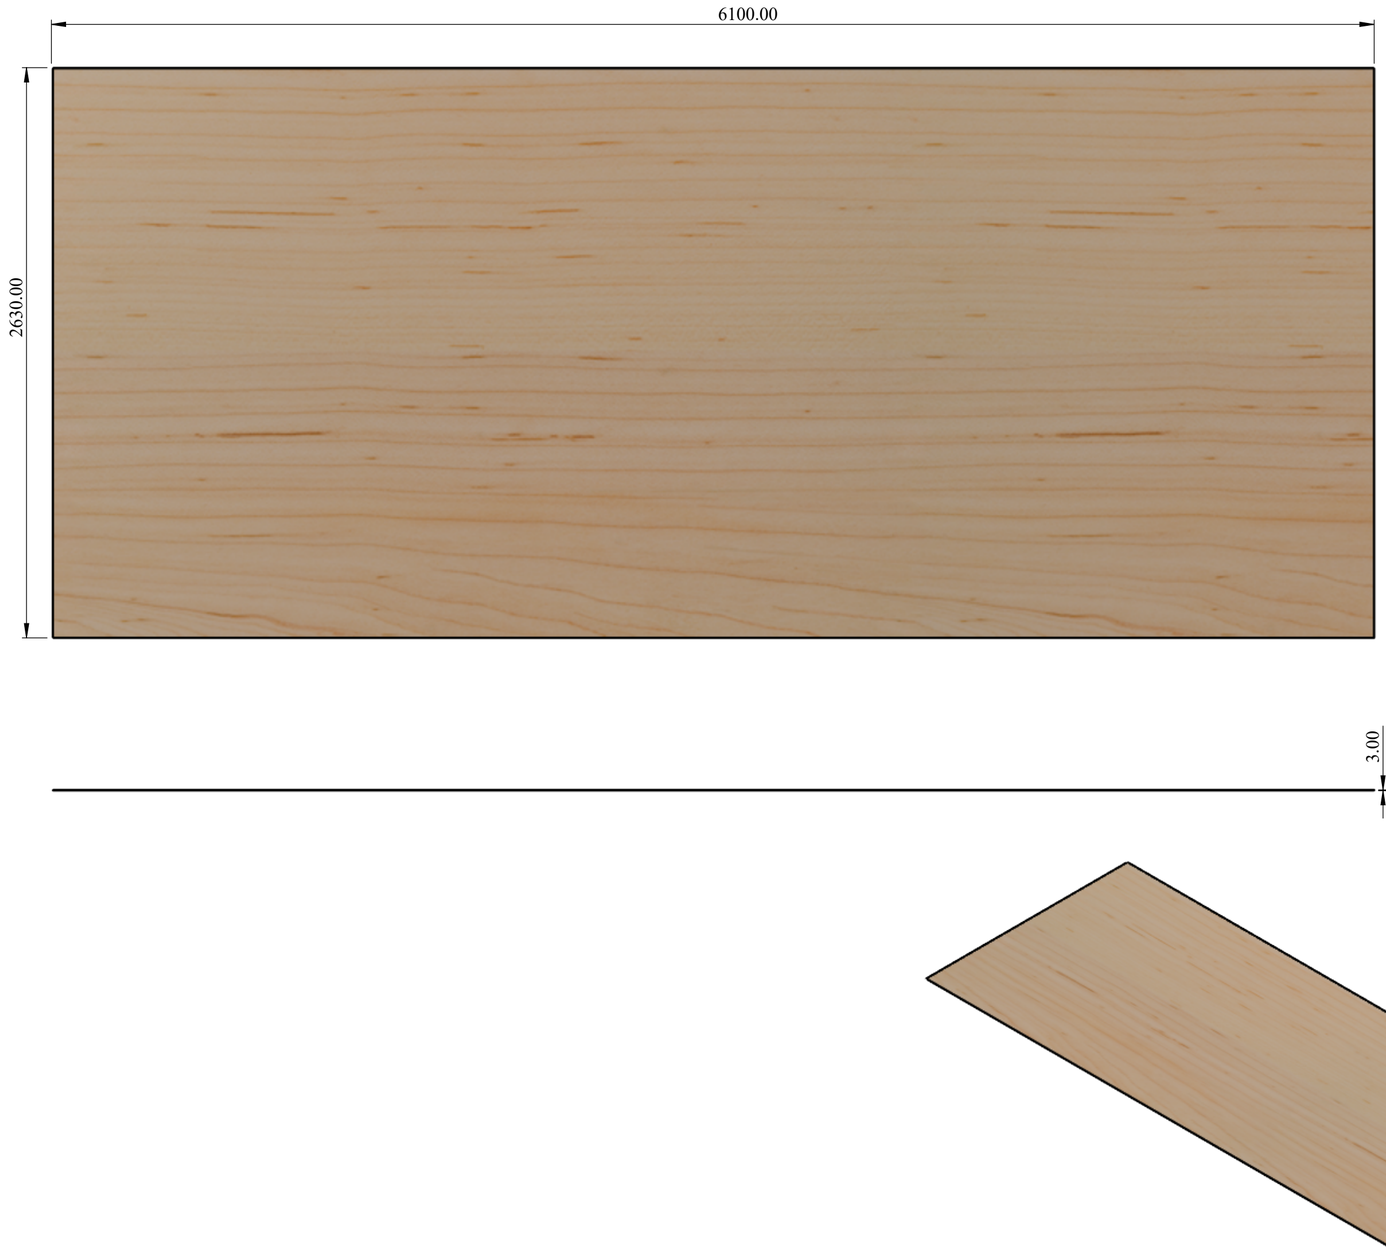

REV DESCRIPTION	DATE	REV NO
	25-08-2025	REV 00
1.		

NOTE :

Name: Covering Plate
Size : 2630x6100 mm
Thk : 3 mm
Mtl : SS
Qty : 1 No's.

SPECIAL INSTRUCTION'S :

TITLE - SWIMMING POOL ENCLOSER

DWG NO - NTPL-294-PM-001-00-00-00

NIHVA TECHNOLOGIES PVT.LTD.PUNE
Website - www.nihva.com


	NAME	SIGNATURE	DATE
DRAWN	V.W.		25-08-2025
CHK'D	B.S.		29-08-2025
APPV'D	V.T.		30-08-2025


PRODUCT - SWIMMING POOL DECK
PROJECT NO - NTPL-294-PM | REVISION - 00
SITE LOCATION - PUNE | WEIGHT -
MATRIAL - | QTY - 1
If any queries contact - Design@nihva.com | PROJECTION METHOD: | SCALE :
ALL DIMENSION ARE IN mm | A2 | SHEET 12 OF 19

DRAWING

REV DESCRIPTION	DATE	REV NO
	25-08-2025	REV 00
1.		

ITEM NO.	PART NUMBER	DESCRIPTION	QTY.
1	RACK...	STD (M4 RACK, 30x8x1000 mm, ZINC COATED WITH SPACERS AND SCREWS.)	3

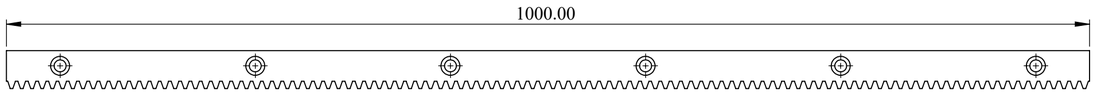

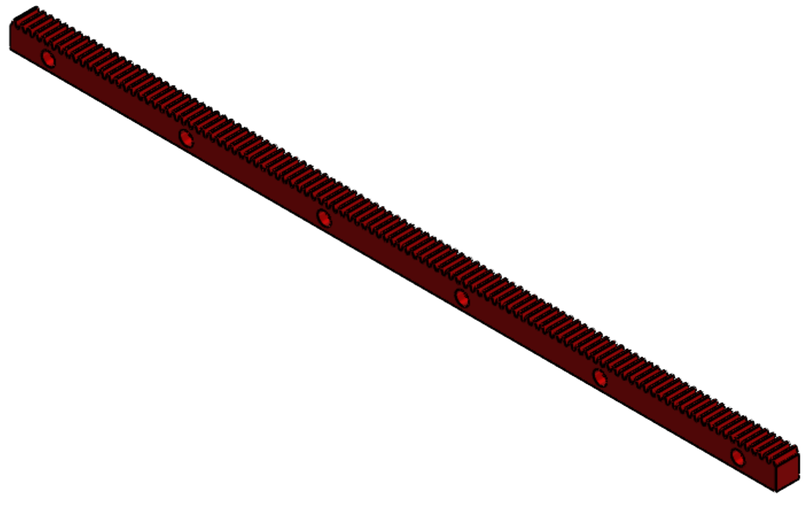

NOTE :

Name : Rack
Qty : 03 No's.

SPECIAL INSTRUCTION'S :

TITLE - SWIMMING POOL ENCLOSER

DWG NO - NTPL-294-PM-001-00-00-00

NIHVA Technologies Pvt. Ltd.

NIHVA TECHNOLOGIES PVT.LTD.PUNE
Website - www.nihva.com

	NAME	SIGNATURE	DATE
DRAWN	V.W.		25-08-2025
CHK'D	B.S.		29-08-2025
APPV'D	V.T.		30-08-2025

PRODUCT - SWIMMING POOL DECK

PROJECT NO - NTPL-294-PM | REVISION - 00

SITE LOCATION - PUNE | WEIGHT -

MATRIAL - | QTY - 1

If any queries contact - Design@nihva.com

PROJECTION METHOD:


SCALE :


ALL DIMENSION ARE IN mm | A2


DRAWING

REV DESCRIPTION	DATE	REV NO
	25-08-2025	REV 00
1.		

ITEM NO.	PART NUMBER	DESCRIPTION	QTY.
1	RACK SUPPORT PLATE	SIZE140.07X70X3 MM THK	08

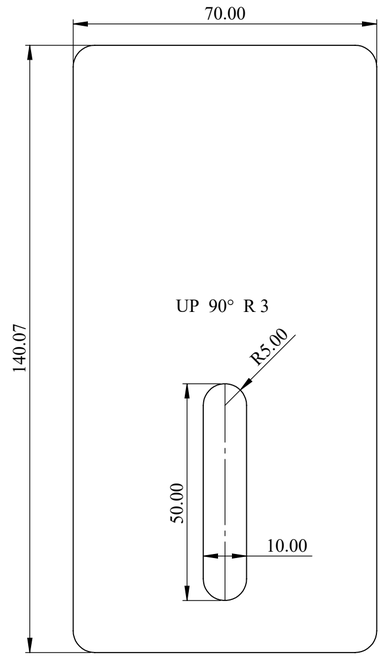

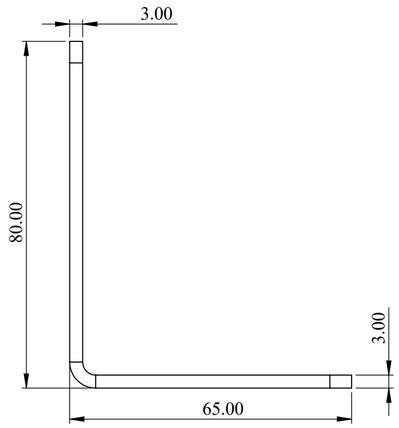

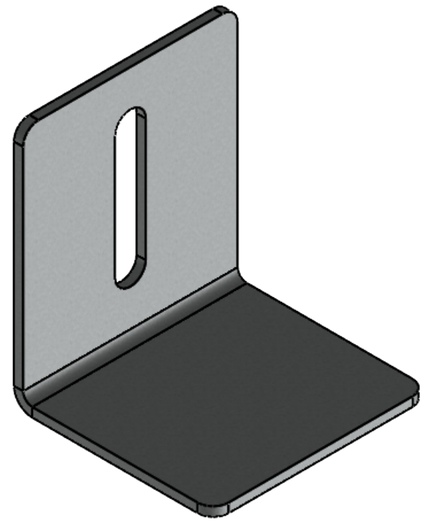

NOTE :

Name : Rack Support Plate
Size : 140.07X70X3 MM
Mtl : SS
Thk :3MM
Qty : 08 No's

SPECIAL INSTRUCTION'S :

TITLE - SWIMMING POOL ENCLOSER

DWG NO - NTPL-294-PM-001-00-00-00

NIHVA TECHNOLOGIES PVT.LTD.PUNE
Website - www.nihva.com

	NAME	SIGNATURE	DATE	PRODUCT - SWIMMING POOL DECK	
DRAWN	V.W.		25-08-2025	PROJECT NO - NTPL-294-PM	REVISION - 00
CHK'D	B.S.		29-08-2025	SITE LOCATION - PUNE	WEIGHT -
APPV'D	V.T.		30-08-2025	MATRIAL -	QTY - 1

If any queries contact - Design@nihva.com

ALL DIMENSION ARE IN mm | A2


PROJECTION METHOD:


SCALE :


DRAWING

REV DESCRIPTION	DATE	REV NO
	25-08-2025	REV 00
1.		

ITEM NO.	PART NUMBER	DESCRIPTION	QTY.
1	Anchor Bolt M10x100 MM L	STD	32

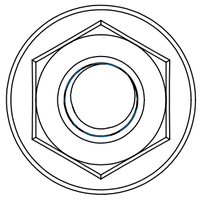

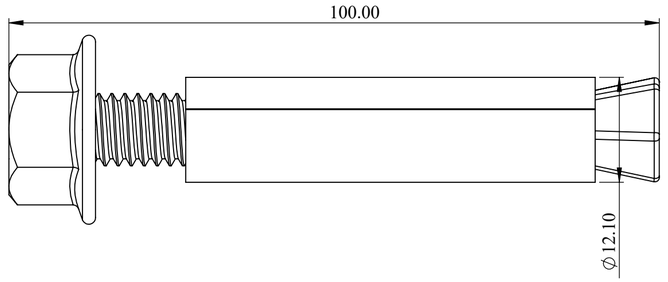

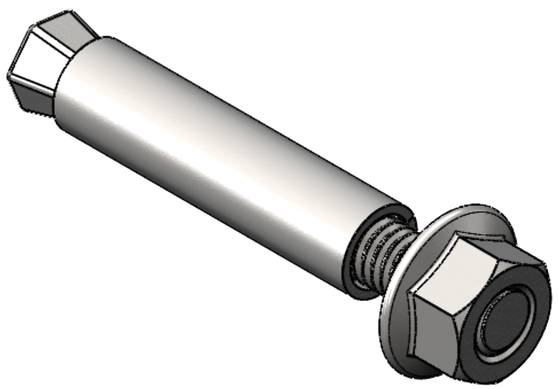

NOTE :

Name : Chemical Anchor Bolt
Size : M10X100 L
Mtl : SS
Qty : 32 No's.

SPECIAL INSTRUCTION'S :

TITLE - SWIMMING POOL ENCLOSER

DWG NO - NTPL-294-PM-001-00-00-00

NIHVA Technologies Pvt. Ltd.


NIHVA TECHNOLOGIES PVT.LTD.PUNE
Website - www.nihva.com

	NAME	SIGNATURE	DATE
DRAWN	V.W.		25-08-2025
CHK'D	B.S.		29-08-2025
APPV'D	V.T.		30-08-2025


PRODUCT - SWIMMING POOL DECK
PROJECT NO - NTPL-294-PM
REVISION - 00
SITE LOCATION - PUNE
WEIGHT -
MATRIAL -
QTY - 1
SCALE :
PROJECTION METHOD:
If any queries contact - Design@nihva.com
ALL DIMENSION ARE IN mm
A2


DRAWING

REV DESCRIPTION	DATE	REV NO
	25-08-2025	REV 00
1.		

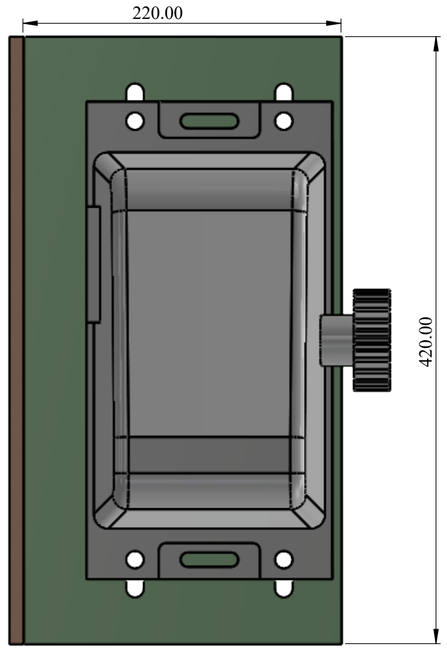

ITEM NO.	PART NUMBER	DESCRIPTION	QTY.
1	POST MOTOR BASE PLATE...		1
2	.Rev_02_MOTOR BRACKET.		1
3	.Rev_02_Nice RB1000.		1

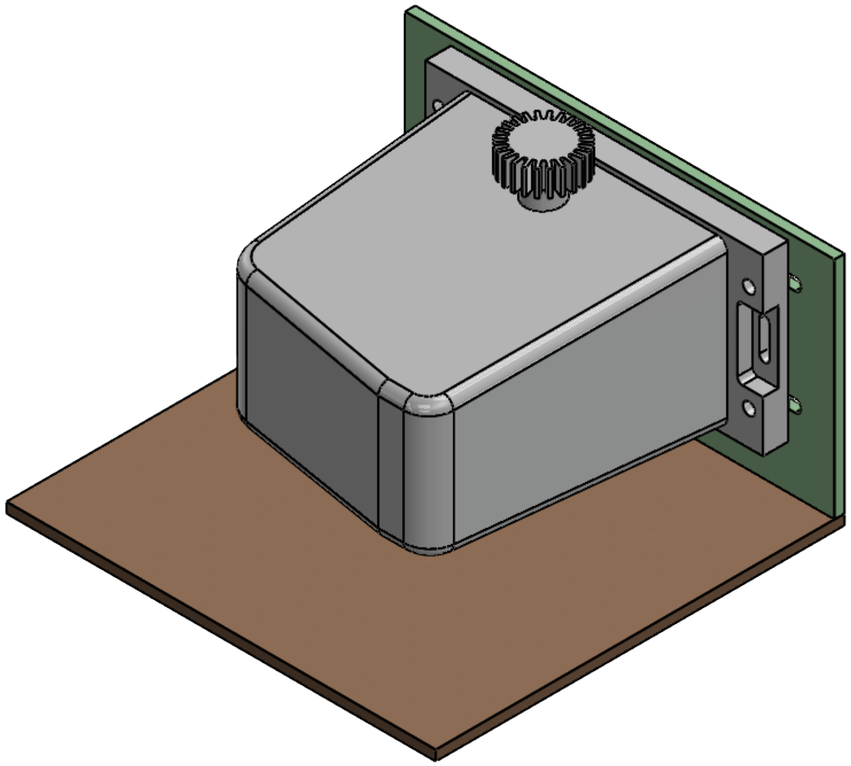

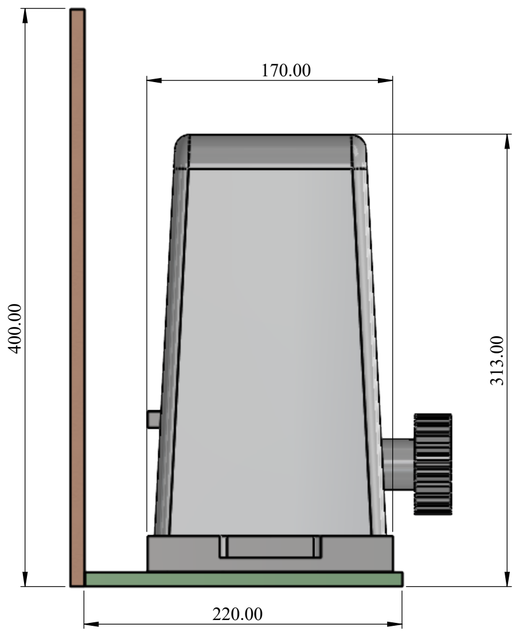

NOTE :

MOTOR MOUNTING ASM
MOTOR - NICE RB 1000
QTY - 1NOS

SPECIAL INSTRUCTION'S :

TITLE - SWIMMING POOL ENCLOSER

DWG NO - NTPL-294-PM-001-00-00-00

NIHVA Technologies Pvt. Ltd.

NIHVA TECHNOLOGIES PVT.LTD.PUNE
Website - www.nihva.com

	NAME	SIGNATURE	DATE
DRAWN	V.W.		25-08-2025
CHK'D	B.S.		29-08-2025
APPV'D	V.T.		30-08-2025


PRODUCT - SWIMMING POOL DECK
PROJECT NO - NTPL-294-PM | REVISION - 00
SITE LOCATION - PUNE | WEIGHT -
MATRIAL - | QTY - 1

If any queries contact - Design@nihva.com
ALL DIMENSION ARE IN mm | A2
PROJECTION METHOD:
SCALE :
SHEET 16 OF 19

DRAWING

ITEM NO.	PART NUMBER	DESCRIPTION	QTY.
1	.Rev_02_MTR MTG PLT.	380X220X16	1

REV DESCRIPTION	DATE	REV NO
	25-08-2025	REV 00
1.		

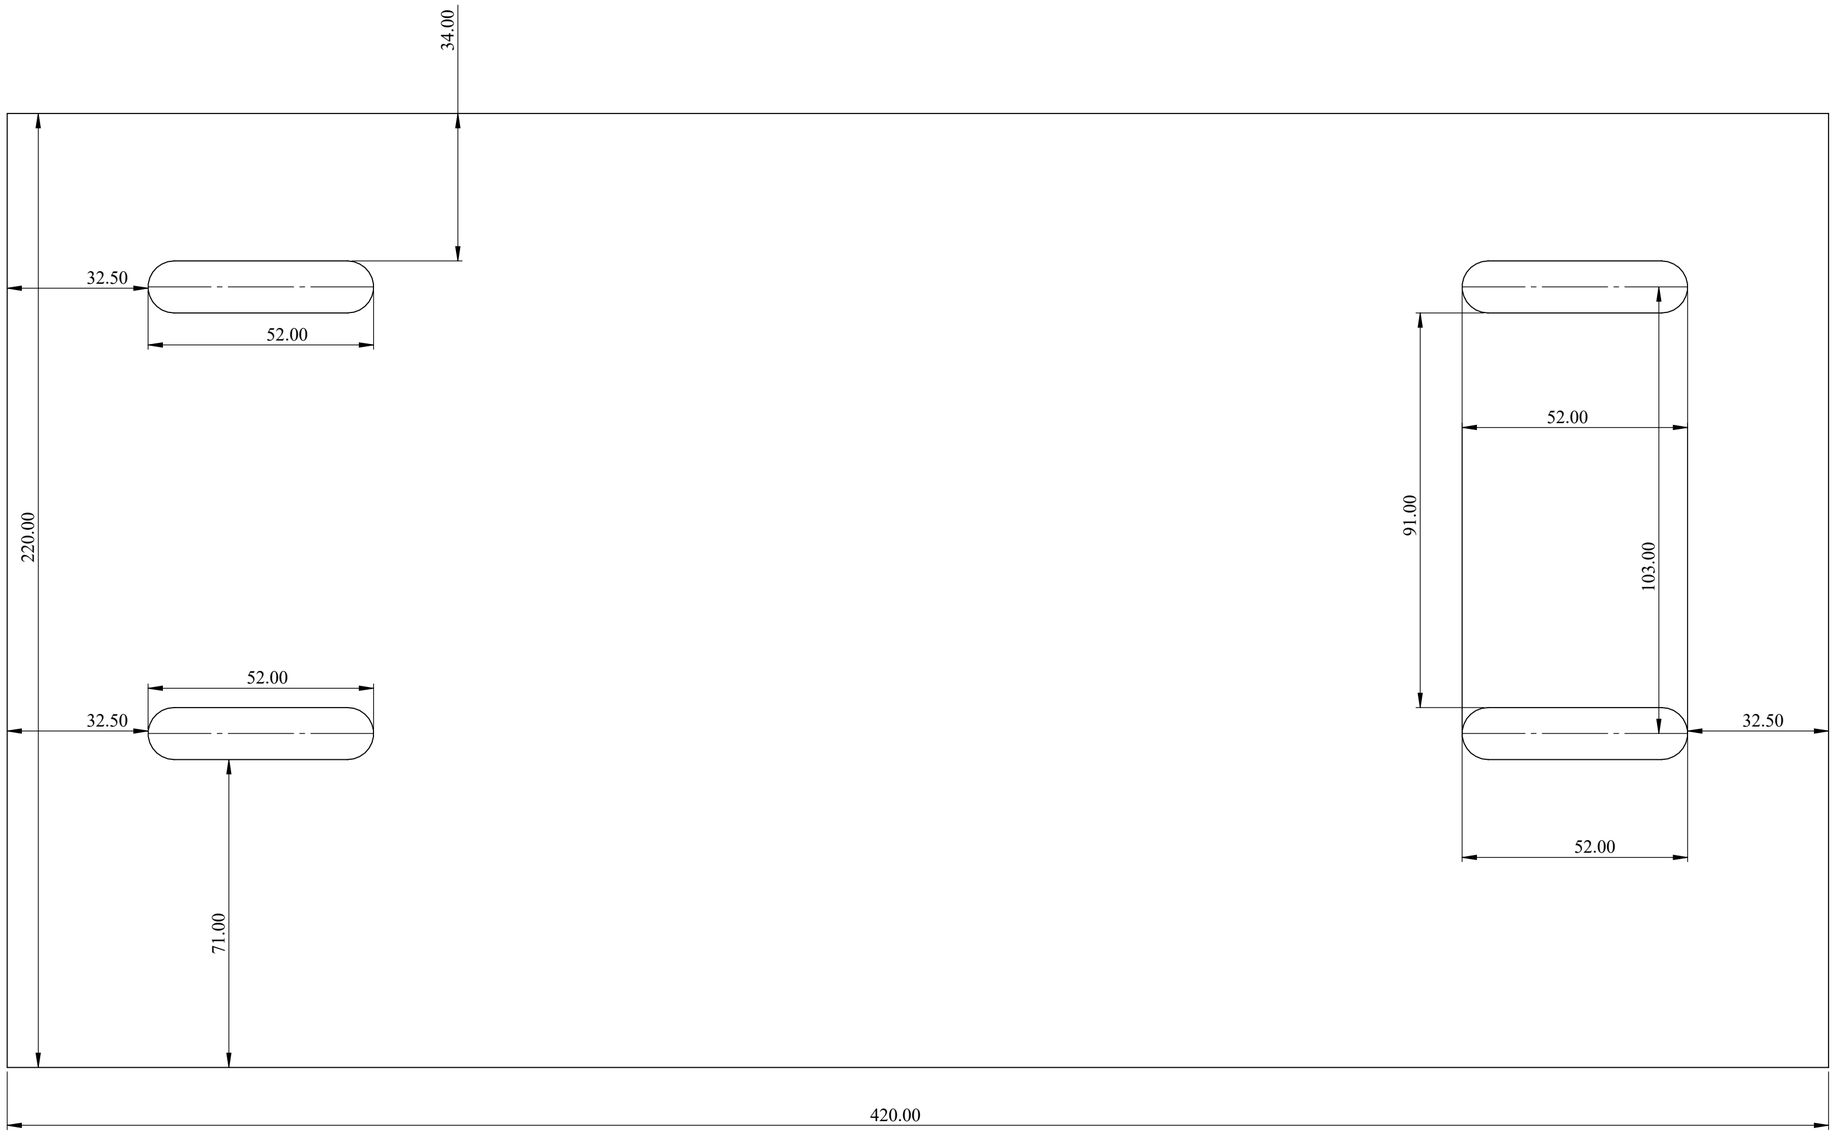

NOTE :

MOTOR MOUNTING PLATE 1
MTL - MS
THK - 10 MM
QTY - 1

SPECIAL INSTRUCTION'S :

TITLE - SWIMMING POOL ENCLOSER

DWG NO - NTPL-294-PM-001-00-00-00

NIHVA Technologies Pvt. Ltd.

NIHVA TECHNOLOGIES PVT.LTD.PUNE
Website - www.nihva.com


	NAME	SIGNATURE	DATE
DRAWN	V.W.		25-08-2025
CHK'D	B.S.		29-08-2025
APPV'D	V.T.		30-08-2025


PRODUCT - SWIMMING POOL DECK
PROJECT NO - NTPL-294-PM | REVISION - 00
SITE LOCATION - PUNE | WEIGHT -
MATRIAL - | QTY - 1
If any queries contact - Design@nihva.com | PROJECTION METHOD: | SCALE :
ALL DIMENSION ARE IN mm | A2 | SHEET 17 OF 19


DRAWING

REV DESCRIPTION	DATE	REV NO
	25-08-2025	REV 00
1.		

ITEM NO.	PART NUMBER	DESCRIPTION	QTY.
1	POST MOTOR BASE PLATE...		1

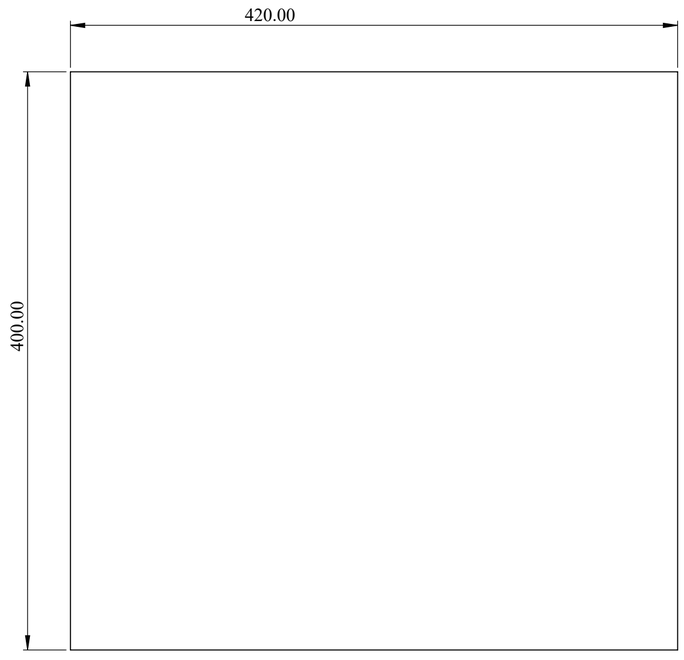

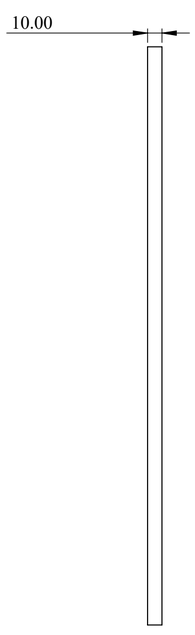

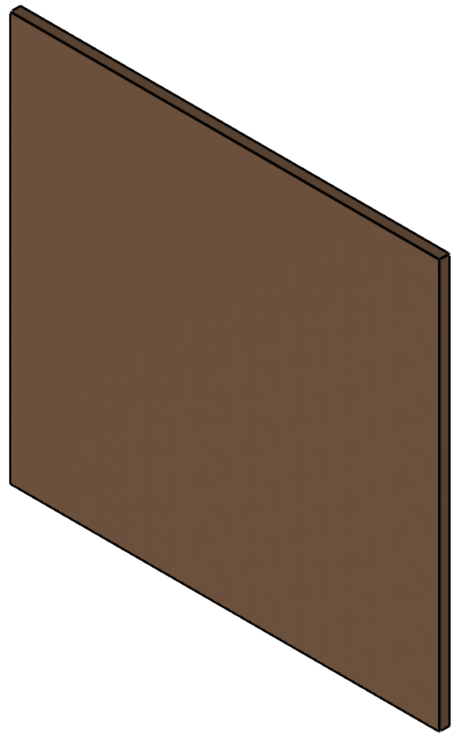

NOTE :

MOTOR MOUNTING PLATE 2
MTL - MS
QTY - 1 NOS
THK -10 MM

SPECIAL INSTRUCTION'S :

TITLE - SWIMMING POOL ENCLOSER

DWG NO - NTPL-294-PM-001-00-00-00

NIHVA TECHNOLOGIES PVT.LTD.PUNE
Website - www.nihva.com


	NAME	SIGNATURE	DATE
DRAWN	V.W.		25-08-2025
CHK'D	B.S.		29-08-2025
APPV'D	V.T.		30-08-2025


PRODUCT - SWIMMING POOL DECK
PROJECT NO - NTPL-294-PM
REVISION - 00
SITE LOCATION - PUNE
WEIGHT -
MATRIAL -
QTY - 1
If any queries contact - Design@nihva.com
PROJECTION METHOD:
SCALE :
ALL DIMENSION ARE IN mm
A2

DRAWING

REV DESCRIPTION	DATE	REV NO
	25-08-2025	REV 00
1.		

ITEM NO.	PART NUMBER	DESCRIPTION	QTY.
1	Link Plate		1
2	Rivet Link Plate		1
3	Clamp		1
4	Screw		1
5	Wheel		1
6	Connection Pin		1

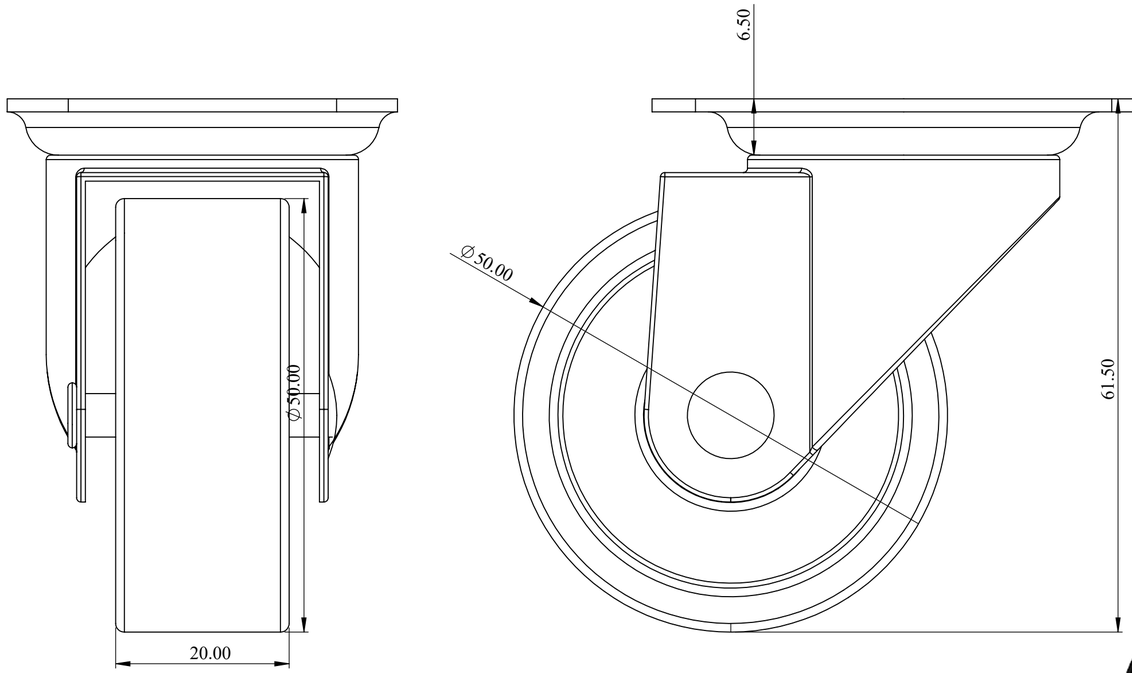

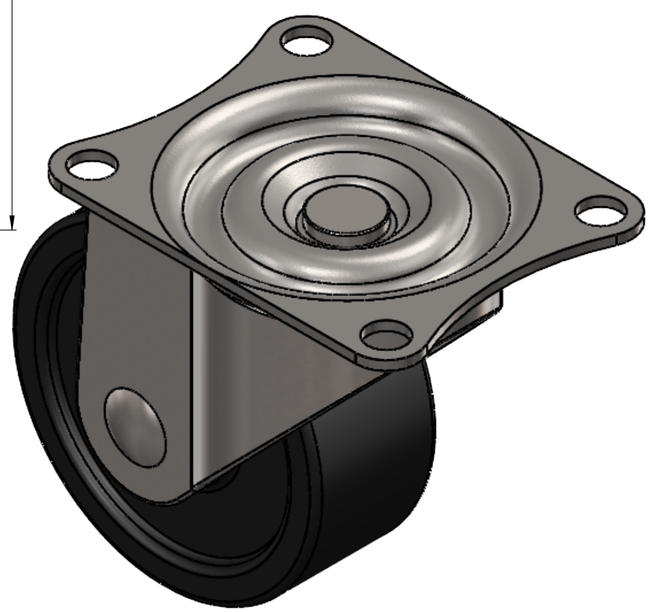

NOTE :

Name : Caster Wheel
Qty : 04 No's

SPECIAL INSTRUCTION'S :

TITLE - SWIMMING POOL ENCLOSER

DWG NO - NTPL-294-PM-001-00-00-00

NIHVA Technologies Pvt. Ltd.

NIHVA TECHNOLOGIES PVT.LTD.PUNE
Website - www.nihva.com

	NAME	SIGNATURE	DATE
DRAWN	V.W.		25-08-2025
CHK'D	B.S.		29-08-2025
APPV'D	V.T.		30-08-2025

PRODUCT - SWIMMING POOL DECK
PROJECT NO - NTPL-294-PM | REVISION - 00
SITE LOCATION - PUNE | WEIGHT -
MATRIAL - | QTY - 1
If any queries contact - Design@nihva.com | PROJECTION METHOD: | SCALE :
ALL DIMENSION ARE IN mm | A2 | SHEET 19 OF 19