This drawing is the property of L&T Construction ,B&F-EDRC and must not be passed on to any person or body not authorised by us to receive it nor be copied or otherwise made use either in full or in part by such person or body without our prior permission in writing.

##
10000
5000 (SLIDING GATE)
5000 (SLIDING GATE)
6800
3400 (SLIDING GATE)
3400 (SLIDING GATE)
LAWN
PLANTER BOX
MS GUIDE CHANNEL
MS GUIDE PLATE
SPACE FOR POT PLANTS
ENTRANCE PORTAL
+34.15 FRL
+34.00 FRL
+34.20 FPL
INSIDE
OUTSIDE
RC COLUMN AS PER STRUCTURAL DWG
3800
1200 (OPENABLE GATE)
50X50 MS HOLLOW SECTION
MS HOLD FAST FOR OPENABLE GATE
150MM THK BLOCK WALL (HEIGHT MATCH WITH COMPOUND WALL)
RC CURB BELOW SLAB
RC SLAB @+34.65 LVL
ENTRANCE PORTAL BEAM ABOVE
RC COLUMN AS PR STRUCTURE DWG
150 EQ
50 (TYP)
5535
675
16535
18185
2595
EQ

① PLAN OF ENTRY / EXIT GATE -1
1:25

RC COLUMN AS PER STRUCTURAL DWG
03
04
10000
5000 (SLIDING GATE)
5000 (SLIDING GATE)
6800
3400 (SLIDING GATE)
3400 (SLIDING GATE)
150MM WIDE RC BAND
EQ
+36.15 LVL
MS GUIDE PLATE
+34.15 FRL
+34.00 FRL
2000
50X50 MS HOLLOW SECTION
3800
1200 (OPENABLE GATE)
MS HOLD FAST FOR OPENABLE GATE
1500
900
650
20MM THK BLOCK WALL WITH TEXTURE PAINT - 1
PLASTER GROOVES
MS WHEEL
300 (TYP)
+34.20 FPL
150MM WIDE RC BAND
20MM THK BLOCK WALL WITH TEXTURE PAINT - 2

② ELEVATION OF ENTRY / EXIT GATE -1
1:25

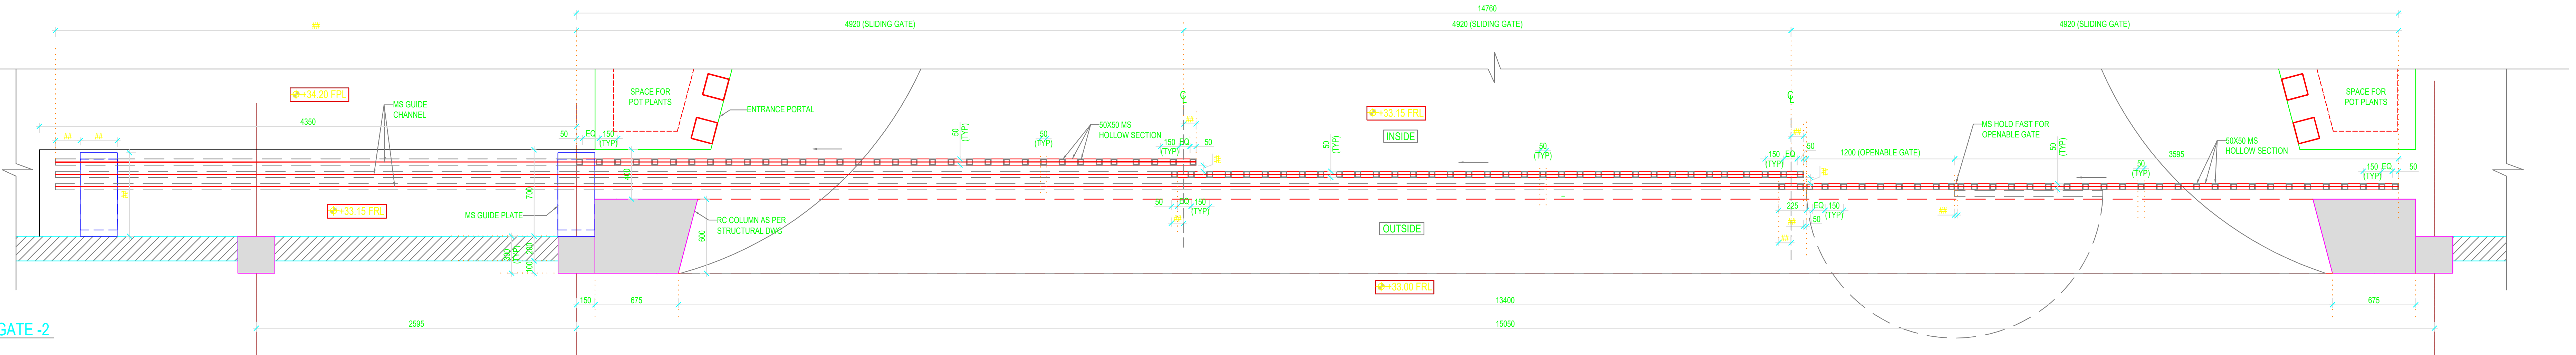

14760
4920 (SLIDING GATE)
4920 (SLIDING GATE)
4920 (SLIDING GATE)
+34.20 FPL
MS GUIDE CHANNEL
4350
SPACE FOR POT PLANTS
ENTRANCE PORTAL
50X50 MS HOLLOW SECTION
INSIDE
OUTSIDE
MS GUIDE PLATE
RC COLUMN AS PER STRUCTURAL DWG
1200 (OPENABLE GATE)
MS HOLD FAST FOR OPENABLE GATE
3595
675
13400
15050
2695

③ PLAN OF ENTRY / EXIT GATE -2
1:25

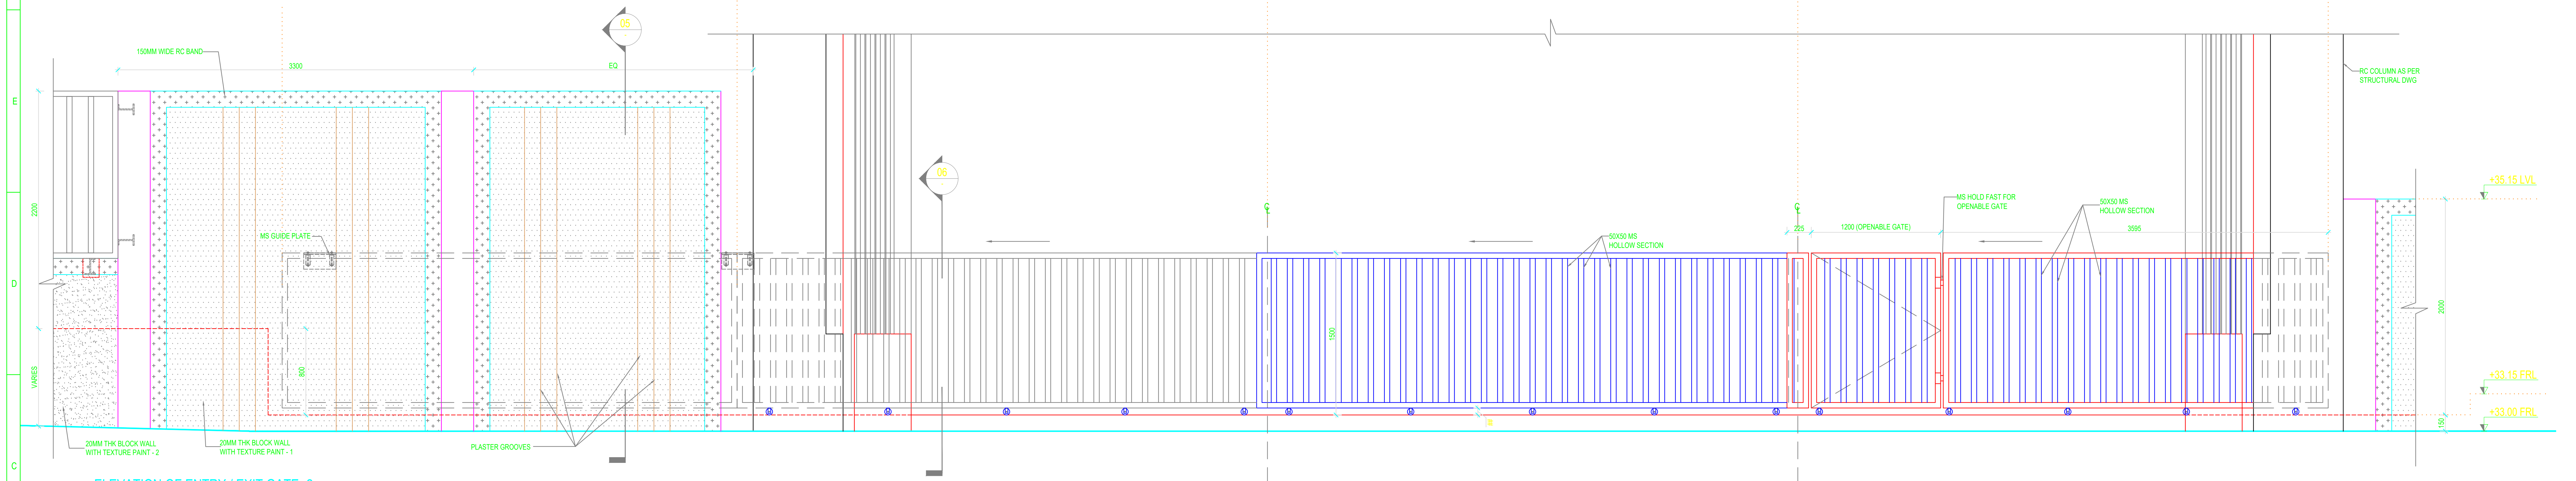

150MM WIDE RC BAND
3300
EQ
05
06
MS GUIDE PLATE
2000
VARIES
800
RC COLUMN AS PER STRUCTURAL DWG
50X50 MS HOLLOW SECTION
MS HOLD FAST FOR OPENABLE GATE
1200 (OPENABLE GATE)
3595
1500
+35.15 LVL
+33.15 FRL
+33.00 FRL
20MM THK BLOCK WALL WITH TEXTURE PAINT - 2
20MM THK BLOCK WALL WITH TEXTURE PAINT - 1
PLASTER GROOVES

④ ELEVATION OF ENTRY / EXIT GATE -2
1:25

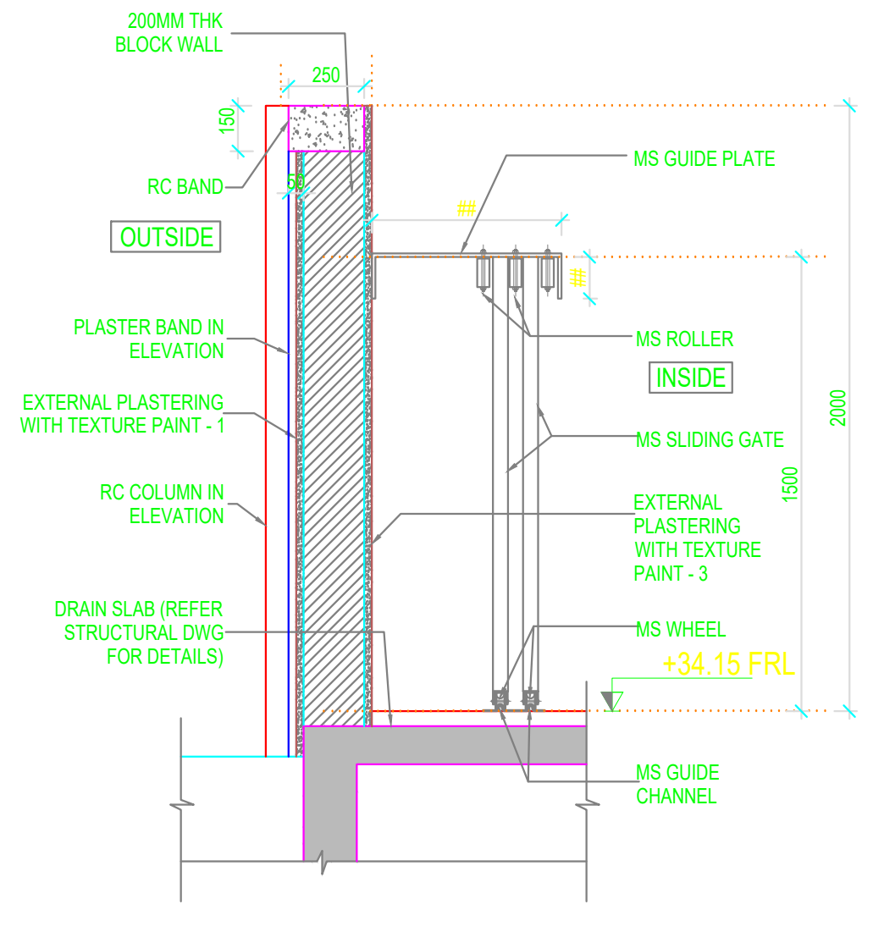

200MM THK BLOCK WALL
250
150
RC BAND
OUTSIDE
PLASTER BAND IN ELEVATION
EXTERNAL PLASTERING WITH TEXTURE PAINT - 1
RC COLUMN IN ELEVATION
DRAIN SLAB (REFER STRUCTURAL DWG FOR DETAILS)
MS GUIDE PLATE
MS ROLLER
INSIDE
MS SLIDING GATE
EXTERNAL PLASTERING WITH TEXTURE PAINT - 3
MS WHEEL
+34.15 FRL
MS GUIDE CHANNEL
2000
1500

⑤ SECTION -3
1:25

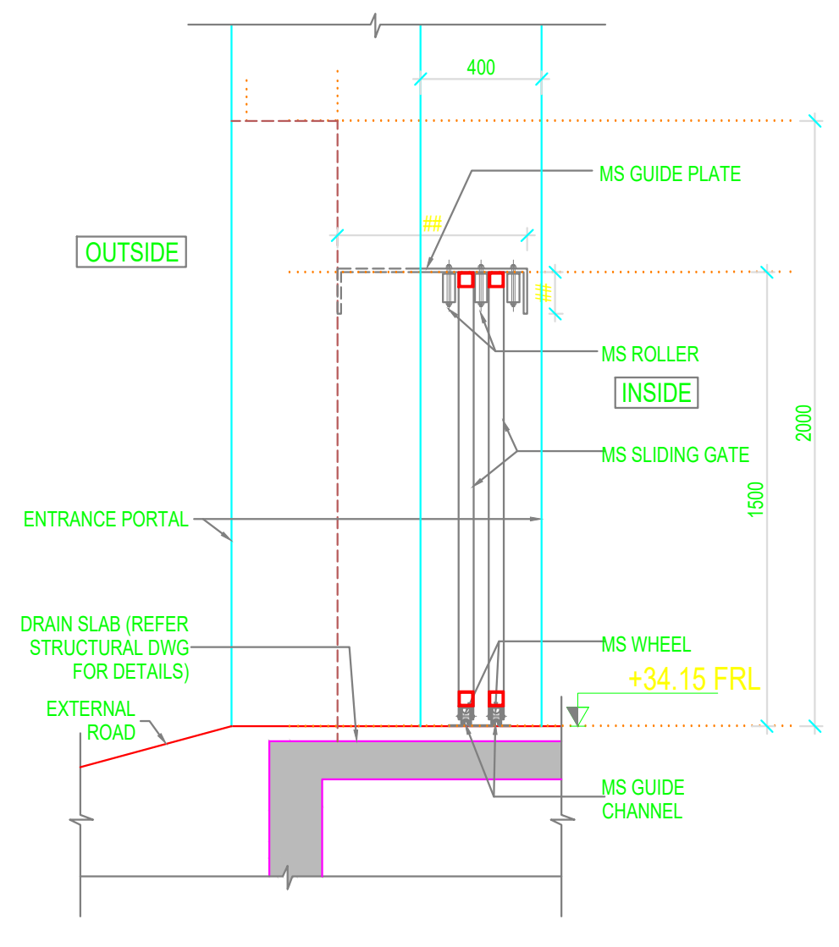

400
OUTSIDE
ENTRANCE PORTAL
DRAIN SLAB (REFER STRUCTURAL DWG FOR DETAILS)
EXTERNAL ROAD
MS GUIDE PLATE
MS ROLLER
INSIDE
MS SLIDING GATE
MS WHEEL
+34.15 FRL
MS GUIDE CHANNEL
2000
1500

⑥ SECTION -4
1:25

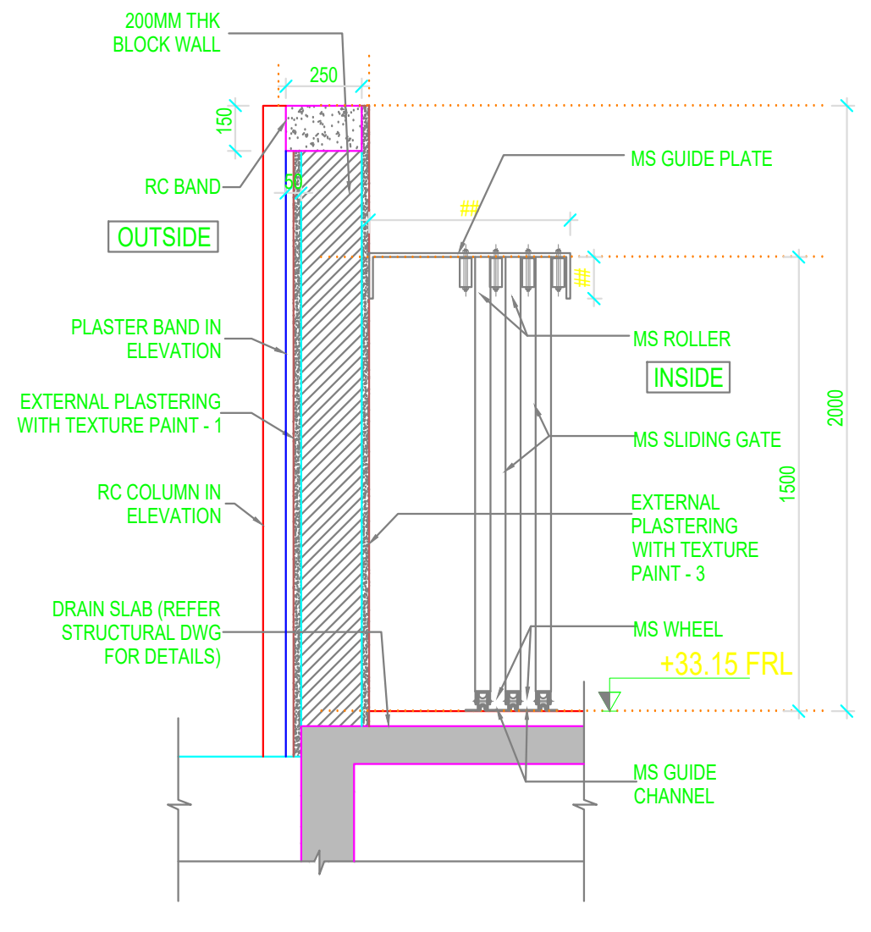

200MM THK BLOCK WALL
250
150
RC BAND
OUTSIDE
PLASTER BAND IN ELEVATION
EXTERNAL PLASTERING WITH TEXTURE PAINT - 1
RC COLUMN IN ELEVATION
DRAIN SLAB (REFER STRUCTURAL DWG FOR DETAILS)
MS GUIDE PLATE
MS ROLLER
INSIDE
MS SLIDING GATE
EXTERNAL PLASTERING WITH TEXTURE PAINT - 3
MS WHEEL
+33.15 FRL
MS GUIDE CHANNEL
2000
1500

⑦ SECTION -5
1:25

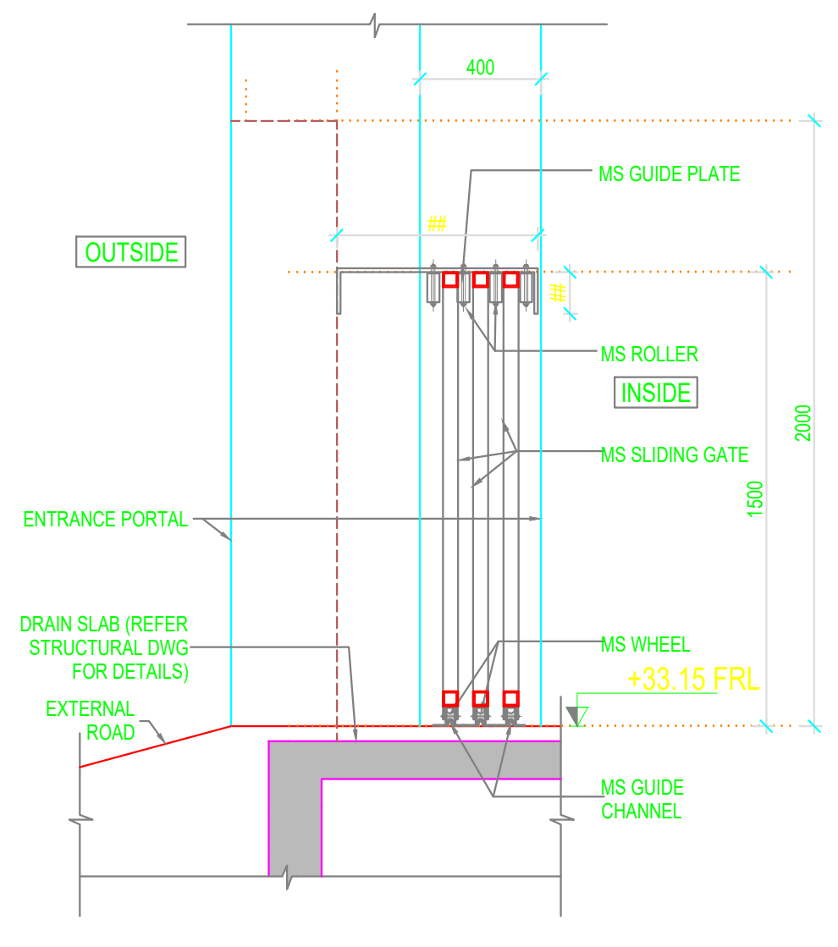

400
OUTSIDE
ENTRANCE PORTAL
DRAIN SLAB (REFER STRUCTURAL DWG FOR DETAILS)
EXTERNAL ROAD
MS GUIDE PLATE
MS ROLLER
INSIDE
MS SLIDING GATE
MS WHEEL
+33.15 FRL
MS GUIDE CHANNEL
2000
1500

⑧ SECTION -6
1:25

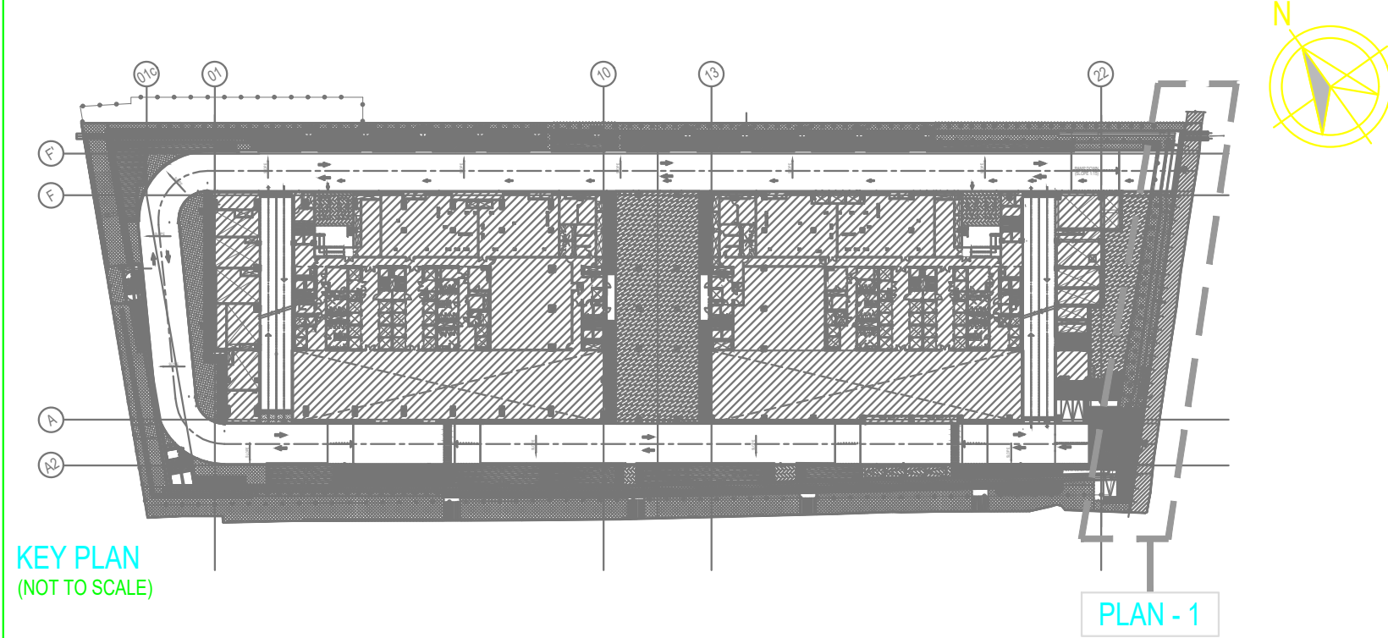

KEY PLAN
(NOT TO SCALE)

WALL INDEX

S.NO	PATTERN	DESCRIPTION
1	▨	200mm THK BLOCK WALL
2	▨ / ▨	R.C.C.
3	▨	DRAIN COVER SLAB
4	▨	LAWN / PLANTER BOX

ABBREVIATIONS

FRL : FINISHED ROAD LEVEL
FPL : FINISHED PAVEMENT LEVEL
FFL : FINISHED FLOOR LEVEL
TSL : TOP OF SOIL LEVEL
TOK : TOP OF KERB LEVEL
TOD : TOP OF DRAIN LEVEL
TOC : TOP OF CONCRETE
LVL : LEVEL

LEGEND

PATTERN	DESCRIPTION
▨	RC / PLASTER BAND
▨	TEXTURE PAINT - TYPE-1
▨	TEXTURE PAINT - TYPE-2

COMPOUND WALL MEASUREMENTS AND LEVELS SHALL BE CONFIRMED AS PER SITE CONDITION BEFORE EXECUTION

INDICATES DIMENSIONS AS PER VENDOR REQUIREMENT

PRIOR TO INSTALLATION OF SLIDING / WICKET GATE VENDOR TO SUBMIT SHOP DRAWING FOR THE SAME AND OBTAIN APPROVAL FROM EDRC.

NOTES

01. ALL DIMENSIONS ARE IN MILLIMETER & LEVELS IN METER.
02. THE FINISHED GROUND FLOOR LEVEL HAS BEEN CONSIDERED AS ±0.000 LVL CORRESPONDS TO +34.20 MSL AT SITE
03. FOR SITE SETTING OUT PLAN REFER DWG NO.O23023-A-OB-00-WD-0001
04. FOR MASTER PLAN REFER DWG NO.O23023-A-OB-00-WD-0002
05.THIS DRAWING SHALL BE READ IN CONJUNCTION WITH ALL RELEVANT ARCHITECTURAL STRUCTURAL AND OTHER RELATED SERVICE DRAWINGS
06.ALL DIMENSIONS SHALL BE VERIFIED ON SITE PRIOR TO START OF WORK ANY DISCREPANCY SHALL BE BROUGHT TO THE NOTICE OF THE EDRC ARCHITECT.
07. THIS DRAWING IS TO BE READ AND NOT TO BE SCALED.

REV.NO.	DESCRIPTION	DESIGNED		DRAWN		CHECKED		APPROVED	
0	ISSUED FOR CONSTRUCTION	BSC	27.02.2025	PJ	28.02.2025	ECM	01.03.2025	JVP	03.03.2025

REVISIONS

CHECKED BY	SIGN	DATE	CHECKED BY	SIGN	DATE	CHECKED BY	SIGN	DATE
ARCHITECTURE			HVAC			GIS		
CIVIL & STRUCTURAL			FPS			GEOTECH.		
ELECTRICAL			PIPING					
ELV SYSTEM			PHE					

CLIENT : L&T Realty L&T Realty

O23023,O23023-A-O

L&T Construction
Buildings & Factories

PROJECT: L&T Commercial Tower (LTCT) at Powai, Mumbai

PRINCIPAL CONSULTANT : Engineering Design and Research Center (EDRC), L&T Construction - Buildings & Factories

MEP CONSULTANT : M/s. CHETTIAR CONSULTING ENGINEERS.
SHRI SAI CORPORATE PARK, 304, THIRD FLOOR, NEW LINK ROAD
MAHAKALI TEMPLE ROAD, NEAR VASANT GALAXY &
LAXMI NAGAR, GOREGAON (WEST), MUMBAI-400 062.

SUPPLIER/ CONTRACTOR : Larsen & Toubro Limited, Construction, Buildings & Factories

JOB No : O23023

	NAME	SIGN	DATE
DSGN	BSC		27.02.2025
DRWN	PJ		28.02.2025
CHKD	ECM		01.03.2025
APPD	JVP		03.03.2025

TITLE:
OFFICE BUILDING
ENTRY / EXIT DETAILS

SECTION/ ELEVATION MARKING
DRAWING NUMBER

SCALE
AS INDICATED

DRAWING No. O23023-A-OB-00-WD-0000

PROJECTION
FIRST ANGLE

SIZE	REV
A0	0

RELEASED FOR ☐ PRELIMINARY ☐ TENDER ☐ INFORMATION ☐ APPROVAL ☑ CONSTRUCTION