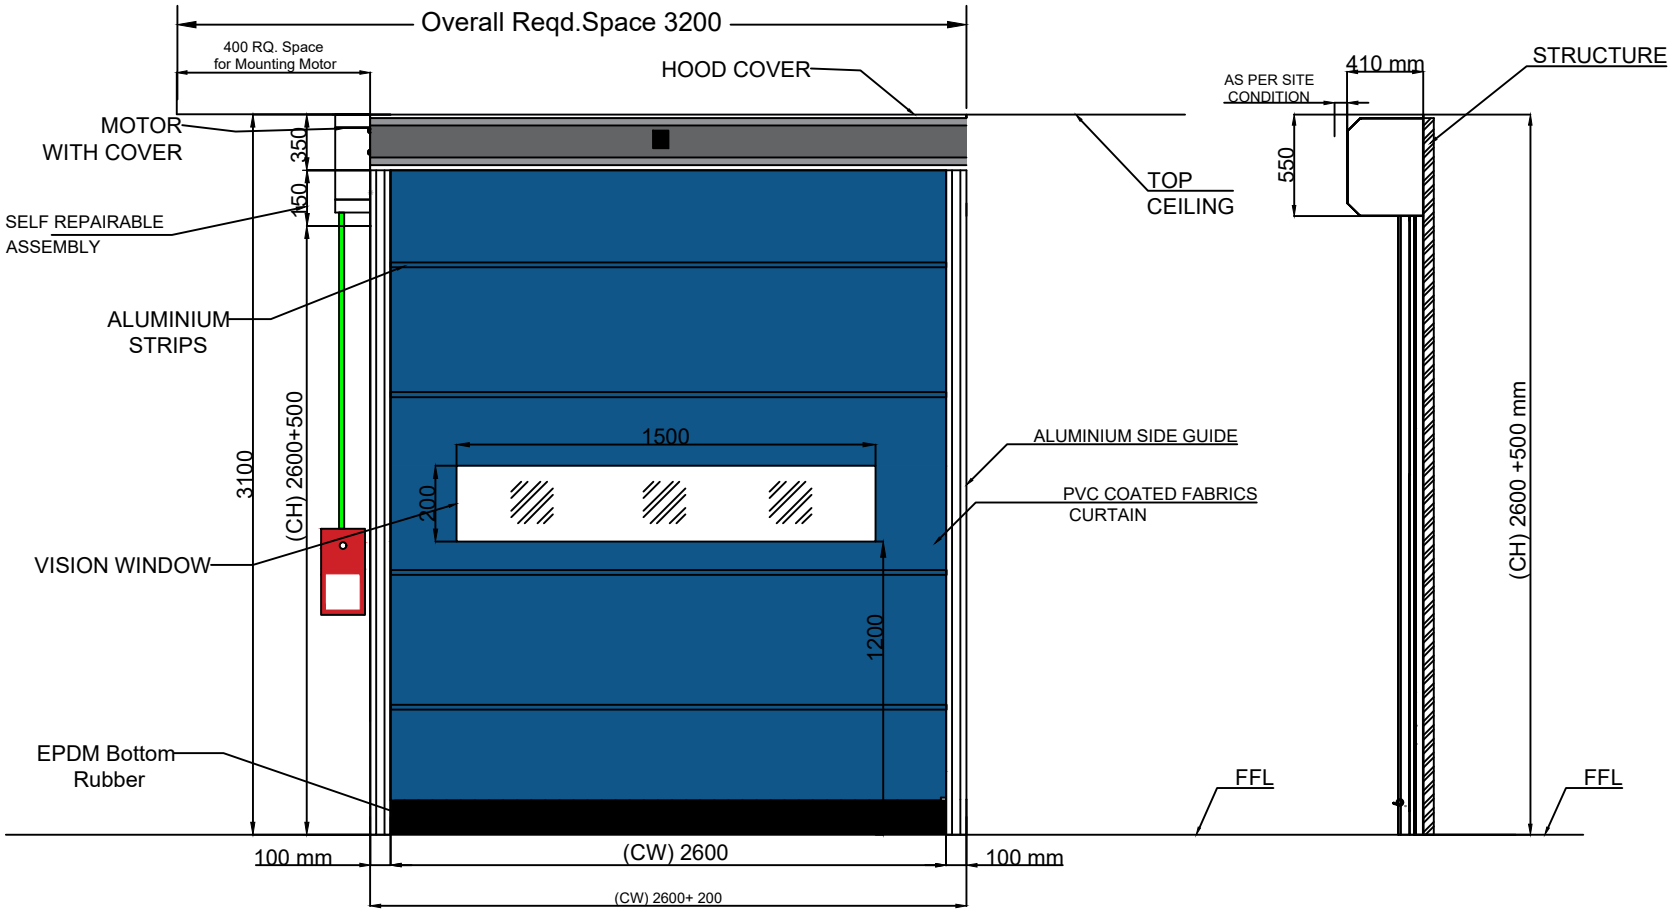


TECHNICAL SPECIFICATION :

SR.	SPECIFICATIONS	DETAILS
1	Use	Internal Door
2	Mounting	On Structure: Inside
3	Control Panel	As per STD
4	Motor	Nihva make
5	Door Travel Speed	Opening: 0.3m/Sec & Closing: 0.8m/Sec
6	Safety Device	Safety Photocell Pair & Safety Edges

Note:-
1. All Dimensions are in mm
2.This drawing is solely meant to be understood.
3. RAL code confirm by client

Sr	Clear Width (CW)	Clear Height (CH)	QTY
1	**2600**	**2600**	01

This drawing & design is the property of NIHVA TECHNOLOGIES. Not to be sold or copied to any other concern.

TITLE: HIGH SPEED DOOR

NIHVA TECHNOLOGIES PVT. LTD. PUNE
Tel : 020 66304033
Email:- info@nihva.com
Website:- www.nihva.com

	NAME	SIGN	DATE
DRAWN	S.J		04.01.2025
CHECK	S.J		04.01.2025
APPRD.	V.T		04.01.2025

CLIENT - bilcare
PROJECT - HIGH SPEED DOOR
FORMAT NO - NIHVA-DD-F-03
If any queries contact : projectsupport@nihva.com
DWG. NO. : NIHVA/24-25/SM/241001 REV- R04
ALL DIMENSION ARE IN mm
SCALE: NTS WT: SHEET: