

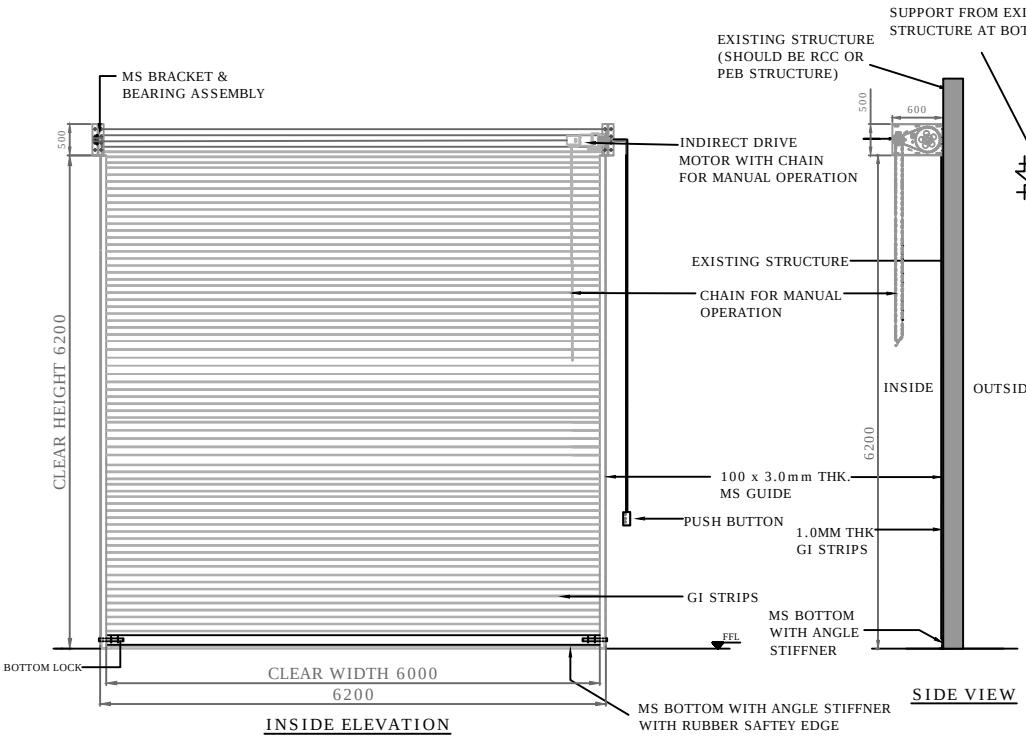


INSIDE ELEVATION


SIDE VIEW

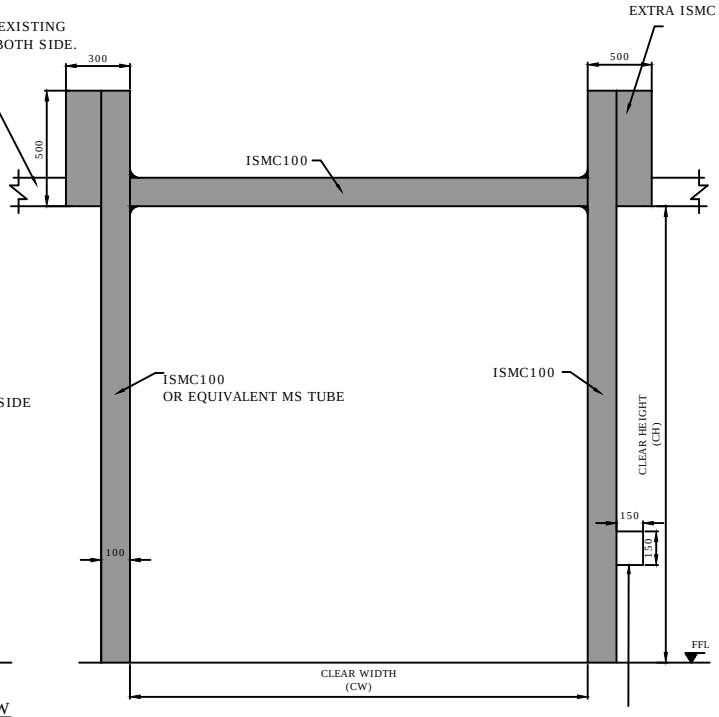


MS STRUCTURE

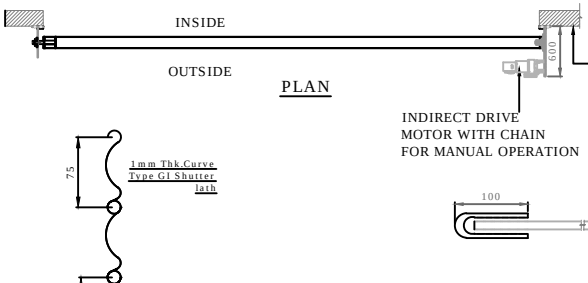

PLAN

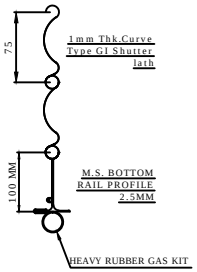

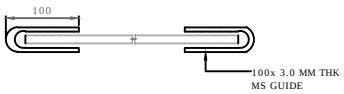

CLEAR WIDTH (CW)	CLEAR HEIGHT (CH)	QUANTITY
6000	6200	1

DIMENSION :

CLEAR WIDTH	CLEAR HEIGHT	QUANTITY
6000 mm	6200 mm	1 NOS.

MATERIAL :

THICKNESS :

NOTE: REQUIRED STRUCTURE FOR DOOR SHOULD BE IN CLIENT SCOPE.

ONE COAT OF RED OXIDE PRIMER SHALL BE GIVEN TO THE SHUTTER.

NIHVA TECHNOLOGIES PVT. LTD.
NIHVA TECHNOLOGY PVT. LTD. PUNE
Email:- info@nihva.com
Website:- www.nihva.com

TITLE:

MOTORIZED ROLLING SHUTTER

CLIENT'S APPROVAL :

CLIENT -

PROJECT -

SITE LOCATION -

DWG. NO. : NIHVA/16-17/VDR/004

SCALE: NTS	WT:	SHEET:1 OF 1

DRAWN BY: OMKAR	DATE: 26-10-2016
CHECK : ANIL	DATE: 26-10-2016

If any queries contact : projects@nihva.com

NOTE: ALL DIMENSION ARE IN mm

THIS DRAWING & DESIGNING IS THE PROPERTY OF NIHVA TECHNOLOGIES. NOT BE SOLD OR COPY TO ANY OTHER CONCERN.