




SIDE VIEW

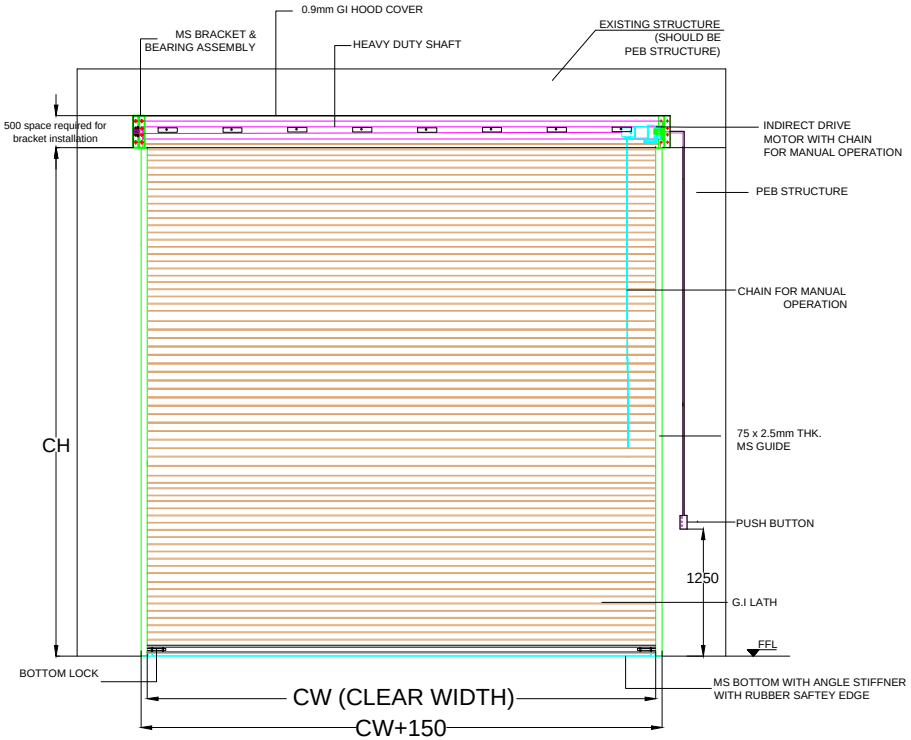


ELEVATION

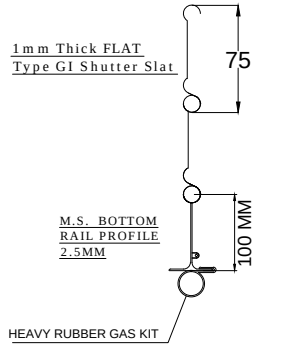

M.S. BOTTOM RAIL PROFILE 2.5MM

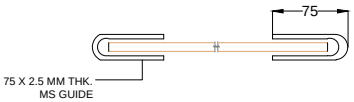

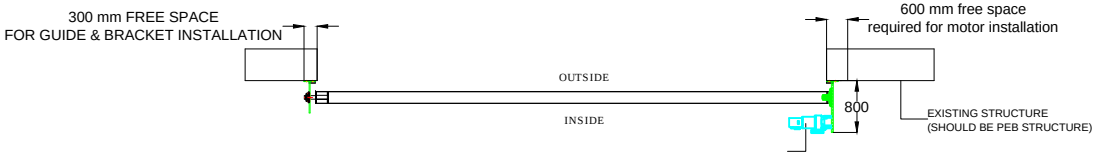

PLAN

NOTE:
1 REQUIRED STRUCTURE FOR SHUTTER SHALL BE IN CLIENT SCOPE.
2.ONE COAT OF RED OXIDE PRIMER WILL BE GIVEN TO THE SHUTTER.
3.SINGLE PHASE. 3CORE 1.2SQ. CABLE REQUIRED AT SITE (CLIENT'S SCOPE)

S.NO	RAL CODE	COLOR	APPROVED
01	RAL 9002	WHITE GRAY	
02	RAL 5010	GENTIAN BLUE	
03	RAL 7035	LIGHT GRAY	
04	RAL 9016	TRAFFIC WHITE	
05	RAL 3001	SIGNAL RED	

REV NO	DRAWN	DATE	REMARK
R01	P.A	28.12.18	2. RAL CODE TABLE ADD. 1. SLAT PROFILE CHANGE.

TOLERANCE - ±10mm

CLEAR WIDTH	CLEAR HEIGHT	QTY.
4000mm	5000mm	01NO
2500mm	3000mm	03NOS

This drawing & design is the property of NIHVA TECHNOLOGIES. Not to be sold or copied to any other concern.

TITLE
MOTORISED ROLLING SHUTTER

	NAME	SIGN	DATE
DRAWN	SURAJ		18-12-2018
CHECK	OMKAR		18-12-2018
APPRD.	PRADEEP		18-12-2018

If any queries contact : design@nihva.com

ALL DIMENSION ARE IN mm

NIHVA
NIHVA TECHNOLOGIES PVT. LTD.
Website:- www.nihva.com
NIHVA TECHNOLOGIES PVT. LTD. PUNE
Tel : 020 66304033
Email:- info@nihva.com

CLIENT -**SYNERGY PROPERTY DEVELOPMENT SERVICES PVT LTD**

PROJECT -

SITE LOCATION - CHAKAN

DWG. NO. : NIHVA/18-19/0212/R01 | REV- R01

SCALE: NTS | WT: | SHEET: 01 OF 01