

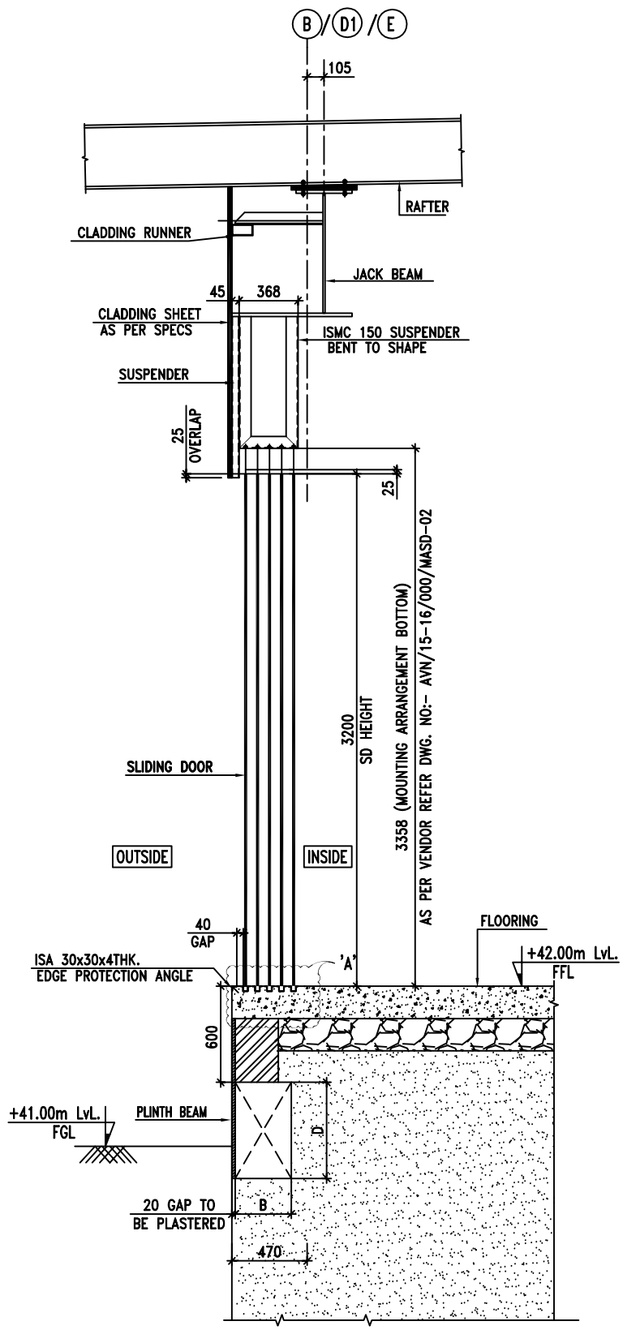



TYPICAL SLIDING DOOR CONNECTION DETAIL FOR 5 PANELS

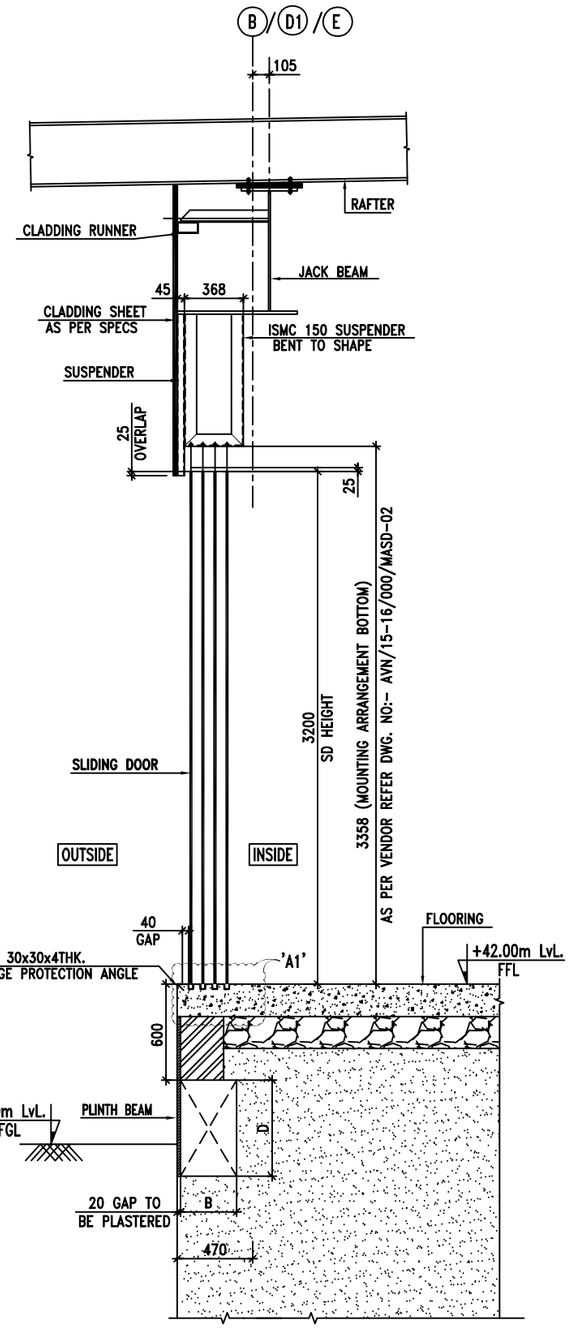


TYPICAL SLIDING DOOR CONNECTION DETAIL FOR 4 PANELS

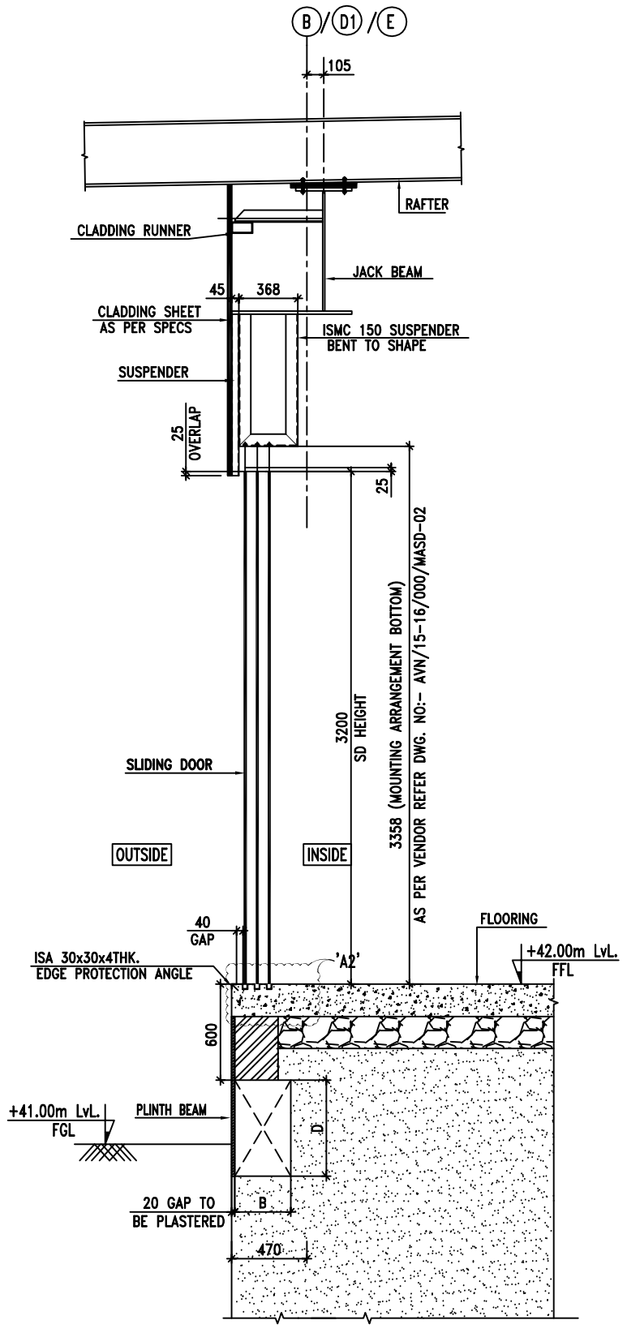


TYPICAL SLIDING DOOR CONNECTION DETAIL FOR 3 PANELS

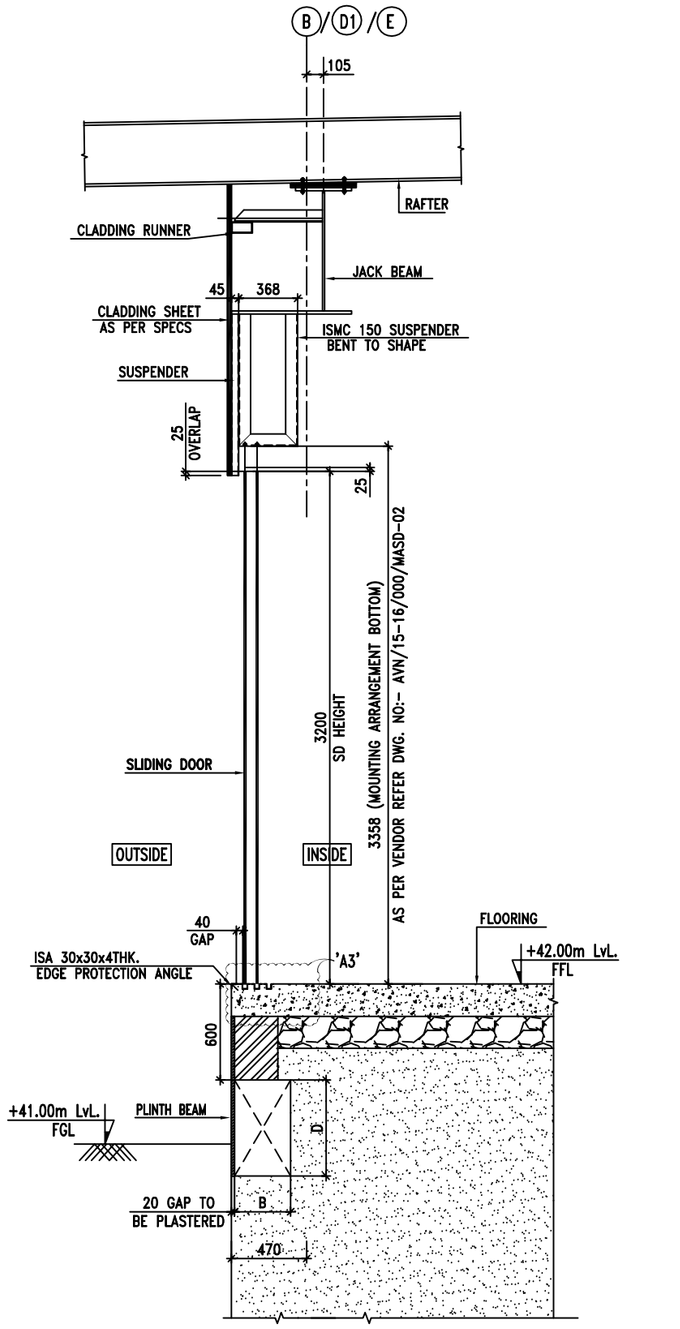


TYPICAL SLIDING DOOR CONNECTION DETAIL FOR 2 PANELS

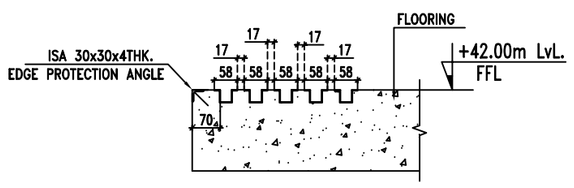


DETAIL–'A'

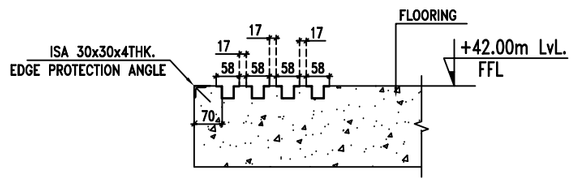

DETAIL–'A1'

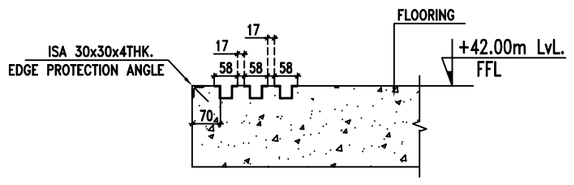

DETAIL–'A2'

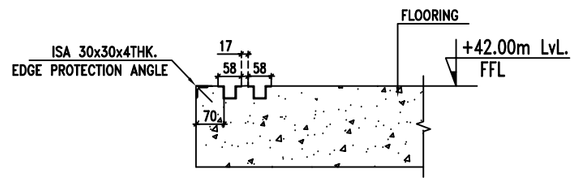

DETAIL–'A3'


NOTES :-

IF IN DOUBT ASK

FOR APPROVAL

02.03.17	R0	FOR APPROVAL	
DATE	NO	REVISIONS	BY
DATE	NO	ISSUED TO	BY
	MAIL	SITE	
	1	SITE PRINT	

KEY PLAN

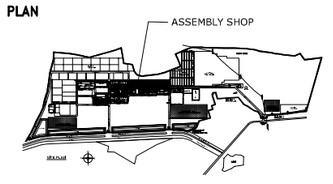

CLIENT

SUZUKI
SUZUKI MOTOR GUJARAT PVT. LTD.

DESIGN & BUILD CONTRACTOR

Shapoorji Pallonji ENGINEERING & CONSTRUCTION

ASSEMBLY SHOP

DRAWING NO: SC/SPCL/SMG/STR/RC/AS

TITLE : ASSEMBLY SHOP
TYPICAL SLIDING DOOR CONNECTION DETAIL

SCALE :1:40	
DRAWN BY : SAI	
CHECKED BY : MANIKANTA	
APPROVED BY : RAJESH RB	
DESIGN ENGR. : MANIKANTA	
DATE : 28.02.17	
REV. NO. R0	

N W E S