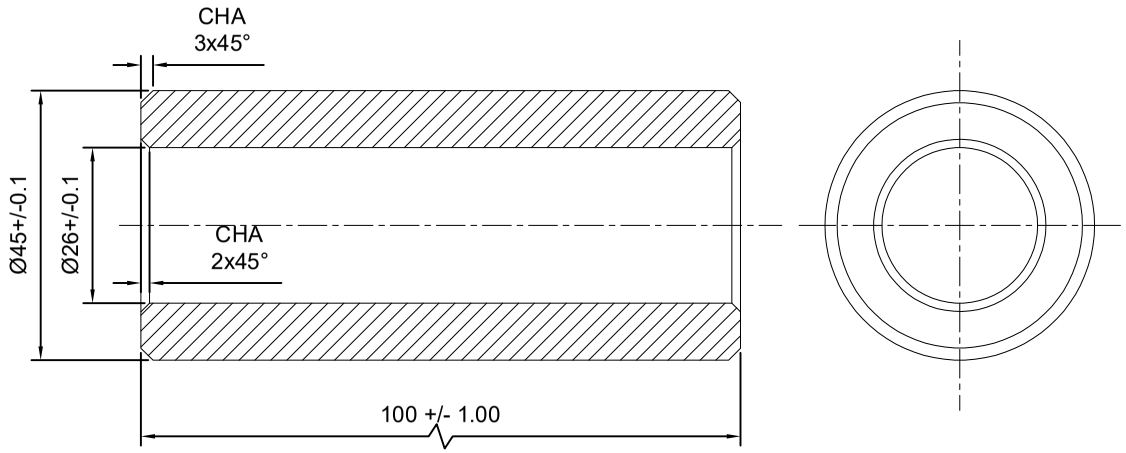


NOTE:~ MTL : MS

BUSH Ø45 X 100L = 20NOS

NOTE : ~ PLEASE MAINTAIN 7 MM GAP BETWEEN TWO LIP BUSHES.

This drawing & design is the property of NIHVA TECHNOLOGIES. Not to be sold or copied to any other concern.

TITLE				NIHVA TECHNOLOGIES PVT. LTD. PUNE
LIP MOUNTING BUSH				Tel : 020 66304033
	NAME	DATE	SIGN	Email:- info@nihva.com
DRAWN	SUJATA	31/12/2021		Website:- www.nihva.com
CHECK	G.PATIL	31/12/2021		CLIENT -
APPRD.	A.K	31/12/2021		PROJECT -
If any queries contact : design@nihva.com				SITE LOCATION -
ALL DIMENSION ARE IN mm				DWG. NO. : NIHVA/21-22/VDR/010
				SCALE: NTS / WT: / REV- 0