

DWG.NO: SALT_1729_STR_03_R0

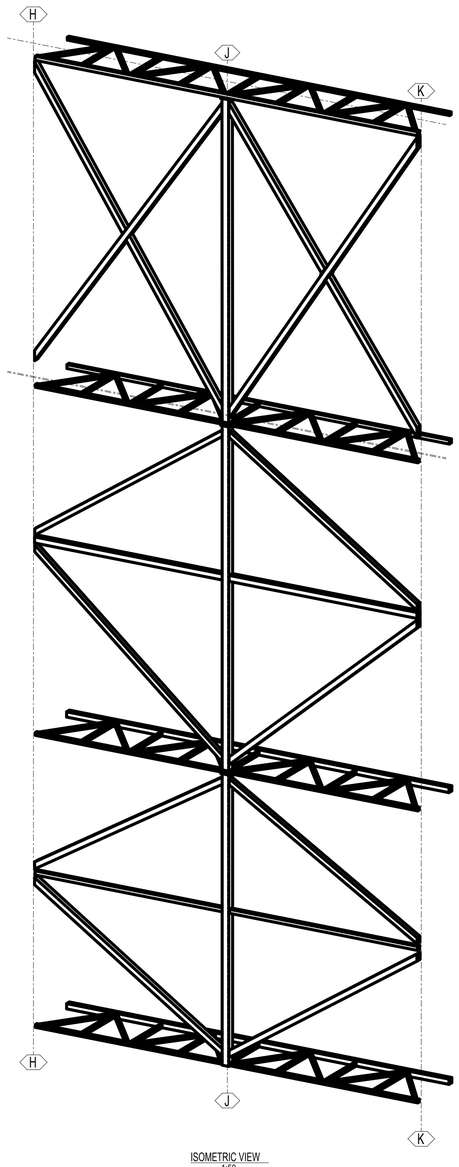


ISOMETRIC VIEW
1:50

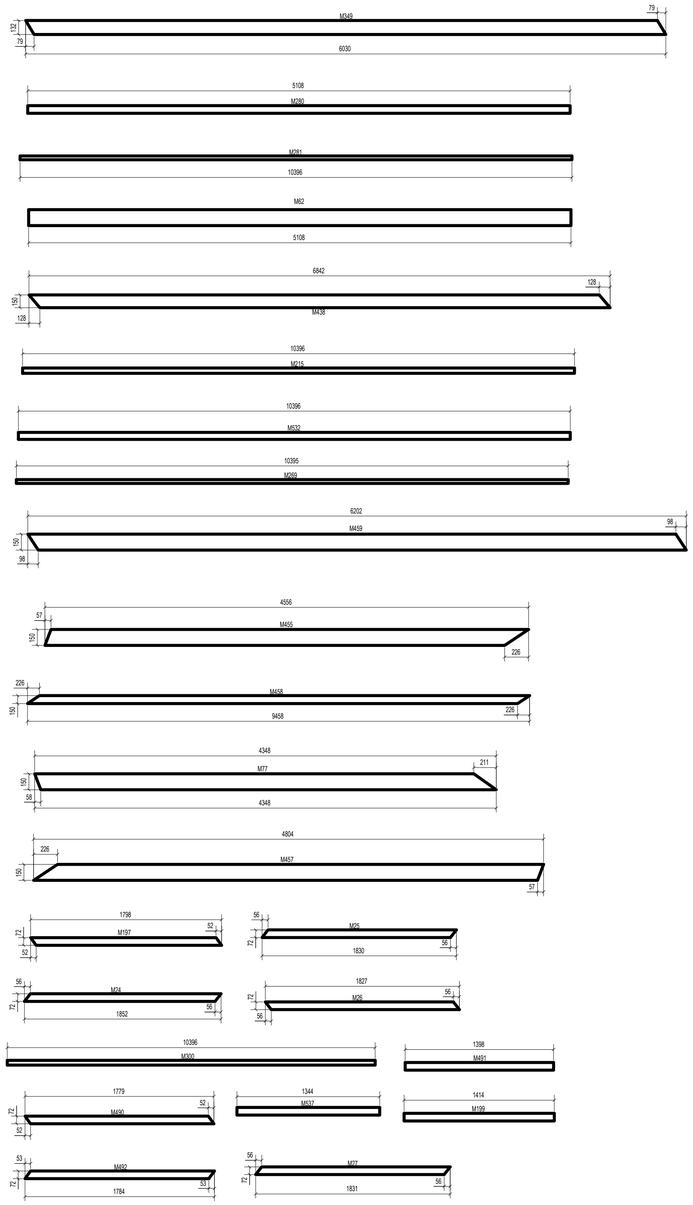



CUTTING DETAIL BETWEEN GRID H & GRID K						
PartPos	Profile	No.	Material	Length	Net Weight(kg	Gross Weight(kg)
M23	SHS72.0X72.0X3.2	4	IS2062	1848	12	48
M24	SHS72.0X72.0X3.2	4	IS2062	1852	12.02	48.08
M25	SHS72.0X72.0X3.2	2	IS2062	1830	11.88	23.76
M26	SHS72.0X72.0X3.2	4	IS2062	1827	11.86	47.44
M27	SHS72.0X72.0X3.2	4	IS2062	1831	11.89	47.56
M62	SHS150*4.5	1	IS2062	5108	105.01	105.01
M62	SHS150*4.5	1	IS2062	5108	105.02	105.02
M77	SHS150.0X150.0X6.0	1	IS2062	4348	111.14	111.14
M138	SHS150*8	1	IS2062	4571	158.23	158.23
M197	SHS72.0X72.0X3.2	4	IS2062	1798	11.7	46.8
M198	SHS72.0X72.0X3.2	4	IS2062	1850	12.01	48.04
M199	SHS72.0X72.0X3.2	14	IS2062	1414	9.48	132.72
M215	SHS100.0X100.0X6.0	1	IS2062	10396	176.51	176.51
M215	SHS100.0X100.0X6.0	1	IS2062	10396	176.52	176.52
M224	SHS100.0X100.0X6.0	1	IS2062	5108	86.72	86.72
M224	SHS100.0X100.0X6.0	1	IS2062	5108	86.74	86.74
M269	SHS72*5	1	IS2062	10395	109.34	109.34
M269	SHS72*5	1	IS2062	10396	109.35	109.35
M280	SHS72*5	2	IS2062	5108	53.73	107.46
M281	SHS72*5	1	IS2062	10396	109.35	109.35
M300	SHS132.0X132.0X4.8	1	IS2062	10396	194.47	194.47
M349	SHS132.0X132.0X4.8	1	IS2062	6030	111.28	111.28
M350	SHS132.0X132.0X4.8	1	IS2062	6226	114.78	114.78
M350	SHS132.0X132.0X4.8	1	IS2062	6227	114.79	114.79
M351	SHS132.0X132.0X4.8	1	IS2062	6827	125.55	125.55
M372	SHS180.0X180.0X8.0	1	IS2062	8630	366.5	366.5
M373	SHS180.0X180.0X8.0	1	IS2062	8106	344.25	344.25
M376	SHS180.0X180.0X8.0	1	IS2062	7307	310.32	310.32
M438	SHS150.0X150.0X5.0	1	IS2062	6842	149.41	149.41
M455	SHS150.0X150.0X5.0	1	IS2062	4556	98.2	98.2
M456	SHS150.0X150.0X5.0	1	IS2062	8993	195.42	195.42
M457	SHS150.0X150.0X5.0	1	IS2062	4804	103.72	103.72
M458	SHS150.0X150.0X5.0	1	IS2062	9458	205.43	205.43
M459	SHS150.0X150.0X5.0	1	IS2062	6202	135.84	135.84
M460	SHS150.0X150.0X5.0	1	IS2062	6217	136.15	136.15
M461	SHS150.0X150.0X5.0	1	IS2062	6041	132.45	132.45
M490	SHS72.0X72.0X3.2	4	IS2062	1779	11.56	46.24
M491	SHS72.0X72.0X3.2	13	IS2062	1398	9.37	121.81
M492	SHS72.0X72.0X3.2	2	IS2062	1784	11.6	23.2
M532	SHS132.0X132.0X4.8	1	IS2062	10396	194.47	194.47
M537	SHS72.0X72.0X3.2	1	IS2062	1344	9.01	9.01
PLT119	PL10*180	2	IS2062	221	3.12	6.24
PLT120	PL10*210	5	IS2062	240	3.96	19.8
	TOTAL					5143.12

NOTES :–

1. ALL DIMENSIONS ARE IN MM & LEVEL ARE IN METER.
2. ALL STRUCTURAL STEEL AS PER IS:2062.
3. PROVIDE WELDING AS PER IS:816.
4. PROVIDE MIN. 6MM WELD WITH MIN. WELD LENGTH OF 150MM.
5. USE ELECTRODS AS PER IS:814 (PT.–I).
6. FILLET/ BUTT WELD SHALL BE OF 6MM SIZE AND SHALL BE CONTINUOUS.
7. FABRICATION AND ERECTION SHALL BE AS PER IS:800 AND IS:803.
8. WELD SHALL BE GROUND SMOOTH.
9. ALL GUSSET PLATES SHALL BE MIN. 10 THK.
10. ALL M.S. BLACK BOLTS AND NUTS SHALL CONFORM TO IS:1363(PT. 1 TO 3).
11. STRUCTURE SHALL BE APPLIED WITH ONE COAT OF RED OXIDE ZINC CROMATE PRIMER AFTER FABRICATION FOLLOWED ONE MORE COAT BEFORE ERECTION. FINALLY APPLY 2 COATS OF SYNTHETIC ENAMAL OF APPROVED QUALITY.

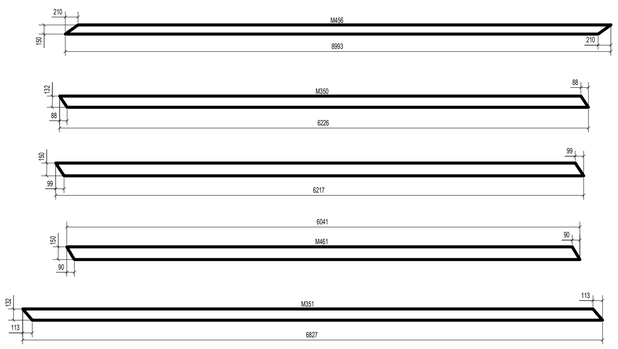

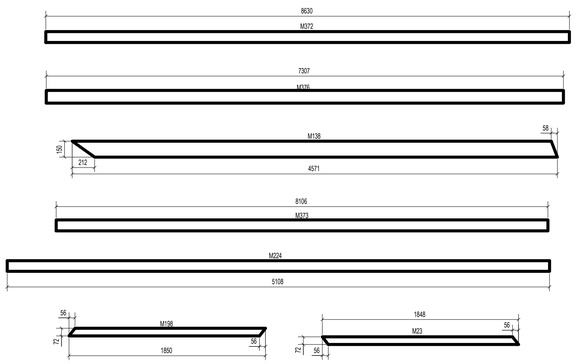

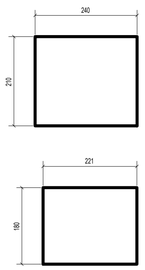

REV.NO.	DESCRIPTION.	REV.DATE	DRAWN.	CHKD.	APPD.
0	DRAWING FOR APPROVAL	27.12.22	AAK	HAB	HAB

DWG.TITLE :- CUTTING DETAIL BETWEEN GRID H TO K
DRAWING FOR DOOR FRAME

PROJECT	MEGADOOR INSTALLATION AT HYDRABAD AIRPORT
CLIENT	GMR

SALT Design Services
NIHVA NIHVA TECHNOLOGIES PVT. LTD.

SALT DESIGN SERVICES
NIHVA TECHNOLOGIES PVT. LTD. PUNE
Tel : 020 66304033
Email:- info@nihva.com
Website:- www.nihva.com

DRAWN :AAK	CHECKED : HAB	SCALE: 1:100
APPROVED : HAB	JOB CODE. : 1729	DATE: 27.12.2022

DWG.NO: SALT_1729_STR_03_R0	(SH-1OF1)	REV. - R0
		SIZE. - A0

A1 [841 x 594]