

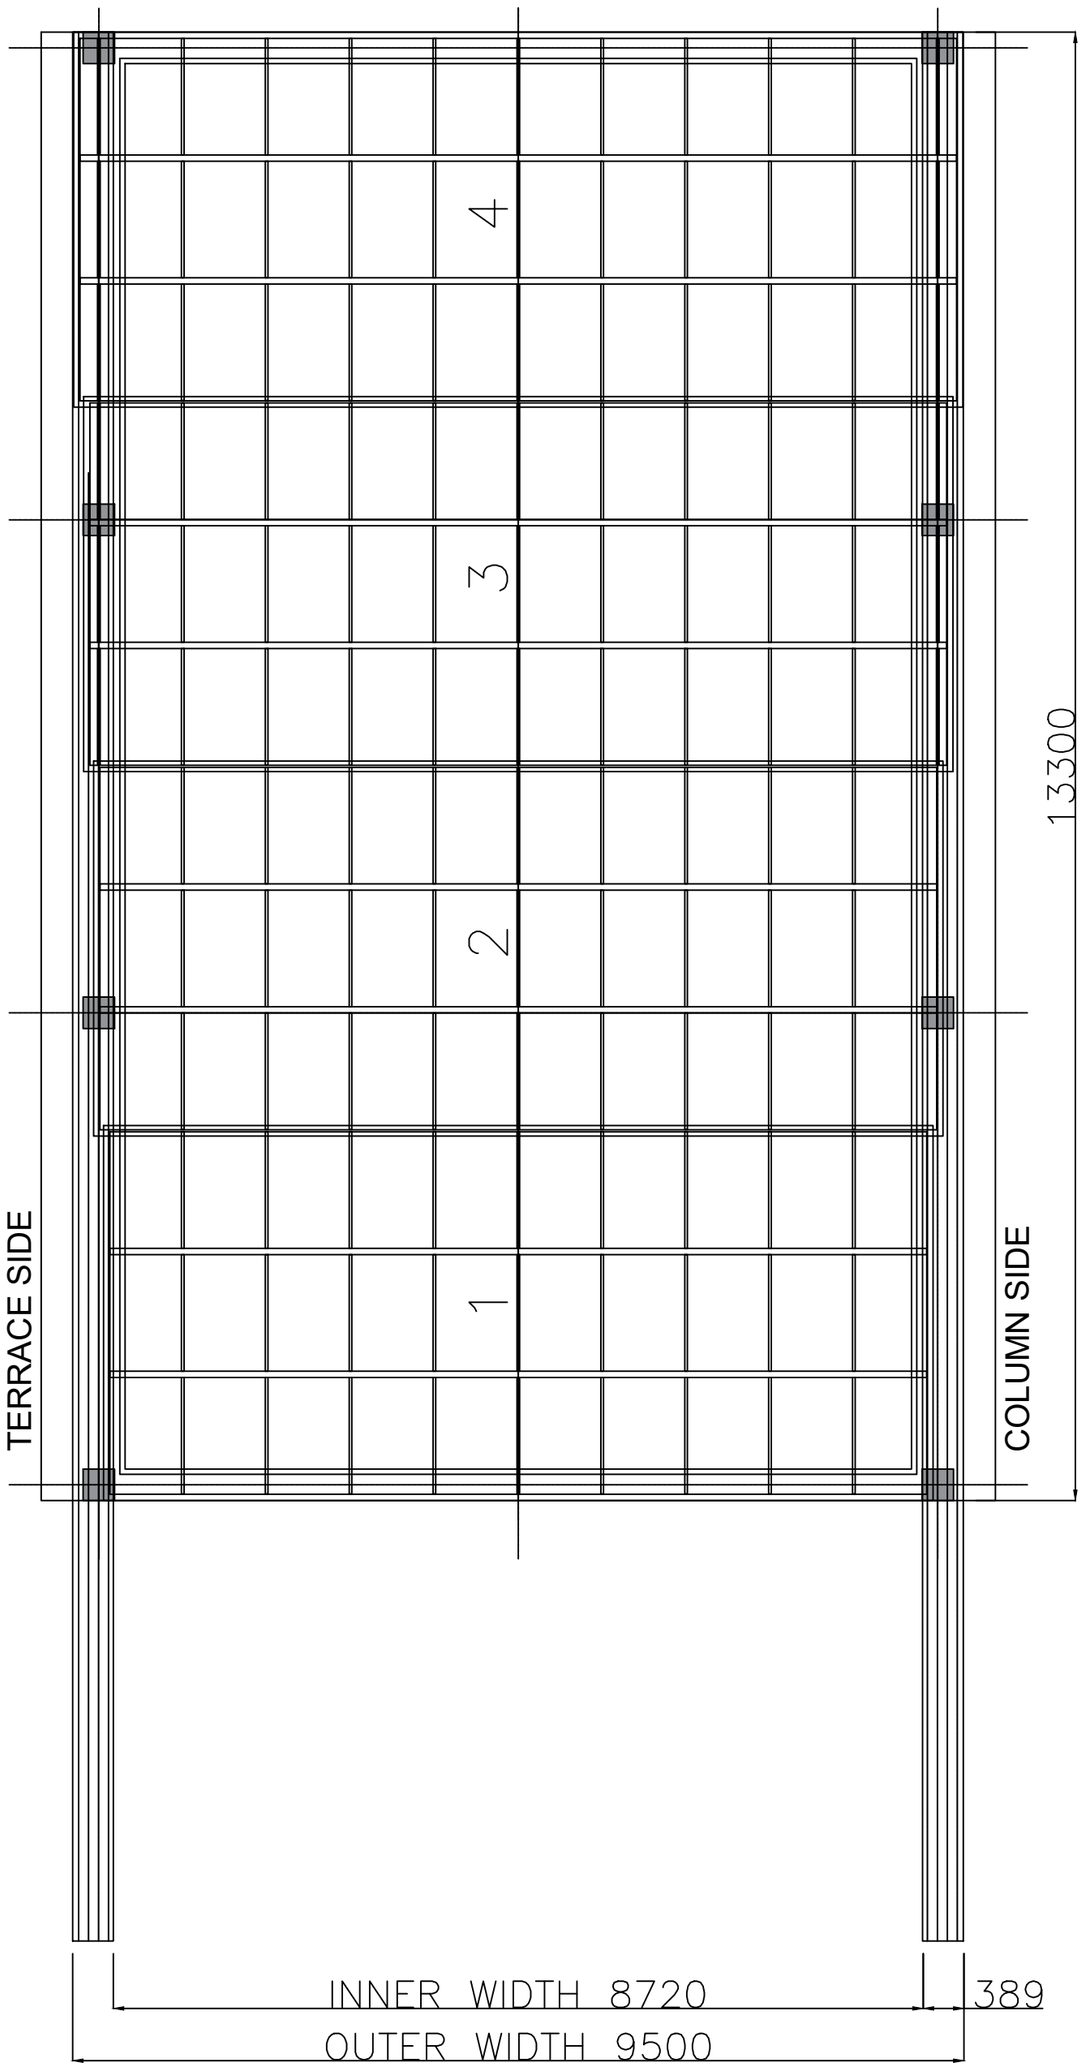


ENCLOSED PLAN

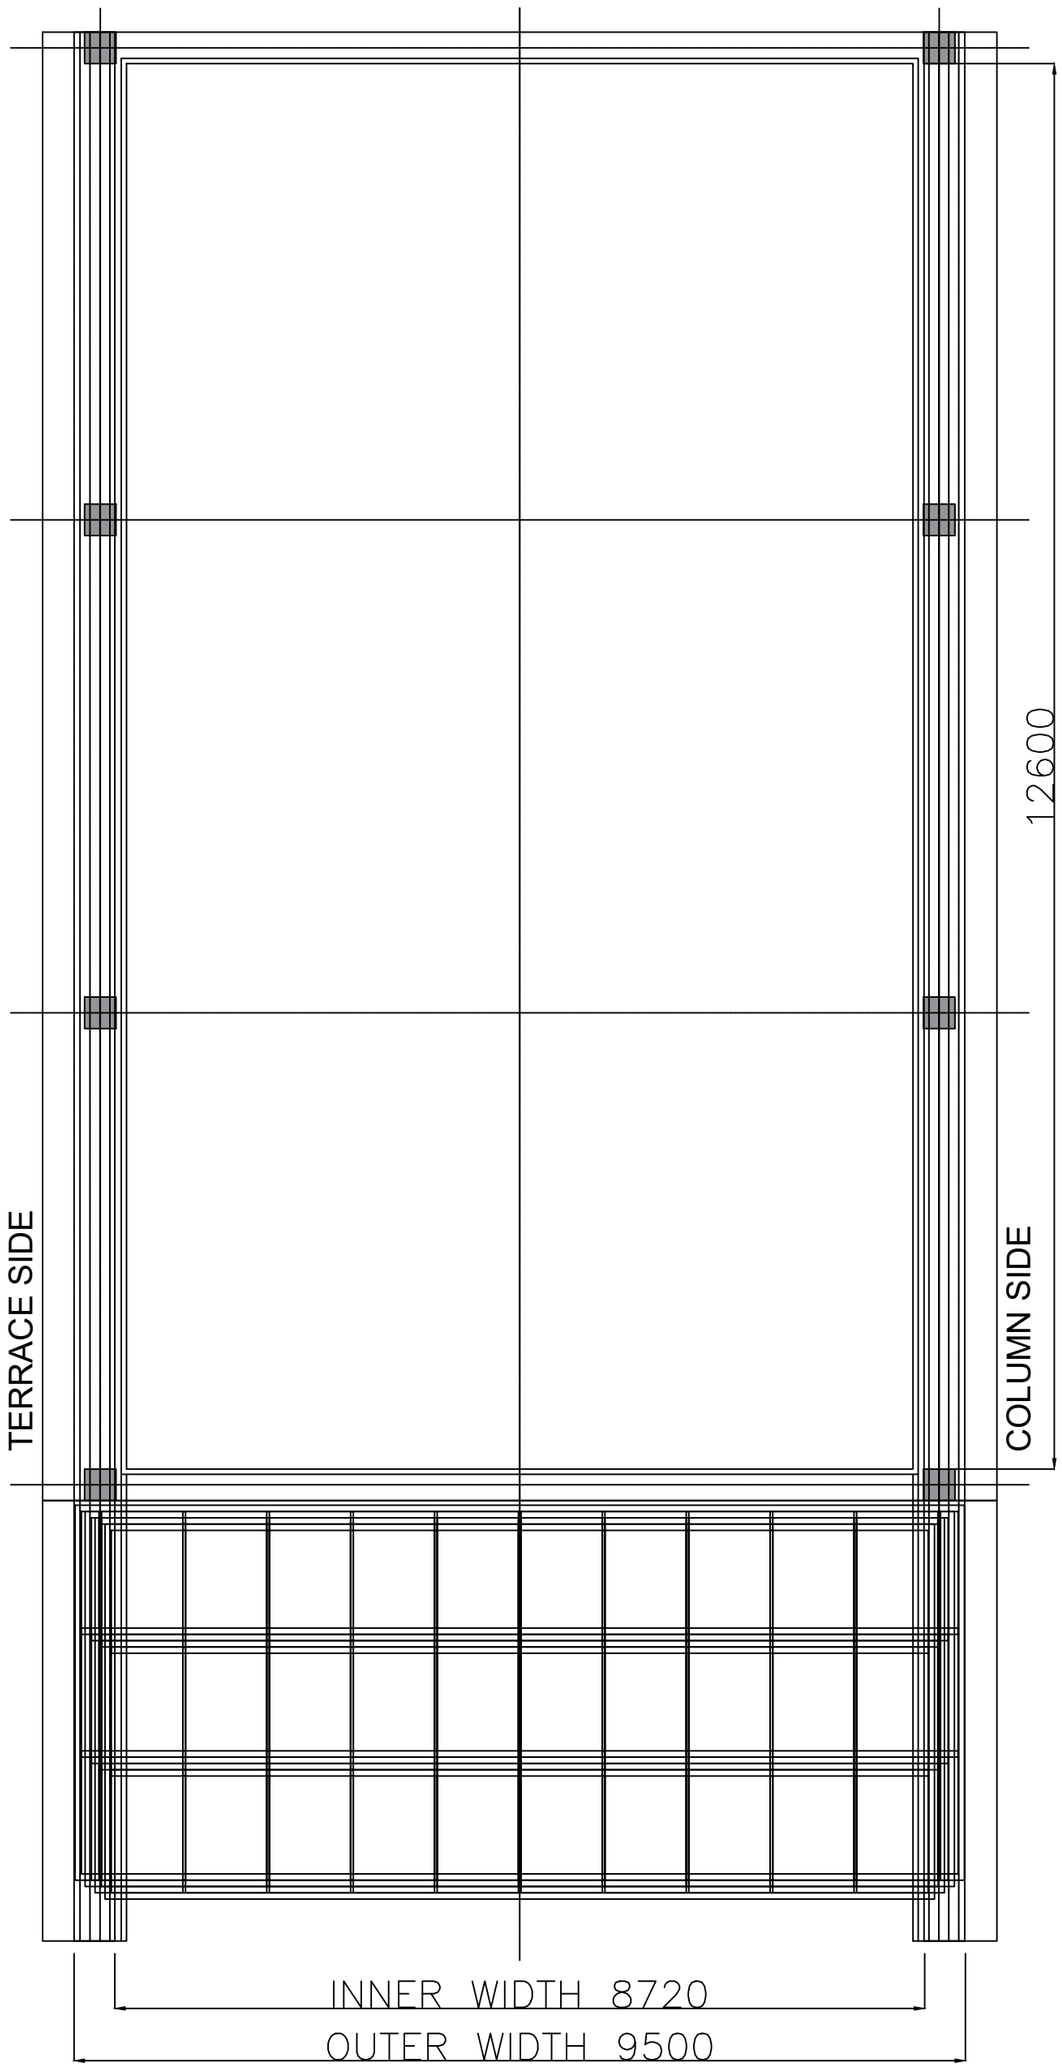

STACKED PLAN

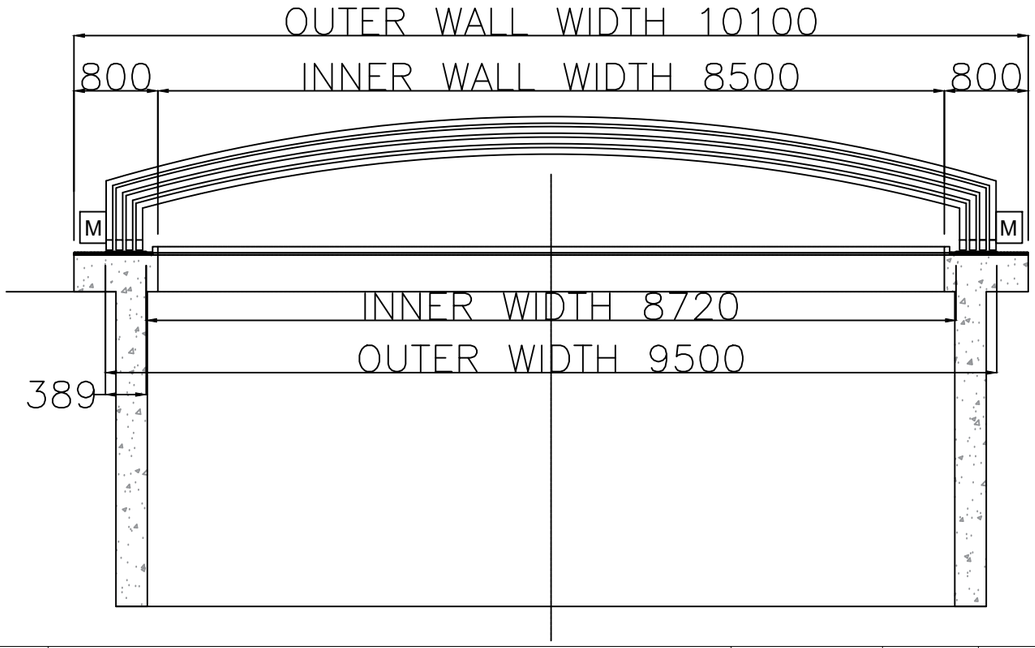

STANDARD PART		
PART LIST	LENGTH	QTY
GNT 001	17.5 M	2
GNT 002	17.5 M	6
GNT 007	3.425 M	8

REV.	DESCRIPTION.	REVISED BY	SIGN	DATE
002	REVISED GA DRAWING PER SINGLE SIDE OUT OF CLEAR OPENING	MAHESH S.		08.10.22
001	REVISED GA DRAWING PER BI-PARTING WITHIN CLEAR OPENING	MAHESH S.		
000	RELEASED GA DWG FOR APPROVAL	GAURAV J.		

This drawing & design is the property of NIHVA TECHNOLOGIES. Not to be sold or copied to any other concern.

TITLE
ASSLY LAYOUT

	NAME	SIGN	DATE
DRAWN	MAHESH S.		08.10.22
CHECK	MAHESH S.		08.10.22
APPRD.	VIJAY T.		08.10.22

NIHVA TECHNOLOGIES PVT. LTD.

ARCWAY TECH STRUCTURES

If any queries contact : projectsautomation@nihva.com

ALL DIMENSION ARE IN mm

CLIENT - MR. PRANAV

LOCATION - NOIDA_IN

PRODUCT - RETRACTABLE ROOF

NIHVA\22-23\02XX | REV- 0

SCALE: NTS | SHEET: 01 OF 01