

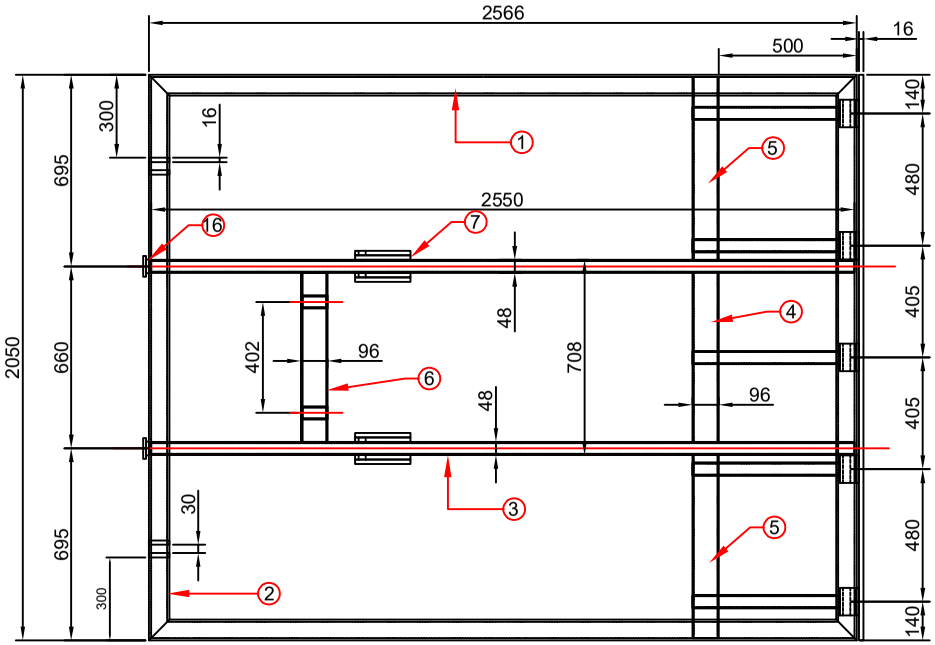


BOM			
SL NO.	DESCRIPTION	SPECIFICATION	QTY
1	ISA	75X75X8X2566	2NOS
2	ISA	75X75X8X2050	2NOS
3	RECT. TUBE	96X48X4.8X2550	2NOS
4	RECT. TUBE	96X48X4.8X612	1NO
5	RECT. TUBE	96X48X4.8X596	2NOS
6	RECT. TUBE	96X48X4.8X612	1NO
7	MS FLAT	75X16X200L	4NOS
8	CYLINEDER MTNG BKT	157X16X200L	4NOS
9	MS FLAT	50X5X100L	2NOS
10	RECT.TUBE	96X48X4.8X382	5NOS
11	RECT.TUBE	96x48.x4.8X589	5NOS
12	RECT.TUBE	96x48X4.8X101	2NOS
13	MS BLOCK(DECK HLDNG BKT)	75X60X100	5NOS
14	MS FLAT	75X16X2050	1NO
15	MS FLAT	75X10X105	1NO
16	MS FLAT	50X10X75	2NOS
17	MS FLAT	75X10X105	2NOS
18	MS FLAT	50X10X100	5NOS

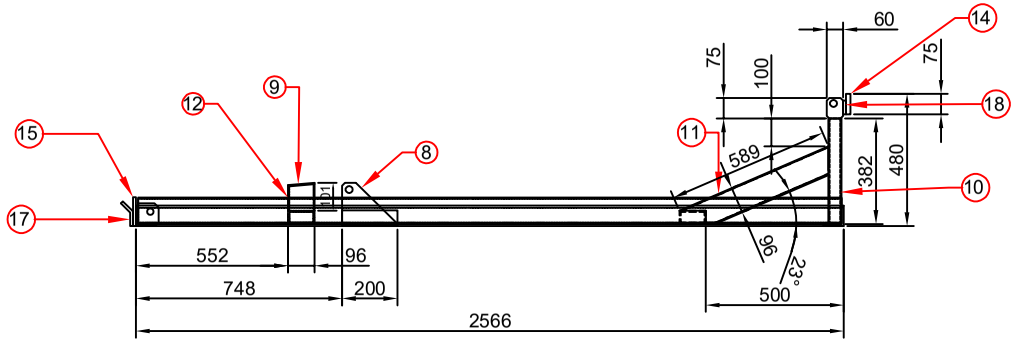

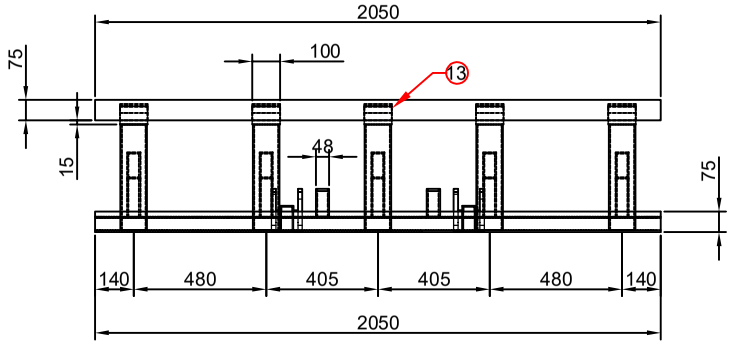

NOTE:-

1.All dimension are in MM

2.Above given quantity in the table is only for the single dock

This drawing & design is the property of NIHVA TECHNOLOGIES. Not to be sold or copied to any other concern.

TITLE:- BASE FRAME

NIHVA TECHNOLOGIES PVT. LTD.
NIHVA TECHNOLOGIES PVT. LTD. PUNE
Tel : 020 66304033
Email:- info@nihva.com
Website:- www.nihva.com

	NAME	DATE	SIGN
DRAWN	SUJATA	21/04/2022	
CHECK	M.SUTAR	21/04/2022	
APPRD.			

CLIENT - ABHI BUILDCON

LOCATION - PUNE

PRODUCT - DOCK LEVELER

If any queries contact : design@nihva.com

DWG NO:-NIHVA/22-23/MFG/0001 REV- 0

ALL DIMENSION ARE IN mm

SCALE: NTS SCALE:-- 1:1 SHEET: 01 OF 01

Rev No.	Revision	Date	Revised By