


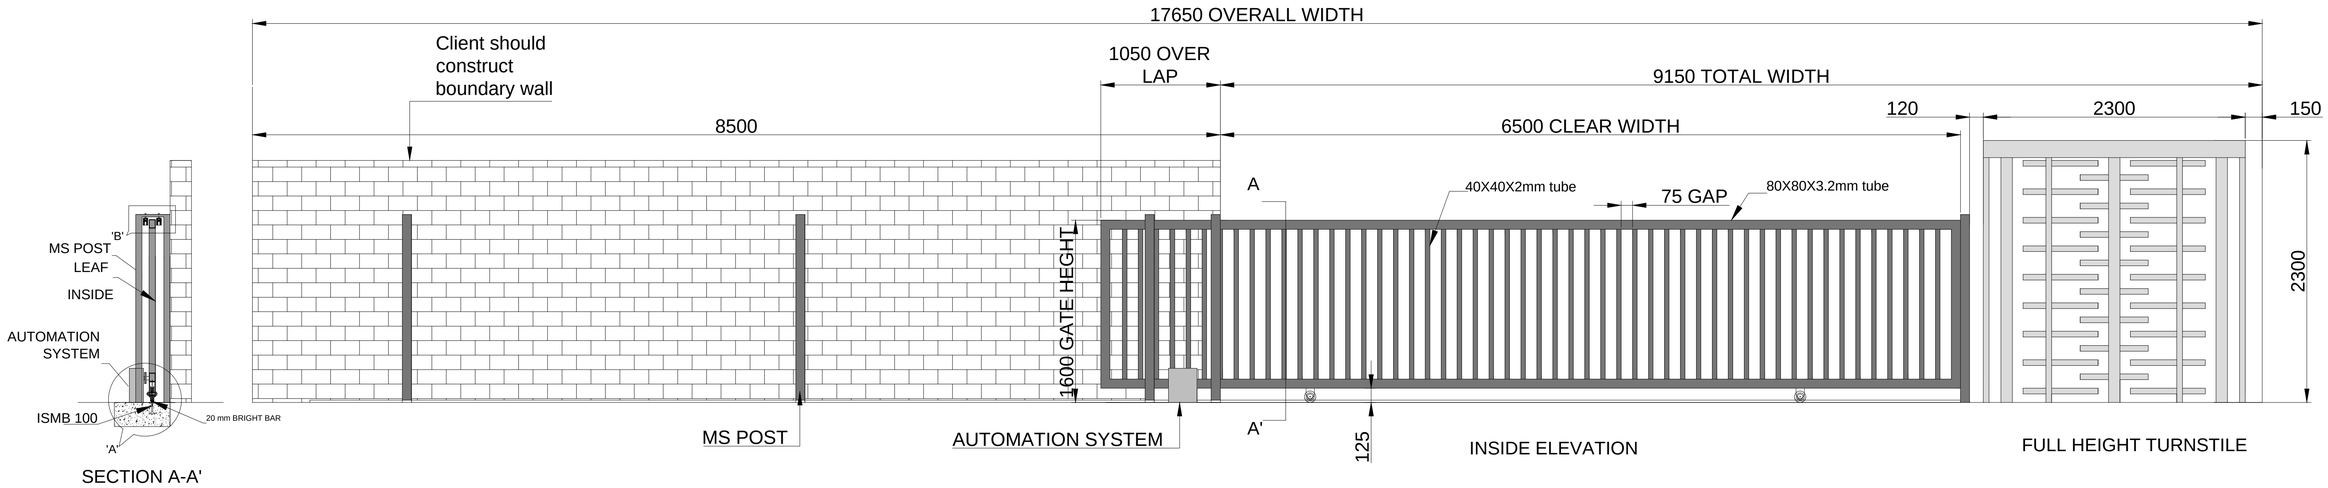


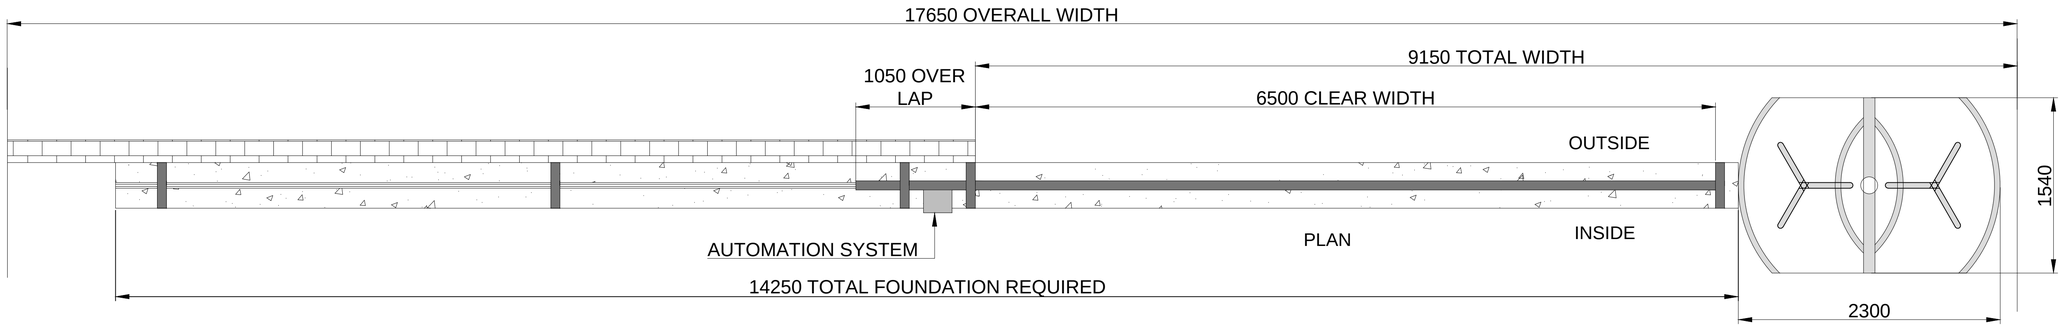

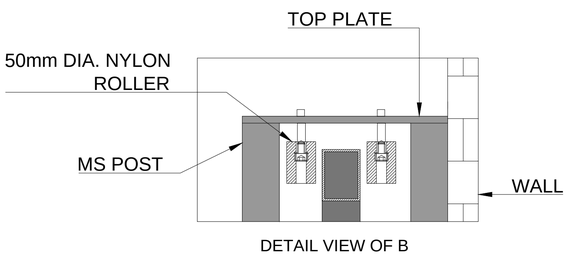

DETAIL VIEW OF B

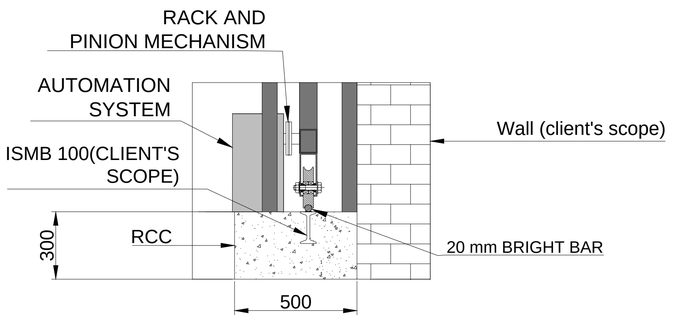

DETAIL VIEW OF A

NOTE-
1. ALL REQUIRED CIVIL WORK WILL BE IN CLIENTS SCOPE.
2. ONE COAT OF RED OXIDE & TWO COAT OF APPROVED RAL SHADE WILL BE GIVEN TO THE GATE.
3.IF NECESSARY GATE LEAF WILL BE IN TWO PARTS FOR TRANSPORTATION & WILL BE WELD TOGETHER ON SITE.

GATE WIDTH	GATE HEIGHT	QUANTITY	LOCATION
6500mm	1600mm	1 NOS	

This drawing & design is the property of NIHVA TECHNOLOGIES. Not to be sold or copied to any other concern.

TITLE
AUTOMATIC SINGLE LEAF SLIDING GATE & TURNSTILE

	NAME	DATE
DRAWN	OMKAR	22/09/17
CHECK	SAGAR P.	22/09/17
REV.		
APPROVAL	S.S	22/09/17

If any queries contact : projects@nihva.com

ALL DIMENSION ARE IN mm

NIHVA TECHNOLOGIES PVT. LTD.
NIHVA TECHNOLOGIES PVT. LTD. PUNE
Tel : 020 66304033
Email:- info@nihva.com
Website:- www.nihva.com

CLIENT - BHARAT FORGE
PROJECT - KALYANI CENTRE OF TECHNOLOGY & INNOVATION
SITE LOCATION - MUNDHWA,PUNE
DWG. NO. : NIHVA/17-18/0213
SCALE: NTS | WT: | SHEET: 01 OF 01