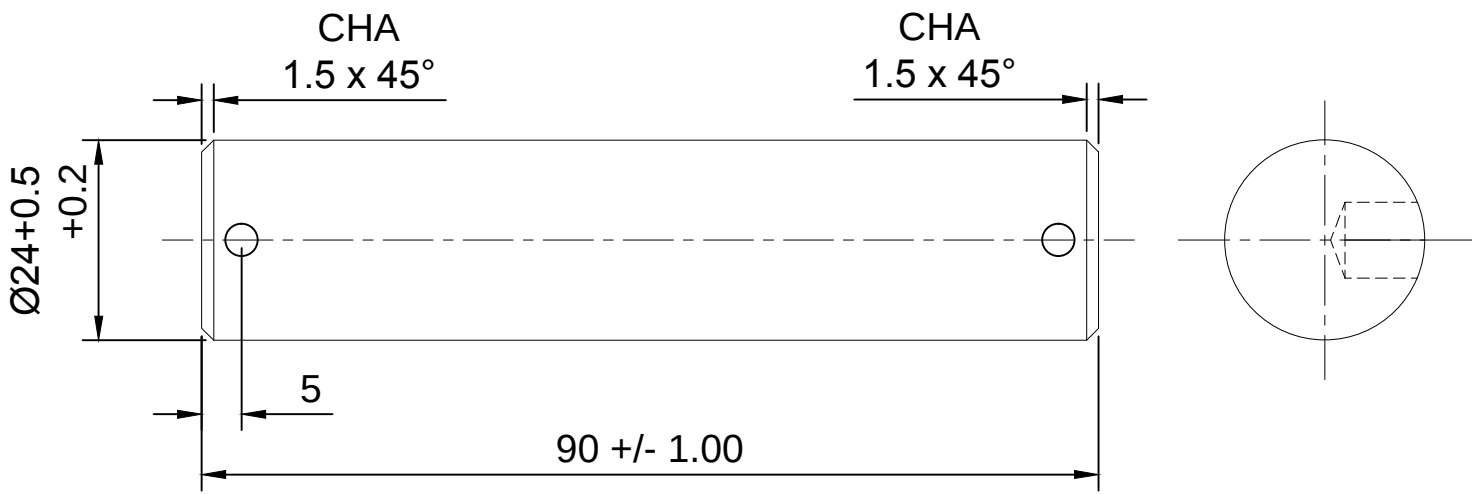


NOTE:~ MTL : EN8

Ø24 X 93L = 4 NOS (HARDENING & GRINDING)

This drawing & design is the property of NIHVA TECHNOLOGIES. Not to be sold or copied to any other concern.

TITLE				
MAINTENANCE STOPPER				NIHVA TECHNOLOGIES PVT. LTD. PUNE Tel : 020 66304033 Email:- info@nihva.com Website:- www.nihva.com
	NAME	SIGN	DATE	
DRAWN	P.V.A		06.03.2019	CLIENT -
CHECK	V.M.T		06.03.2019	PROJECT - NDL 385 & 386
APPRD.				SITE LOCATION -
If any queries contact : design@nihva.com				DWG. NO. : NIHVA/18-19/VDR/420
ALL DIMENSION ARE IN mm				SCALE: NTS / WT: / REV- 0