



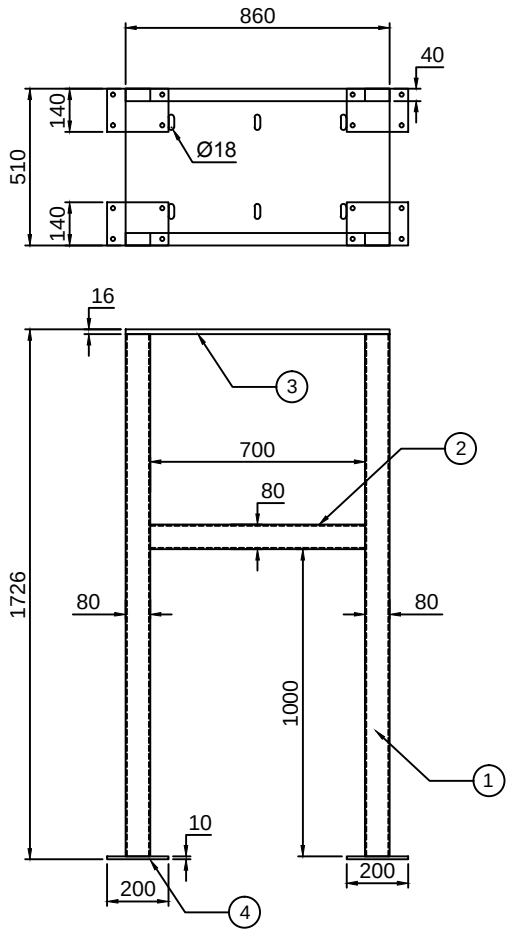


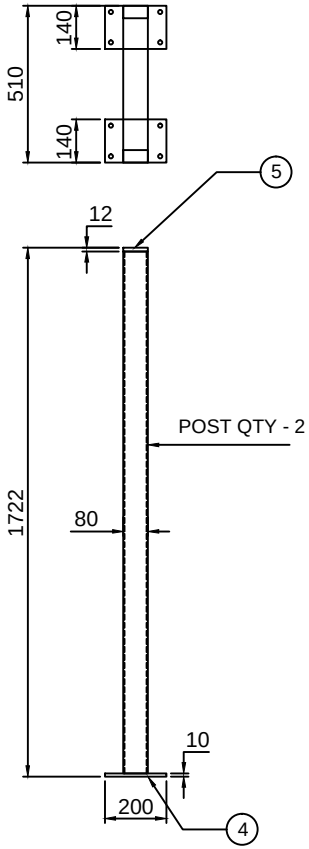

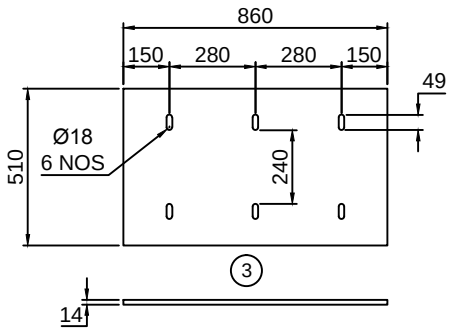

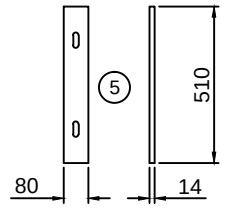

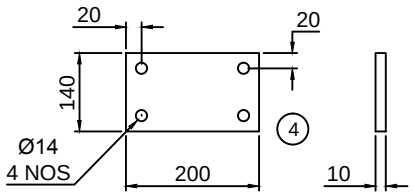

SR NO	DESCRIPTION	SPECIFICATION	QTY
5	PROFILE	80 X 12 X 510L	2 NOS
4	PROFILE	140 X 10 X 200L	8 NOS
3	PROFILE	510 X 14 X 860L	1 NO
2	R. TUBE	80 X 40 X 4 THK X 700L	2 NOS
1	R. TUBE	80 X 40 X 4 THK X 1700L	8 NOS

This drawing & designing is the property of NIHVA TECHNOLOGIES. Not to be sold or copied to any other concern.

TITLE
POST DETAILS

NIHVA
NIHVA TECHNOLOGIES PVT. LTD.

NIHVA TECHNOLOGIES
PVT. LTD. PUNE
Tel : 020 66304033
Email:- info@nihva.com
Website:- www.nihva.com

	NAME	SIGN	DATE
DRAWN	P.A		03.12.19
CHECKED	G.J		03.12.19
APPROVED			

CLIENT -
PROJECT -
SITE LOCATION -
DWG. NO. : NIHVA/19-20/VDR/234
REV: R00
If any queries contact : projects@nihva.com
SCALE: NTS
WT:
SHEET: 01 OF 01
ALL DIMENSION ARE IN mm