


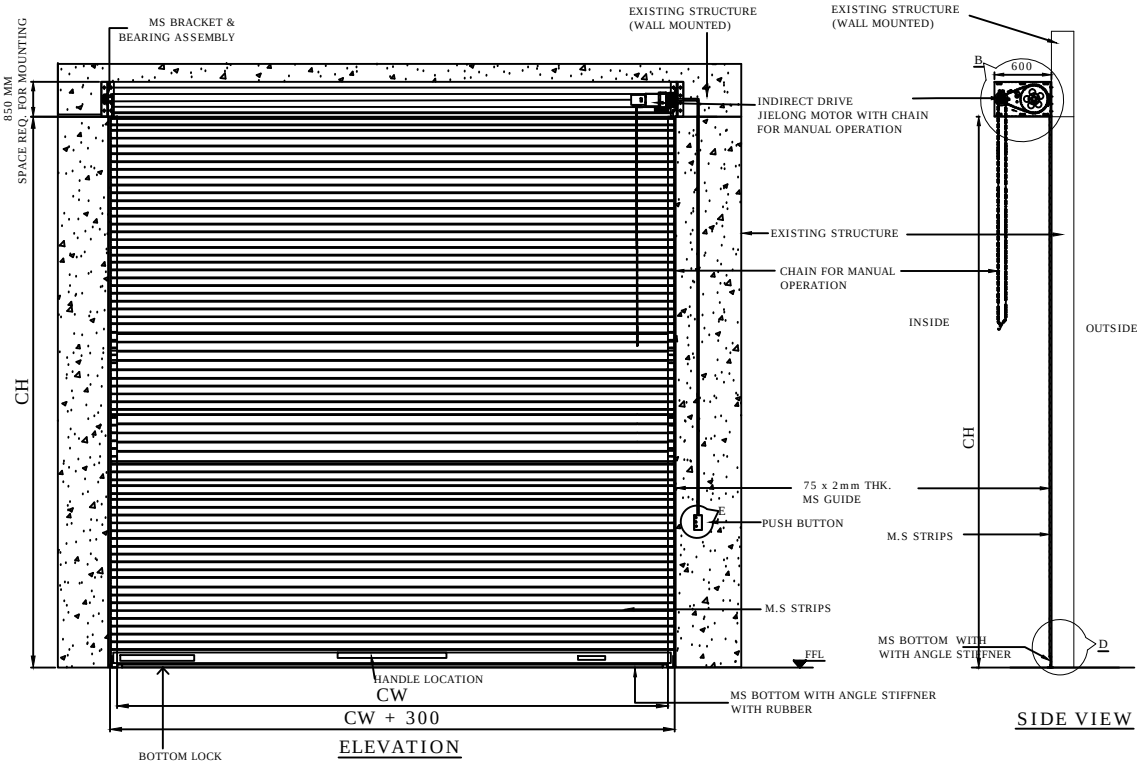


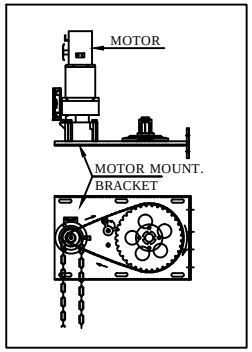


DETAILS : A & B

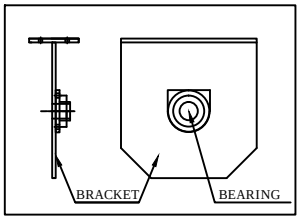


DETAILS : C

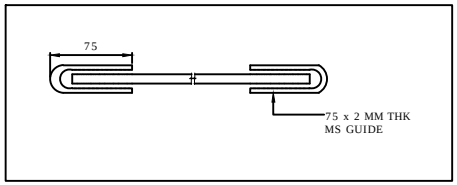

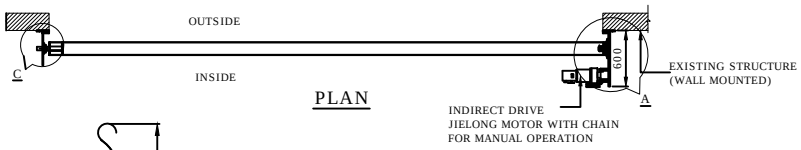

PLAN

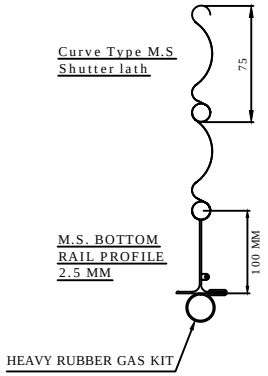

DETAILS : D

(NOTE: SHUTTER IS WALL MOUNTED.)

3555	5000	1	RAL - 9010
3575	5000	1	RAL - 9010
CLEAR WIDTH (CW)	CLEAR HEIGHT (CH)	QUANTITY	RAL COLOR

REV NO	REV DATE	DRAWN	REMARK
R01	25.11.2019	P.A	1.CLEAR WIDTH & HEIGHT CHANGE.

This drawing & design is the property of NIHVA TECHNOLOGIES. Not to be sold or copied to any other concern.

TITLE: WALL MOUNTED MOTORIZED ROLLING SHUTTER

	NAME	SIGN	DATE
DRAWN	P.A		19.11.2019
CHECK	G.J		19.11.2019
APPRD.			

If any queries contact : design@nihva.com

ALL DIMENSION ARE IN mm

NIHVA TECHNOLOGIES PVT. LTD.

NIHVA TECHNOLOGIES PVT. LTD. PUNE
Tel : 020 66304033
Email:- info@nihva.com
Website:- www.nihva.com

CLIENT - INGERSOLL RAND (INDIA) LIMITED

PROJECT -

SITE LOCATION - GUJARAT

DWG. NO. : NIHVA/19-20/0156/R01 | REV- R01

SCALE: NTS | WT: | SHEET: