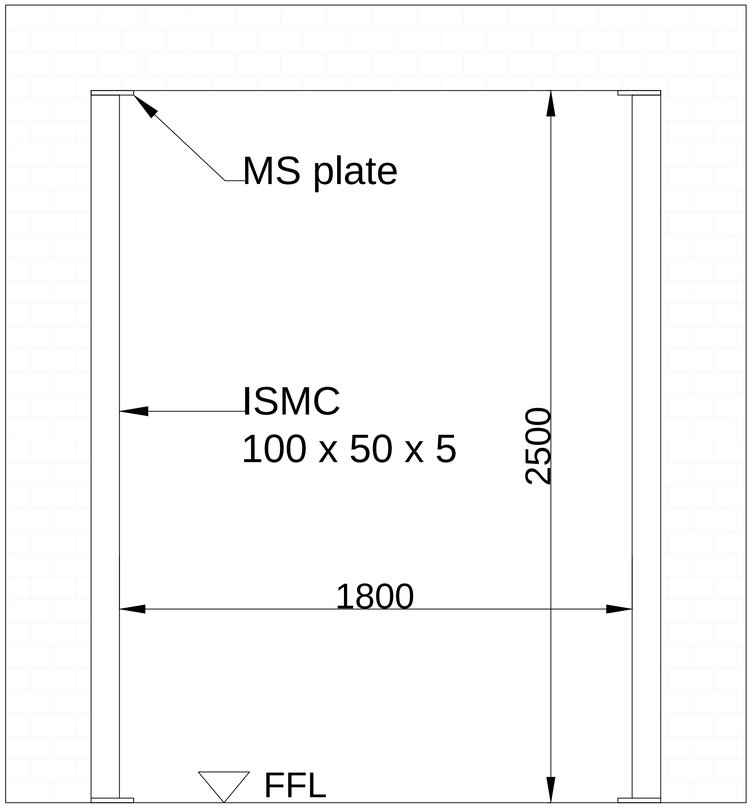

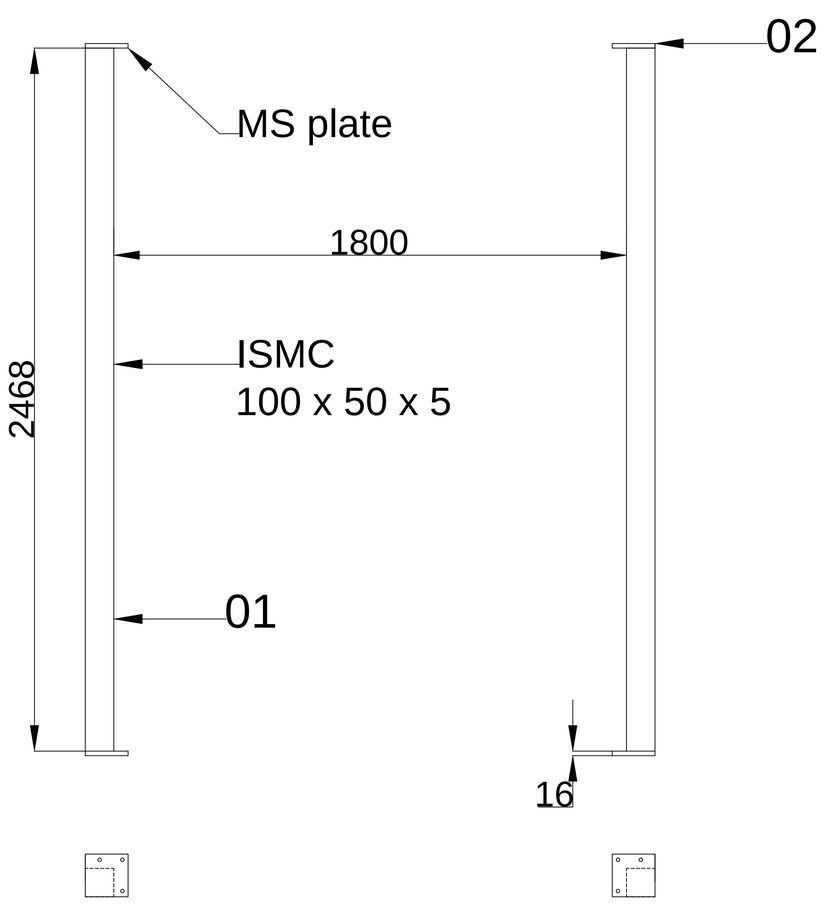

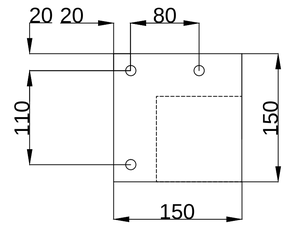

MS plate
Scale: 3:1

Door Structure

BILL OF MATERIAL

Sr. No.	Discription	Qty
01	ISMC 100 x 50 x 5, L = 2468	2 nos
02	MS plate 150 x 150 x 16 thk	4 nos
03	Anchor Fastener M12 x 150	12 nos

This drawing & design is the property of NIHVA TECHNOLOGIES. Not to be sold or copied to any other concern.

TITLE	STRUCTURE			NIHVA TECHNOLOGIES PVT. LTD. PUNE
	NAME	SIGN	DATE	Tel : 020 66304033
DRAWN	G.P.		19.12.21	Email:- info@nihva.com
CHECK	A.K.		19.12.21	Website:- www.nihva.com
APPV'ED	V.T		19.12.21	CLIENT :- COLD AIR SOLUTIONS
				PROJECT :- HIGH SPEED DOOR
				LOCATION :-

If any queries contact : design@nihva.com	DWG. NO. :- NIHVA/21-22/MFG/006	REV :- R00
ALL DIMENSION ARE IN mm	SCALE: NTS	WT:	SHEET: 01 OF 01