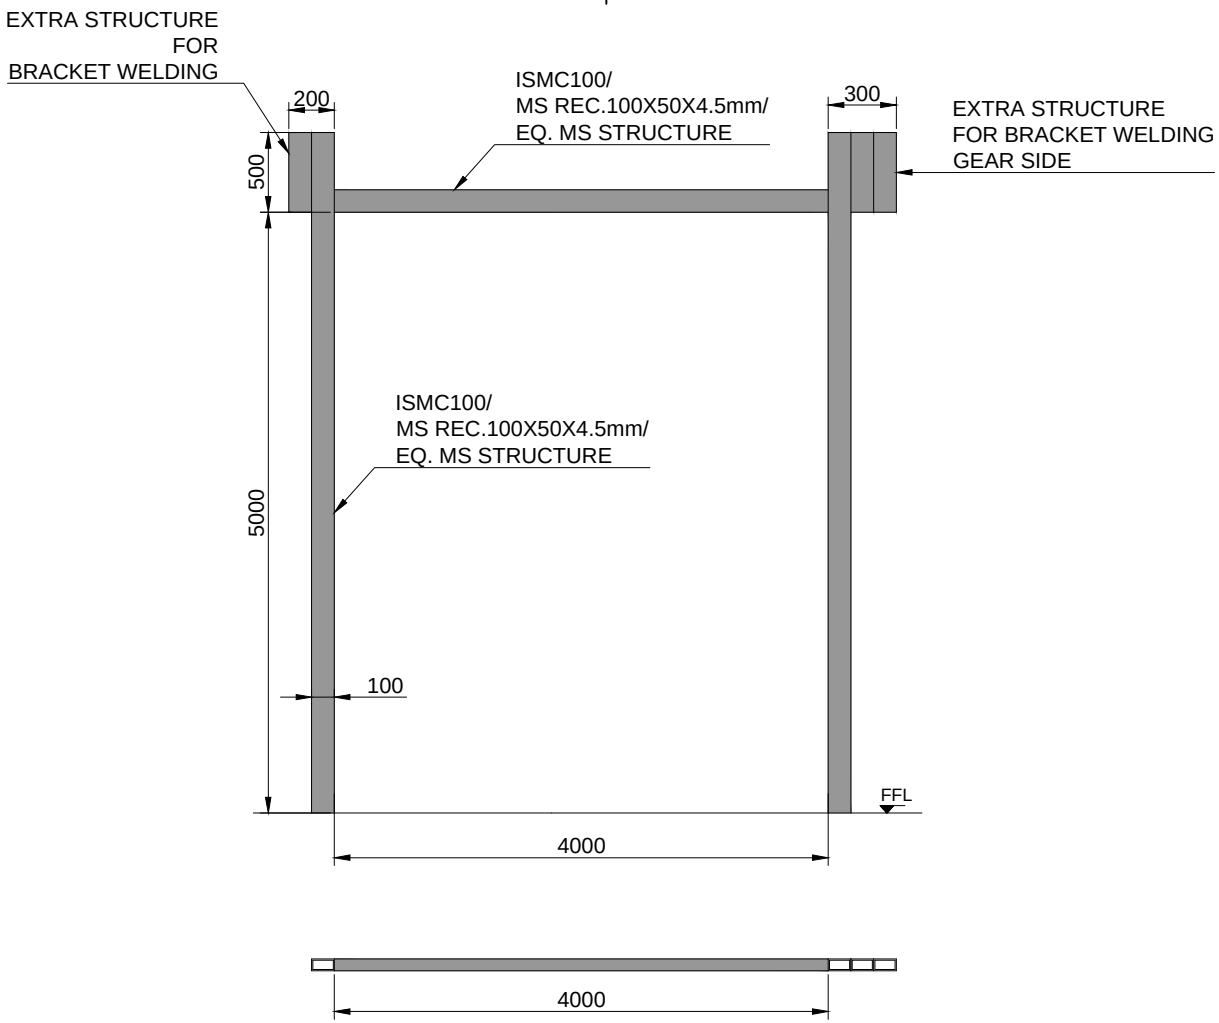


S.N.	LOCATION	SIZE	QUANTITY
1	B400	4000(W)X5000(H)	2
2	B500	4000(W)X5000(H)	2
3	B600	4000(W)X5000(H)	2

NOTE-
1. ALL CIVIL WORK WILL BE CLIENT'S SCOPE.
2.STRUCTURE REQUIRED FOR SHUTTER IS IN CLIENT'S SCOPE.
3.FINAL FINISH OF SHUTTER WILL BE IN POWDER COATING OF APPROVED COLOR i.e.RAL 7001.

TOLERANCE - ±10mm

This drawing & design is the property of NIHVA TECHNOLOGIES. Not to be sold or copied to any other concern.

TITLE STRUCTURE FOR GEAR OPERATED ROLLING SHUTTER 4mX5m

NIHVA TECHNOLOGIES PVT. LTD.

NIHVA TECHNOLOGIES PVT. LTD. PUNE
Tel : 020 66304033
Email:- info@nihva.com
Website:- www.nihva.com

	NAME	SIGN	DATE
DRAWN	OMKAR		26-04-2018
CHECK	PRADEEP		26-04-2018
APPRD.	PRADEEP		26-04-2018

CLIENT - INDOSPACE
PROJECT - BUILDING B500 & B600
SITE LOCATION - CHAKAN 3
If any queries contact : design@nihva.com
DWG. NO. : NIHVA/18-19/0018 REV- 0
ALL DIMENSION ARE IN mm
SCALE: NTS WT: SHEET: 01 OF 01