

Abbrevation's:
WOW-Wall Opening Width
WOH-Wall Opening Height
UC-Under Cut
FFL-Finished Floor Level

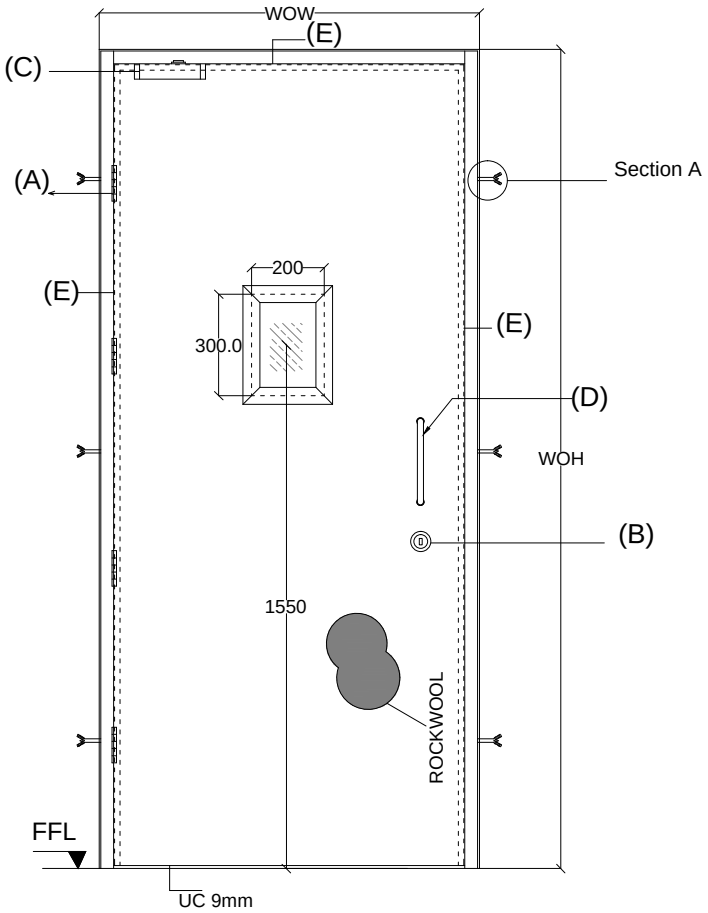

ELEVATION



TOP VIEW

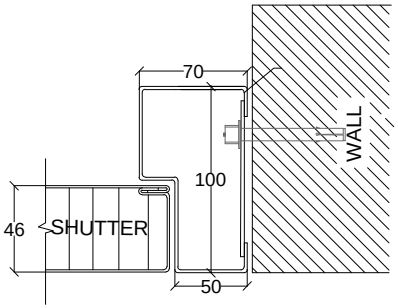

Section A

ASSESORIES DETALES

(A) HINGES: SS Ball bearing butt hinges 100x75x3mm
3S2BB403030-MS-ASSA ABLOY.

(B) LOCK : Mortise Dead lock-18 P4.50-S-ASSA ABLOY,
Cylinder with one side key & other side turn bolt on Rose
(80MM)SS-80mmTTSN-S-ASSA ABLOY.

(C) DOOR CLOSER: C7722-ASSA ABLOY

(D) HANDLE : 'D' HANDLE (BOTH SIDE) dia 200mmX22mm
YEH-11-200-ASSA ABLOY.

(E) SEAL : RP 48 weather strip closed sponge self adhesive
EPDM bulb seal.

Shutter thickness : 46 mm
Frame Sheet thick : 1.5mm
Shutter sheet thick : 1.2mm
Fixing : On Solid Brick plastered wall with Anchors

NOTE:- *All Dimensions are in mm.
*Tolerance:-All Linear Dimensions ±3mm,Others ±0.5mm.
*The Drawing Is For Location of Hardware only. Drawing Does Not Represent The Hardware For More Clarity, Please Go Through Hardware Broucher.

COLOR
1.TRAFFIC WHITE (RAL 9016)
2.LIGHT GREY (RAL 7035)
3.GENTION BLUE (RAL 5010)
4.SIGNAL RED (RAL 3001)

NOTE- 1. CLIENT SHOULD MENTION COLOR FOR DOOR.

Steel door size

WOW	WOH	TYPE 1	TYPE 2	TYPE 3	TYPE 4	QUANTITY
800mm	2000mm	01				01 NOS

REV -1. VISION PANEL IS ADDED.

This drawing & designing is the property of NIHVA TECHNOLOGIES. Not be sold or copy to any other concern.

TITLE: FIRE DOOR (SINGLE LEAF)				NIHVA TECHNOLOGY PVT. LTD. PUNE
	NAME	SIGN.	DATE	Tel : 020 66304033
DRAWN	SURAJ		20/02/18	Email:- info@nihva.com
CHECK	OMKAR		20/02/18	Website:-www.nihva.com
APPRD.	SHEKHAR		20/02/18	CLIENT -FERRERO INDIA PVT LTD.
If any queries contact: design@nihva.com				PROJECT -
ALL DIMENSION ARE IN mm				SITE - BARAMATI.
				DWG. NO. - NIHVA/17-18/0368/R01 REV. :-1
				SCALE: NTS WT: SHEET: 01 OF 01