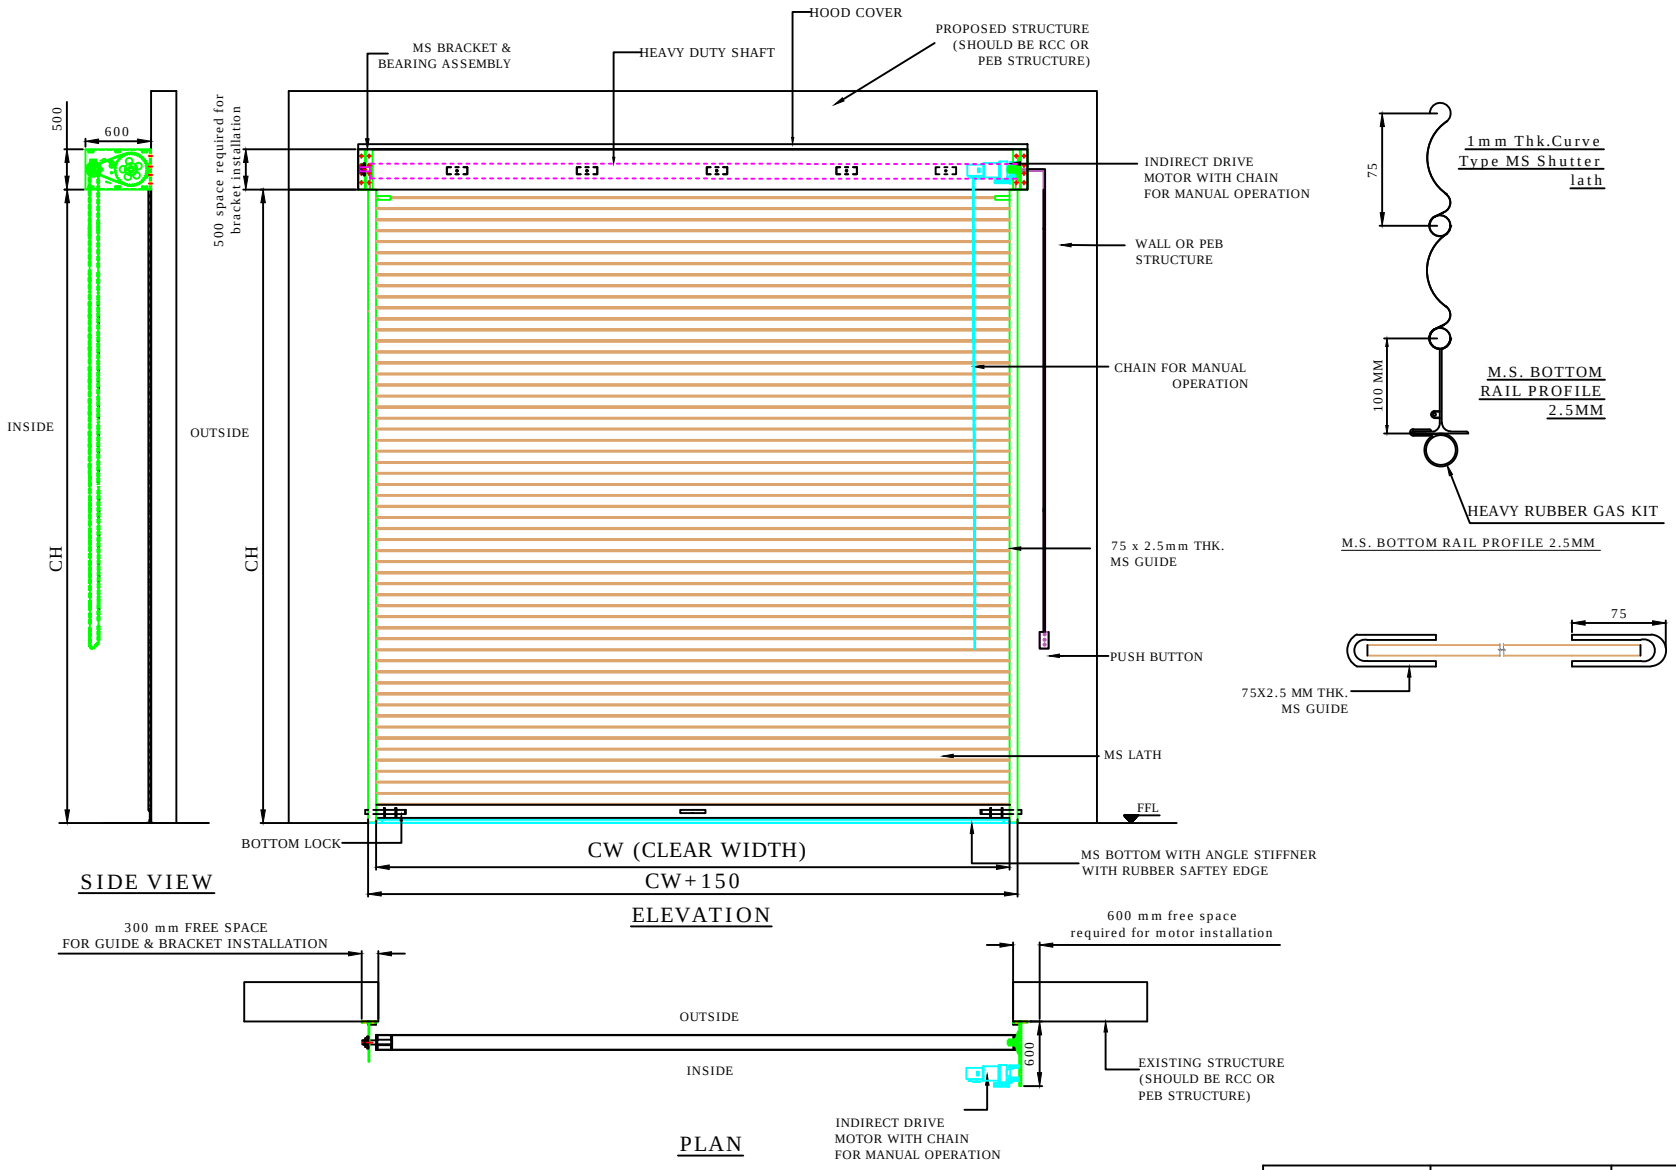


REVISION 1- CHAIN HEIGHT IS MENTIONED AS 1200mm FROM GROUND.

CLEAR WIDTH	CLEAR HEIGHT	QUANTITY
2500 mm	2500 mm	01 NOS.

DIMENSION :

CLEAR WIDTH	CLEAR HEIGHT	QUANTITY
2500 mm	2500 mm	01 NOS.

MATERIAL :

THICKNESS :

NOTE:
1.REQUIRED STRUCTURE FOR ROLLING SHUTTER WILL BE CLIENT'S SCOPE.
2.ONE COAT OF RED OXIDE PRIMER WILL BE GIVEN TO THE SHUTTER.
3.SINGLE PHASE. 3 CORE 1.5 SQ. CABLE REQUIRE AT SITE(CLIENT'S SCOPE)
4.FOR FINAL FINISH CLIENT SHOULD MENTION COLOR SHADE FOR ROLLING SHUTTER.

NIHVA TECHNOLOGIES PVT. LTD.
NIHVA TECHNOLOGY PVT. LTD. PUNE
Email:- info@nihva.com
Website:- www.nihva.com

TITLE:

MOTORIZED ROLLING SHUTTER

CLIENT'S APPROVAL :

CLIENT - INGERSOLL-RAND (INDIA)LTD.

PROJECT -

SITE LOCATION -AHMEDABAD

DWG. NO. : NIHVA/16-17/128/R01

SCALE: NTS	WT:	SHEET:1 OF 1

DRAWN BY: SURAJ	DATE: 21-01-2017
CHECK : OMKAR	DATE: 21-01-2017
APPROVED BY : R.K	DATE: 21-01-2017

If any queries contact : projects@nihva.com

NOTE: ALL DIMENSION ARE IN mm

THIS DRAWING & DESIGNING IS THE PROPERTY OF NIHVA TECHNOLOGIES. NOT BE SOLD OR COPY TO ANY OTHER CONCERN.