

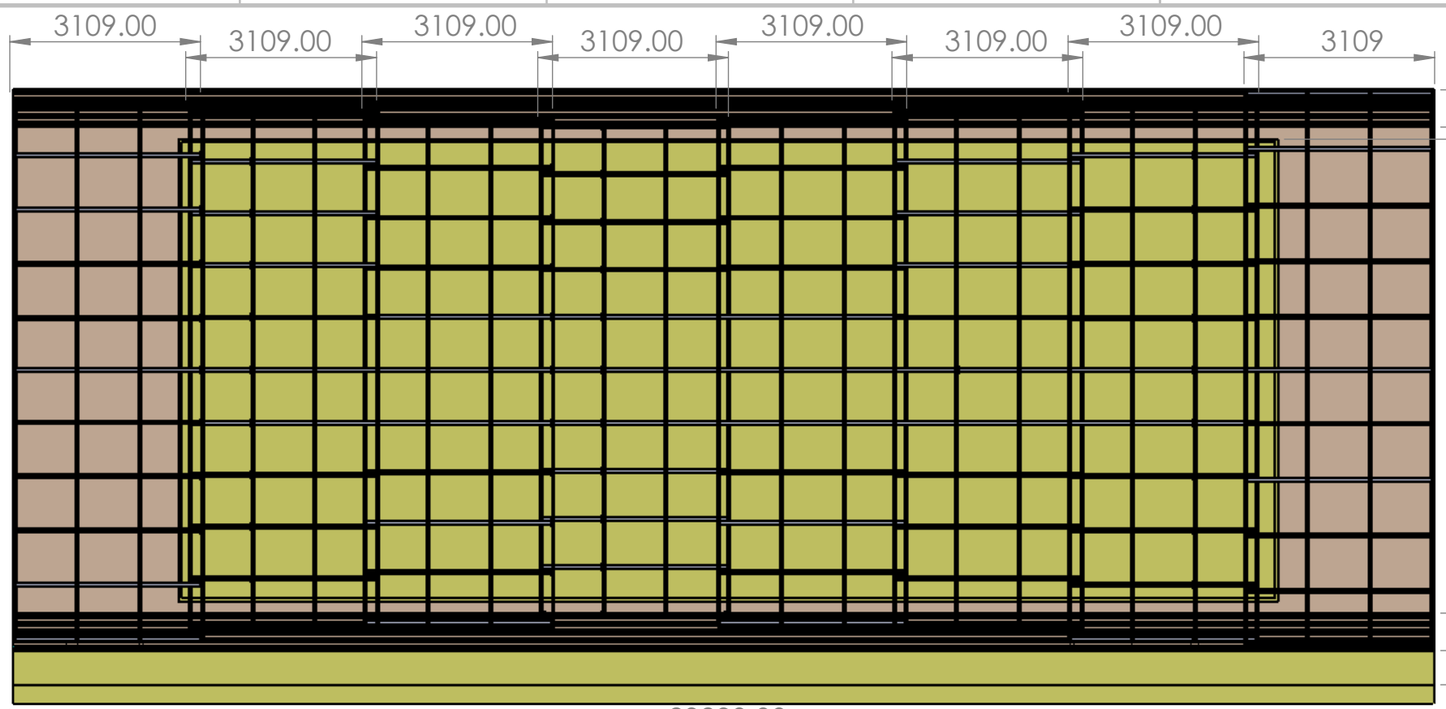


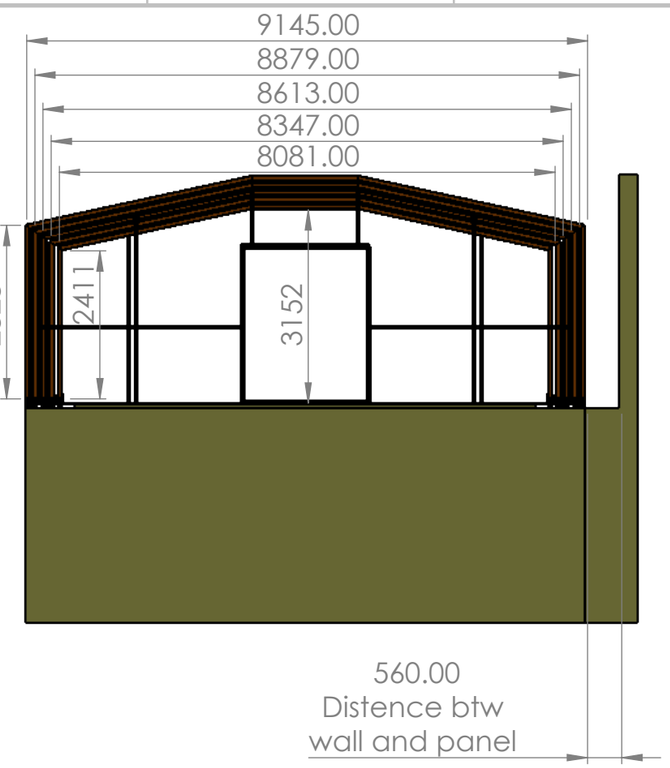

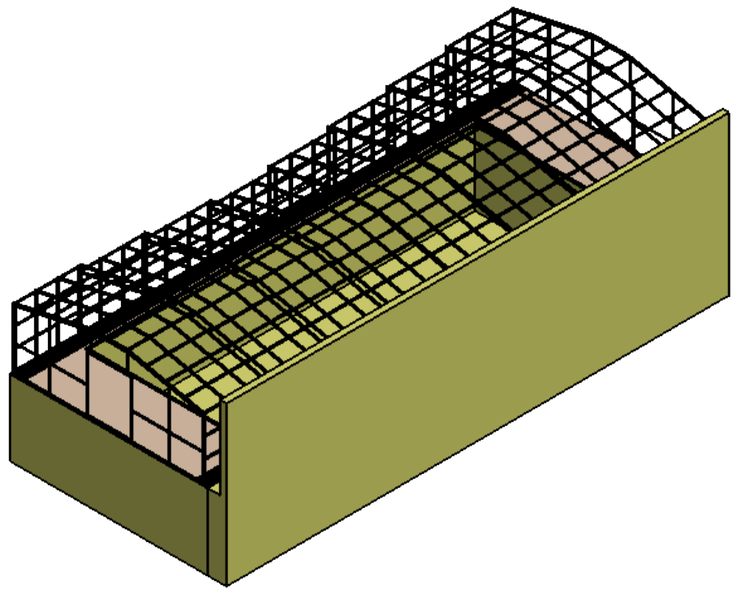

TITLE - TANKING PIT				NIHVA TECHNOLOGIES PVT.LTD.PUNE
DWG NO - GA			QTY - 1	Website - www.nihva.com
	NAME	SIGNATURE	DATE	PROJECT NO - NTPL-244-PM
DRAWN	S.W.		25.09.2024	PRODUCT - TANKING PIT
CHK'D	P.M.		25.09.2024	SITE LOCATION - Gujrat
APPV'D	V.T.		25.09.2024	
if any queries contact - supportautomation@nihva.com				REVISION -
ALL DIMENSION ARE IN mm			A3	SCALE - SHEET 1 OF 1