SR NO	DESCRIPTION	SPECIFICATION	QTY
1	SQ. TUBE	50 X 50 X 3 THK X 945L	8 NOS
2	SQ. TUBE	38 X 38 X 4 THK X 350L	2 NOS
3	PROFILE	450 X 10 X 550L	1 NO
4	FLAT	100 X 10 X 100L	8 NOS
5	FLAT	50 X 10 X 550L	1 NO
6	FLAT	50 X 10 X 550L	1 NO

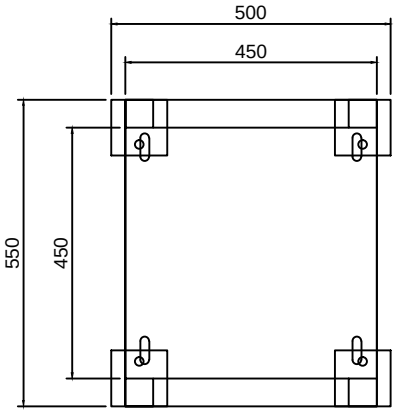

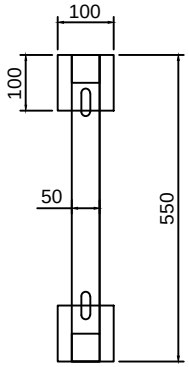

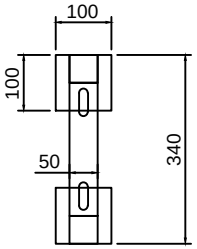

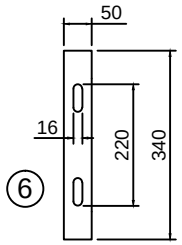

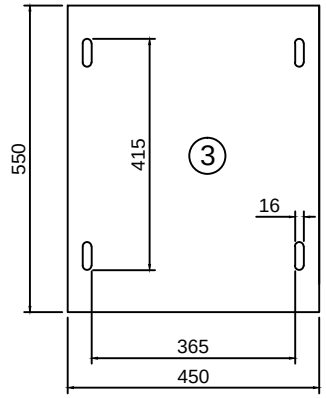

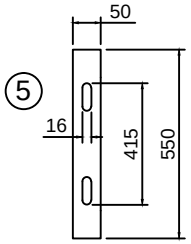

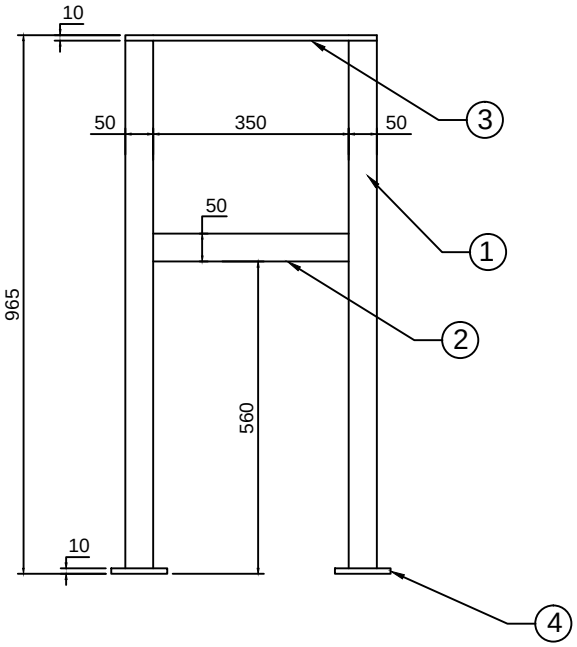

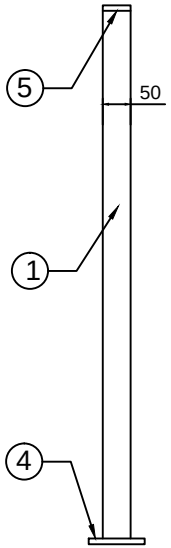

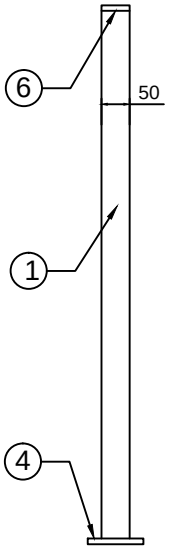

This drawing & designing is the property of NIHVA TECHNOLOGIES. Not to be sold or copied to any other concern.

TITLE

POST DETAILS

NIHVA TECHNOLOGIES
PVT. LTD. PUNE
Tel : 020 66304033
Email:- info@nihva.com
Website:- www.nihva.com

	NAME	SIGN	DATE
DRAWN	P.A		10.12.19
CHECKED	G.J		10.12.19
APPROVED			

CLIENT -

PROJECT -

SITE LOCATION -

DWG. NO. : NIHVA/19-20/VDR/240 REV: R00

If any queries contact : projects@nihva.com

SCALE: NTS WT: SHEET: 01 OF 01

ALL DIMENSION ARE IN mm