SR NO	NAME	DECRIPTION	LENGTH	QTY
1	CURVE PROF1	GNTOO6	5500 MM	1
2	CURVE PROF 2	GNTOO6	2154 MM	1
3	BTM PROF1	GNTOO6	5500 MM	1
4	BTM PROF2	GNTOO6	1761 MM	1
5	SIDE SUPPORT	GNTOO6	130 MM	2
6	MID PROFILE	GNTOO6	637 MM	1
7	SIDE PROFILE	GNTOO6	487 MM	2

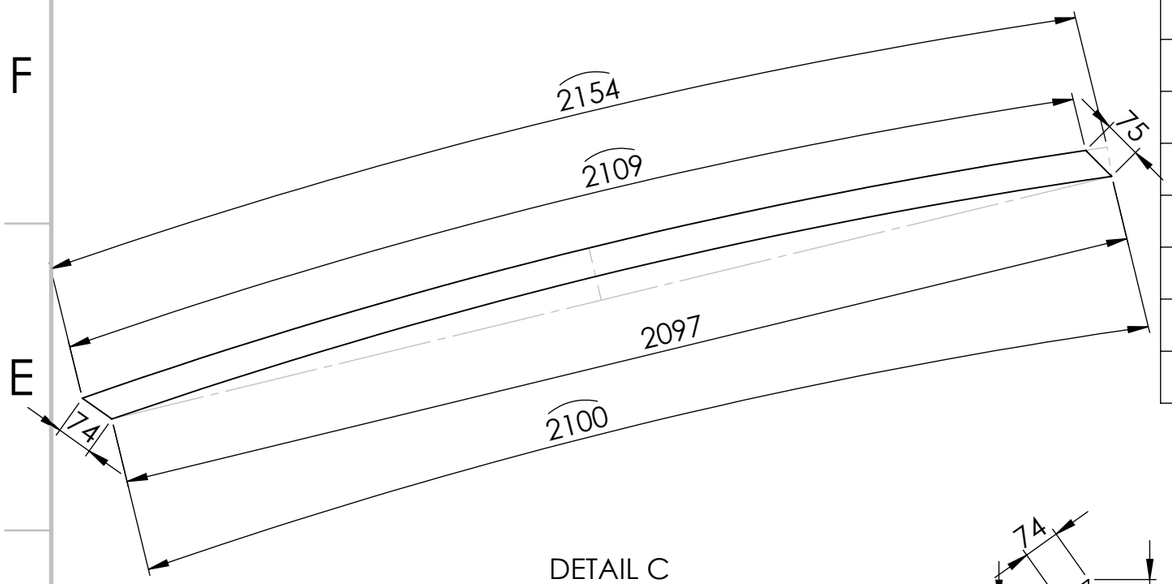

DETAIL C

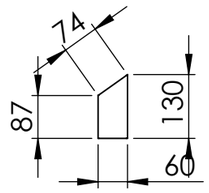

DETAIL B

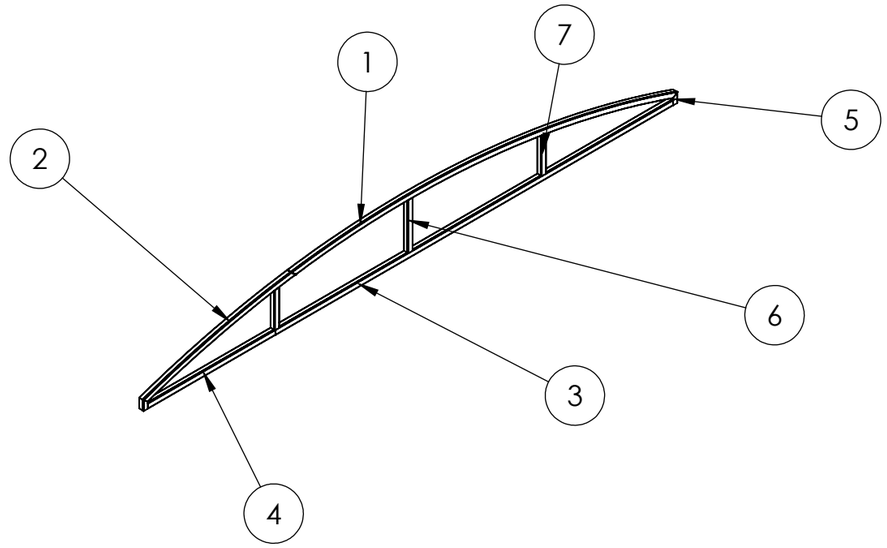

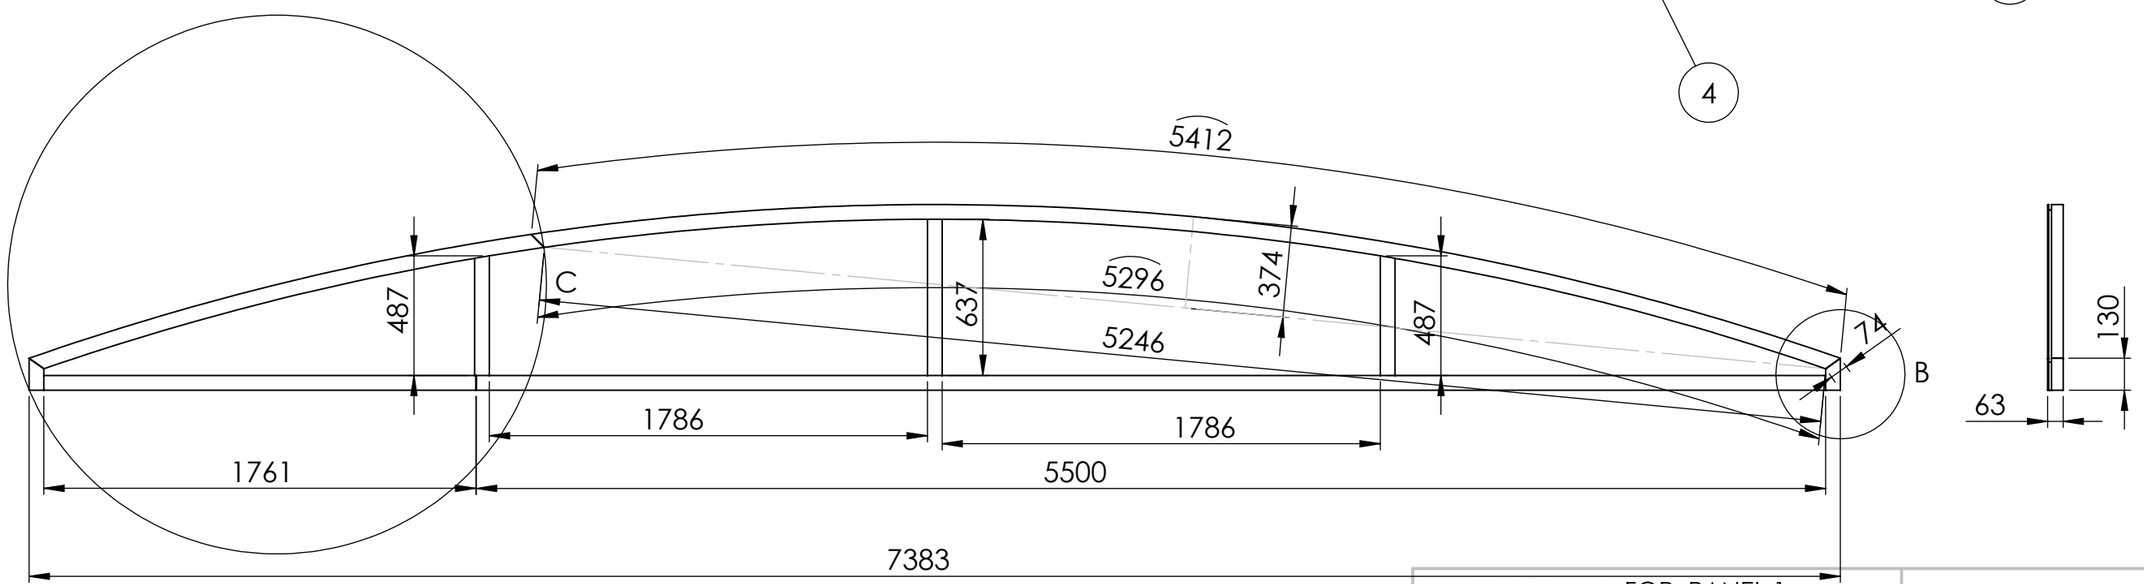

TITLE - ENCLOSURE FOR PANEL 1				NIHVA TECHNOLOGIES PVT.LTD.PUNE
DWG NO - NTPL163-ENCLOSUR			QTY - 2	Website - www.nihva.com
	NAME	SIGNATURE	DATE	PROJECT NO - NTPL 163
DRAWN	H.B.		08.06.2023	PRODUCT - RETRACTABLE ROOF
CHK'D	P.M.		08.06.2023	SITE LOCATION -
APPV'D	V.T.		08.06.2023	
if any queries contact - supportautomation@nihva.com				REVISION - 1
ALL DIMENSION ARE IN mm			A3	SCALE - SHEET 1 OF 1