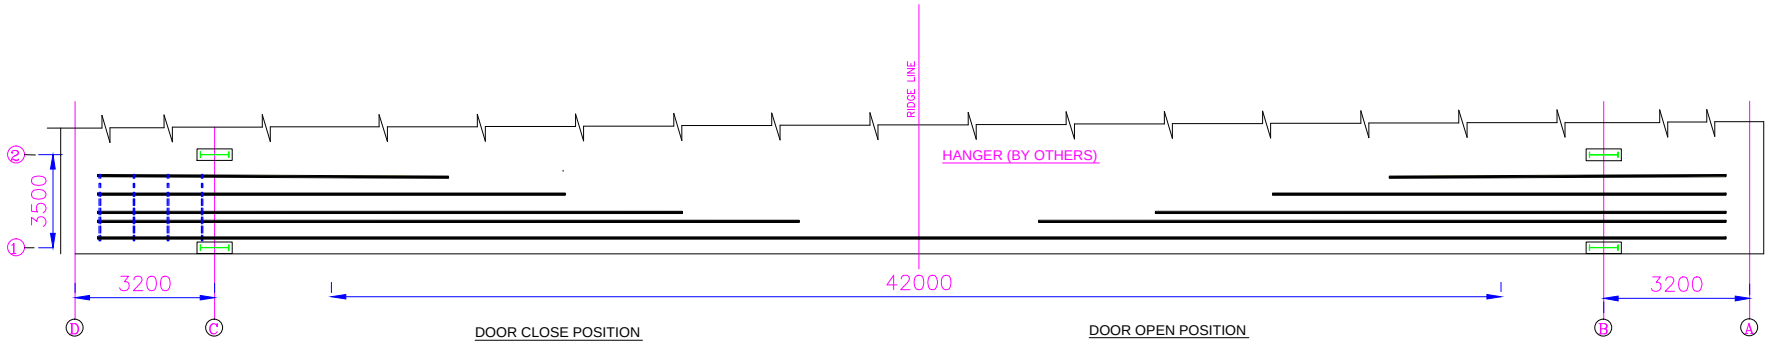

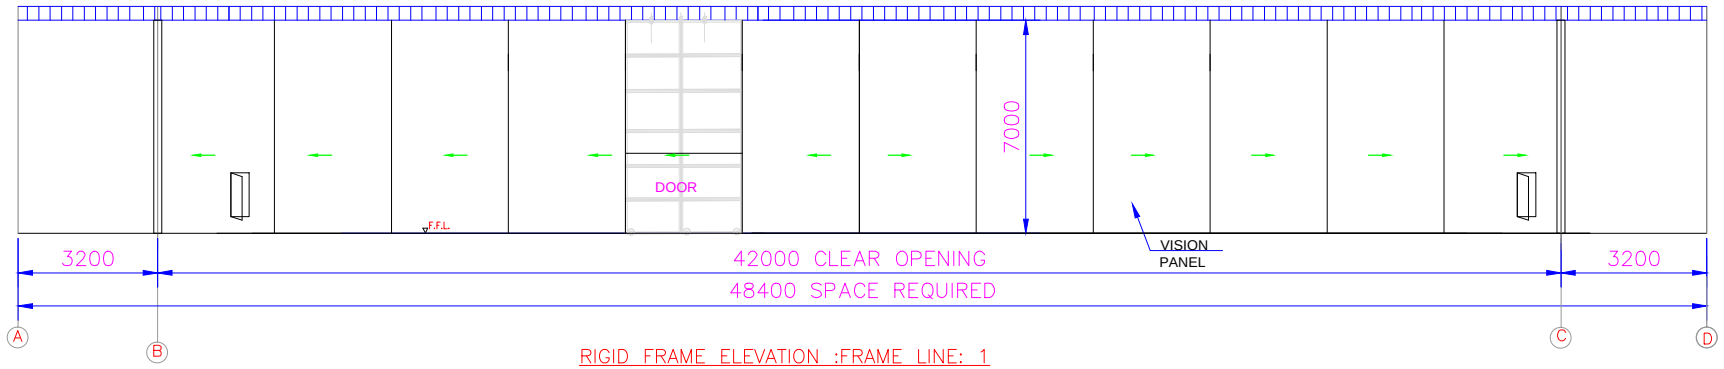

RIGID FRAME ELEVATION :FRAME LINE: 1

PANELS : 0.5 MM,TCT, WALL PANEL COLOR

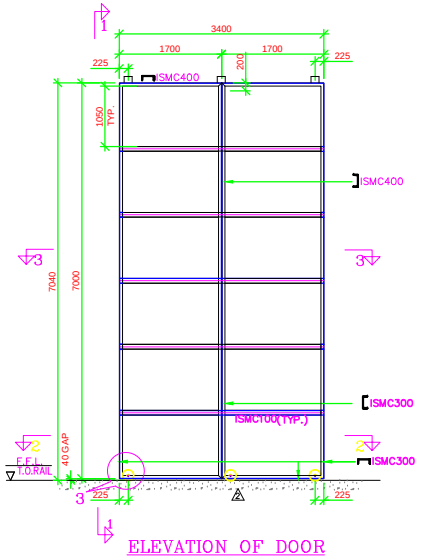

ELEVATION OF DOOR

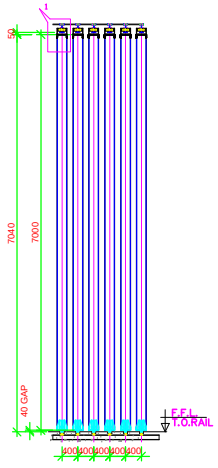

VIEW– 1–1

This drawing & design is the property of NIHVA TECHNOLOGIES. Not to be sold or copied to any other concern.

TITLE: SLIDING DOOR				NIHVA TECHNOLOGIES PVT. LTD. PUNE Tel : 020 66304033 Website:– www.nihva.com Email:– info@nihva.com	
	NAME	SIGN	DATE		
DRAWN	P.A		22.03.19	CLIENT - SUNGROUP	
CHECK	V.T		22.03.19	PROJECT -	
APPRD.				SITE LOCATION - BHIWADI, RAJASTHAN	
If any queries contact : design@nihva.com				DWG. NO. : NIHVA/18-19/0306	REV- R00
ALL DIMENSION ARE IN mm				SCALE: NTS	WT: SHEET: 01 OF 01