

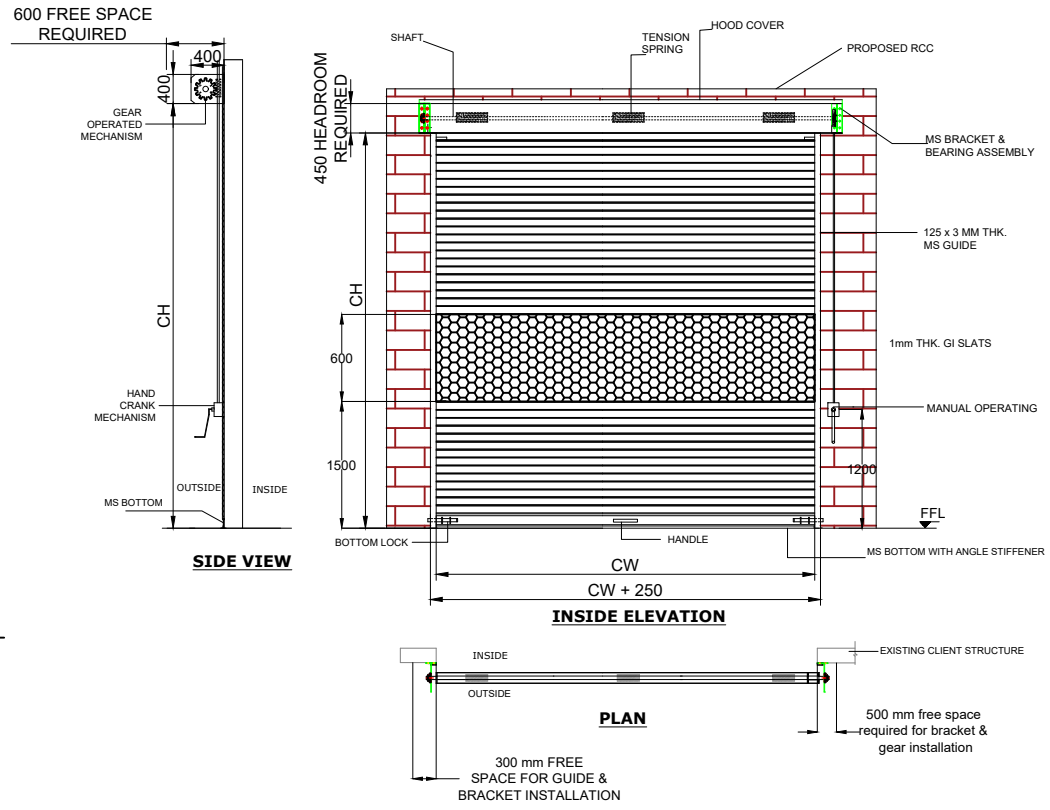


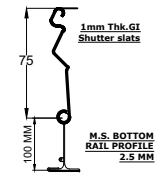

M.S. BOTTOM RAIL PROFILE 2.5MM

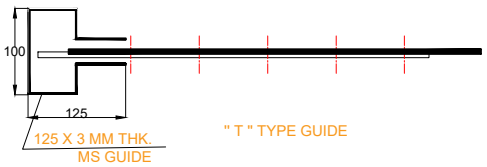

NOTE-
1. ALL CIVIL WORK WILL BE CLIENT'S SCOPE.
2.IF STRUCTURE REQUIRED FOR SHUTTER IS IN CLIENT'S SCOPE.

TECHNICAL SPECIFICATION:-

SR.	SPECIFICATION	DETAILS
1.	DESCRIPTION & DRIVE	GEAR OPERATED SHUTTER
2.	LOCATION AREA	OUTSIDE AREA
3.	MOUNTING SURFACE	SIDE BRACKETS: ON CONCRETE
4.	SLAT	75 MM WIDE - 1 MM THICK GI
5.	BOTTOM PROFILE	M.S. PLATE 100X2.5 MM THICK WITH ANGLE STIFFNER
6.	GUIDE PROFILE	M.S."T" SHAPE -100X125X3 MM THK .
7.	HOOD COVER & MOTOR COVER	MADE OF GI SHEET THICKNESS 0.9 MM.
8.	MATERIAL FINISH	SYNTHETIC ENAMEL PAINT

SR NO	(CW) CLEAR WIDTH	(CH) CLEAR HEIGHT	QUANTITY
1	3000	4100	03 NOS

This drawing & design is the property of NIHVA TECHNOLOGIES. Not to be sold or copied to any other concern.

TITLE: GEAR OPERATED ROLLING SHUTTER

	NAME	SIGN	DATE
DRAWN	B.S.		06.10.2025
CHECK	V.T.		06.10.2025
APPRD.	V.T.		06.10.2025

NIHVA TECHNOLOGIES PVT. LTD.
Website:- www.nihva.com
NIHVA TECHNOLOGIES PVT. LTD. PUNE
Tel : 020 66304033
Email:- info@nihva.com

CLIENT -
PROJECT -
SITE LOCATION -

If any queries contact : design@nihva.com
DWG. NO. : NIHVA/21-22/VDR/020
REV- R00
ALL DIMENSION ARE IN mm
SCALE: NTS
WT:
SHEET: 01 OF 01