

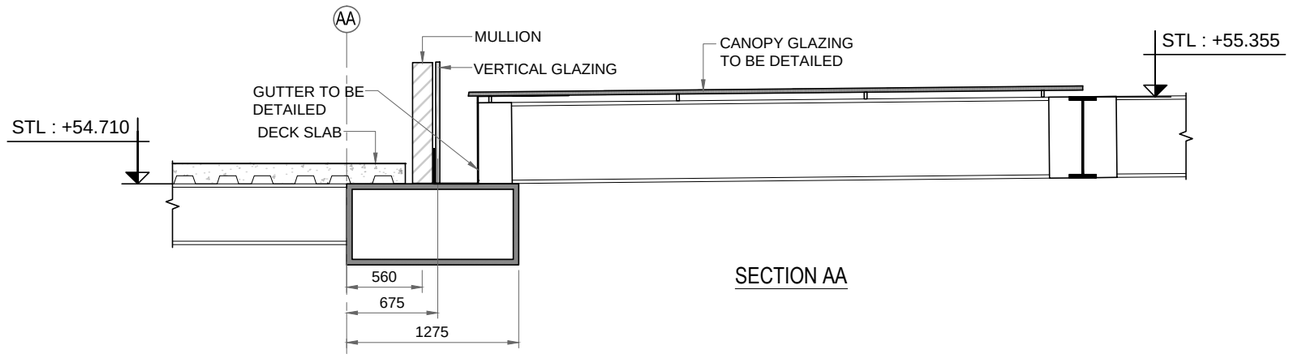


SECTION AA

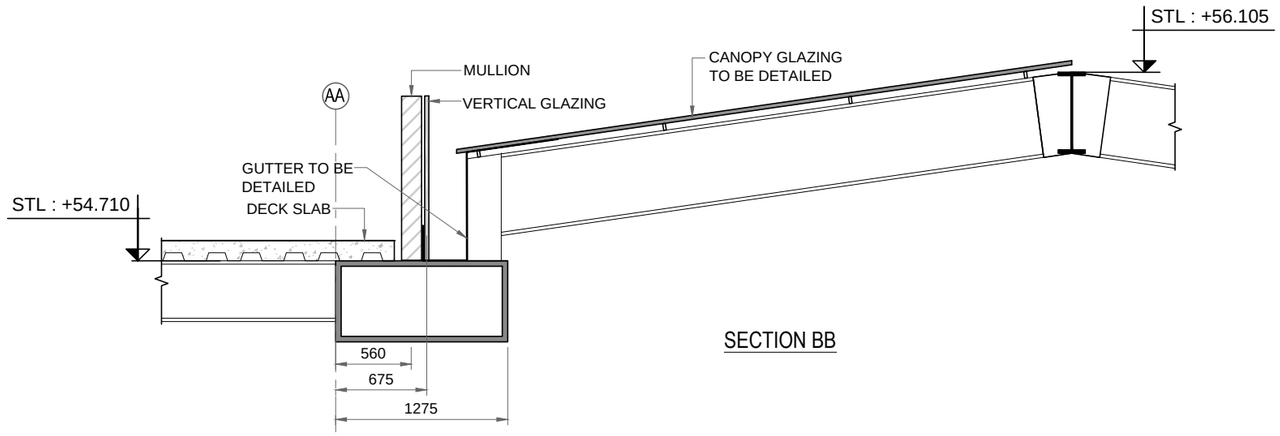


SECTION BB

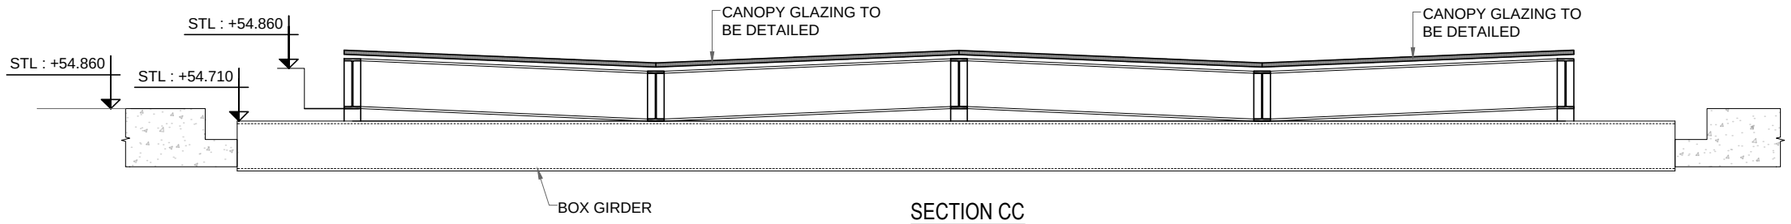

SECTION CC

NOTES:
1. ALL DIMENSIONS ARE IN mm & UNLESS OTHERWISE MENTIONED.
2. GRADE OF STEEL IS E350.

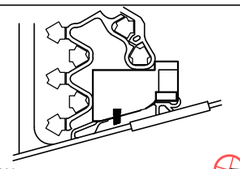

KEY PLAN
SCALE : NTS

REVISIONS

REV NO	DESCRIPTION	DATE
R0	FOR APPROVAL	15/02/2023

CLIENT
OBEROI REALTY

STRUCTURAL AND MEP CONSULTANT
WME
T +971 4 368 1616
E info@wmeglobal.com
W www.wmeglobal.com
Dubai | Abu Dhabi | London | Bangalore | Mumbai | Singapore

CONSULTANTS
BENOY
E: asiapacific@benoy.com
T: +852 2250 7222
www.benoy.com

PROJECT
Borivali Mixed Use
Borivali East, Mumbai, India

DRAWING TITLE
CANOPY LAYOUT & SECTION DETAILS

■ G.A ☐ ASSEMBLY ☐ SUB ASSLY ☐ COMPONENT

GOOD FOR CONSTRUCTION

DRAWN BY: GRK	DATE: 15/02/2023
DESIGNED BY: AK	DATE: 15/02/2023
CHECKED BY: GRK	DATE: 15/02/2023
APPROVED BY: SA	SCALE: 1:30 & 1:65

FILE NAME: G/3180/S/03-1139

DRAWING NUMBER: G / 3180 / S / 03 -1139
REV 0

These drawings are under copyright and are the property of Geodesic Techniques Pvt. Ltd. None of the drawings and related documents can be reproduced, copied in whole or in part whithout prior expressed written consent of Geodesic Techniques Pvt. Ltd. These drawings cannot be handed over to a third party or used for any purpose, other than that for which it has been loaned.

GEODESIC TECHNIQUES
Geodesic Techniques Pvt. Ltd.
N4, 4th Cross, 1st Stage, Peenya Industrial Area,
Bangalore, Karnataka – 560 058. INDIA
Tel: +91 80 6745 1200
Fax: +91 80 6745 1210
Email: enquiry@geodesictechniques.com