


DRAWING

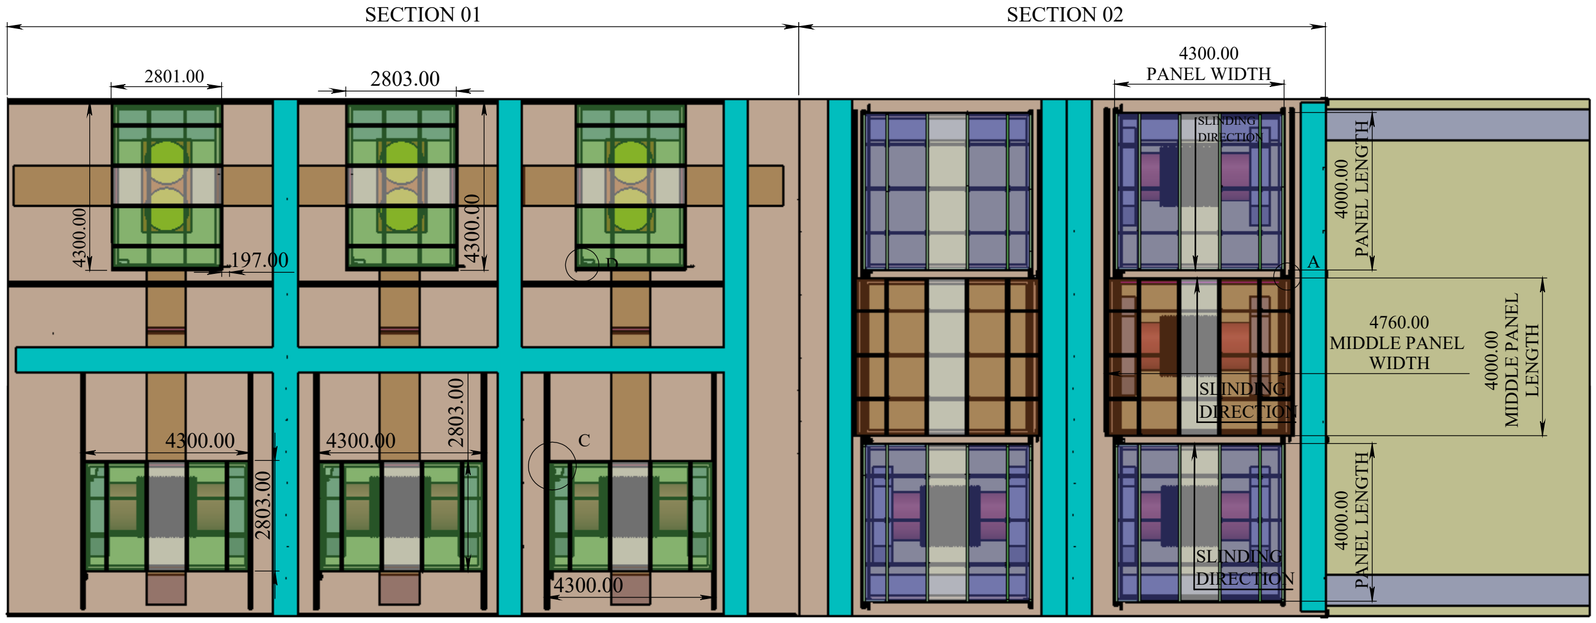


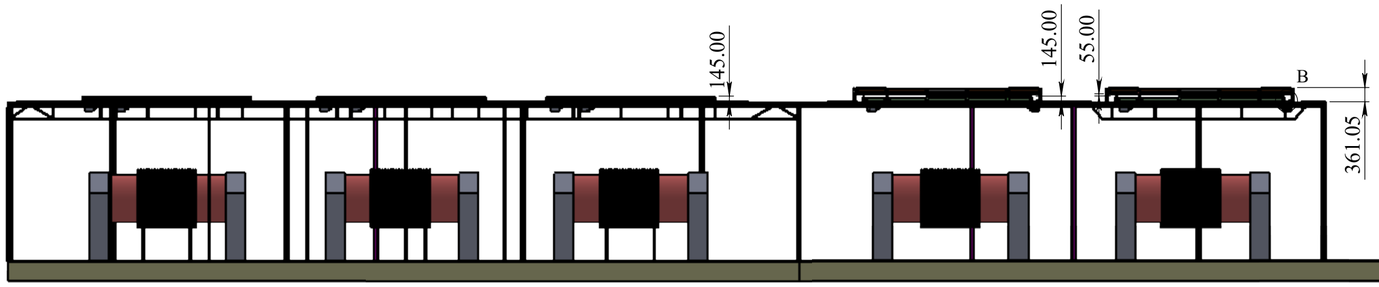

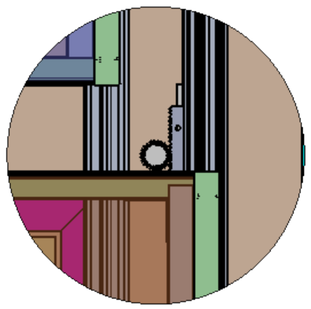


DETAIL A
SCALE 1 : 10

MIDDLE PANEL
MOTOR POSITION

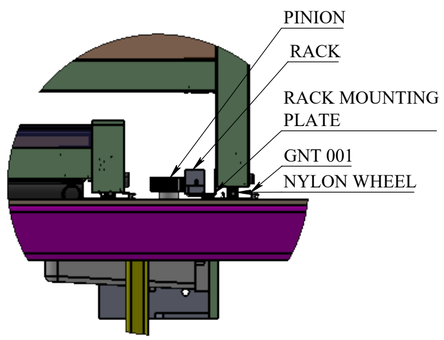


DETAIL B
SCALE 1 : 8

MOTOR MOUNTING
MIDDLE PANEL

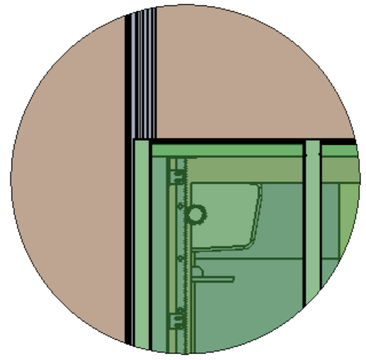

DETAIL C
SCALE 1 : 15

SECTION 01
HORIZONTAL PANEL
MOTOR MOUNTING

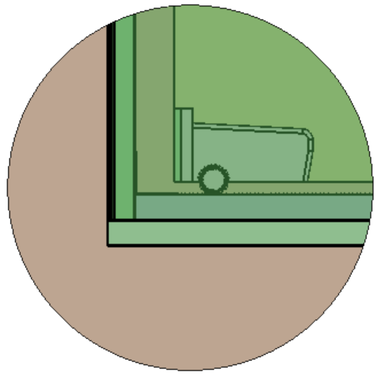

DETAIL D
SCALE 1 : 10

SECTION 02
VERTICAL PANEL
MOTOR MOUNTING

REV DESCRIPTION	DATE	REV NO
03. AIR TIGHTENING & DUST PROOF RUBBER IS ADDED	00-00-2025	REV 03
04. PANEL MODIFICATION	10-07-2025	REV 04
05. SAME UNIT ANTHOER THREE PANEL MODIFICATION	15-07-2025	REV 05
06. MIDDLE PANEL MOTOR POSITION CHANGE	24-07-2025	REV 06

NOTE :

SPECIAL INSTRUCTION'S :

TITLE - ROOF AUTOMATION

DWG NO - NTPL-244-PM-001-00-00-00


NIHVA TECHNOLOGIES PVT.LTD.PUNE
Website - www.nihva.com


	NAME	SIGNATURE	DATE
DRAWN	V.W.		26-07-2025
CHK'D	S.P.		28-07-2025
APPV'D	V.T.		28-07-2025


PRODUCT - RETRACTABLE ROOF
PROJECT NO - NTPL-244-PM
REVISION - 06
SITE LOCATION - AHMEDABAD
WEIGHT -
MATRIAL -
QTY - 1
SCALE :
SHEET 1 OF 11

If any queries contact - design.nihva@gmail.com
ALL DIMENSION ARE IN mm
A2
PROJECTION METHOD:


DRAWING

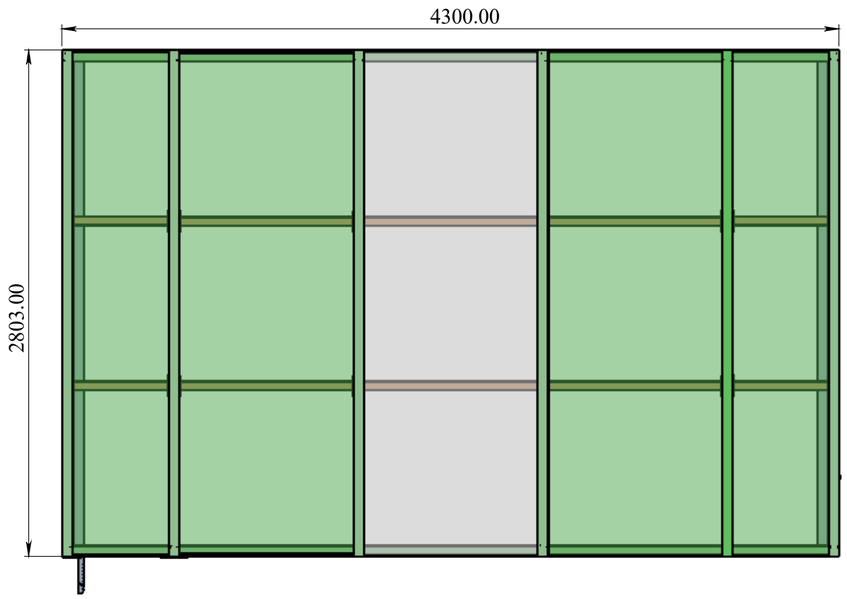

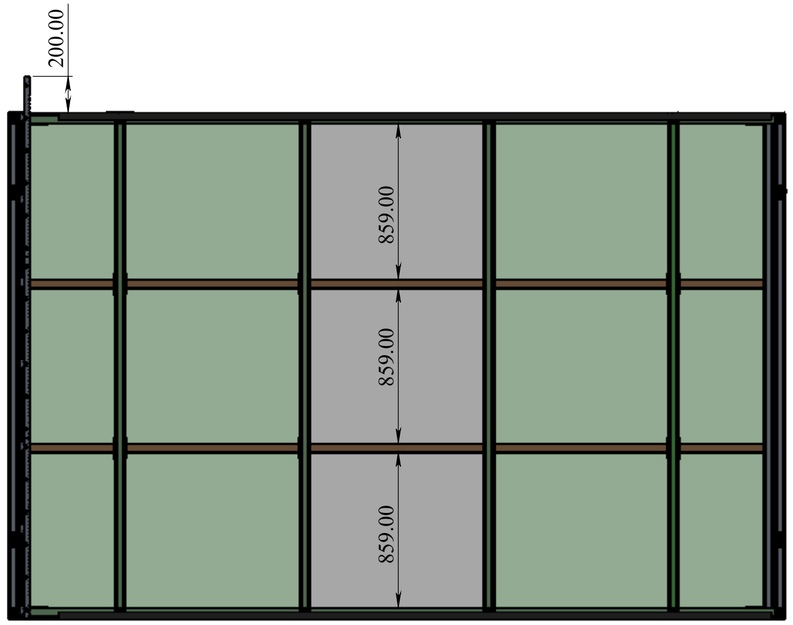


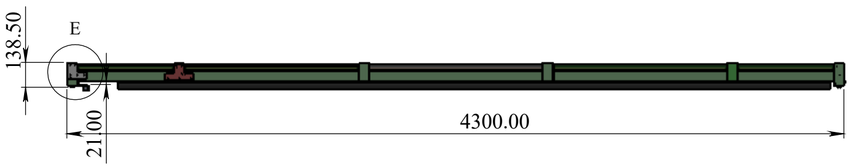


ITEM NO.	PART NUMBER	DESCRIPTION	QTY.
1	.rev0202paneel modify-03.		1
2	.Rev_02_panel modifiy-03 intermediate support assembly.		6
3	.Rev_02_SS WHEEL.	SS WHEEL ∅65X18	4
4	NP-PROF01	MS50X50X4T	2
5	NP-PROF01	MS50X50X4T	2
6	.Rev_02_panel modifiy-02 intermediate support assembly.		4
7	T PLATE	156X91X3 MM THK	1
8	L PLATE	91X106X3 MM THK	1
9	.Rev_02_AL INSIDE CORNER WELD PLATE.	196X40X3 MM THK	4
10	C-MSBL12-35.SLDASM	SHOULDER BOLT	1
11	RACK SUPPORT PLATE.		7
12	.Rev_02_RACK..		3

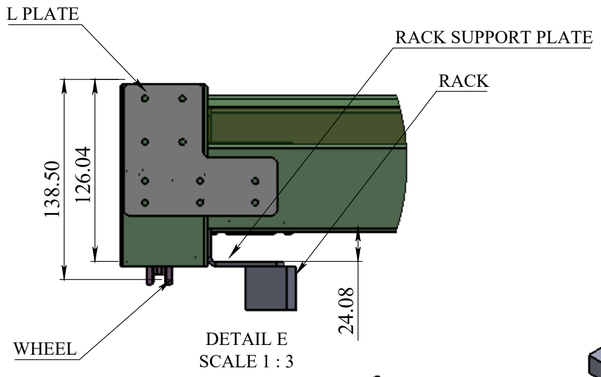

DETAIL E
SCALE 1 : 3

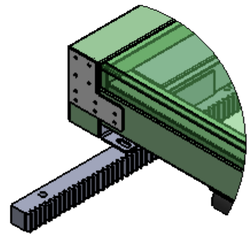

DETAIL F
SCALE 1 : 6

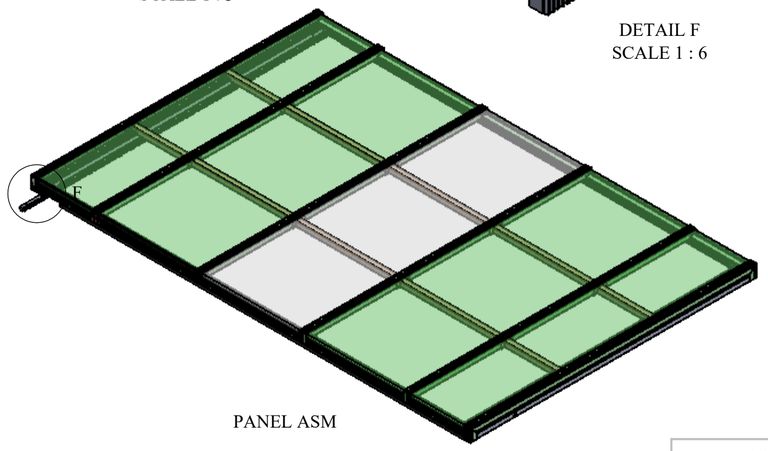

PANEL ASM

REV DESCRIPTION	DATE	REV NO
	26-07-2025	REV 04
1.		

NOTE :

SECTION NO 1 PANEL ASM
QTY - 06 No'S.

SPECIAL INSTRUCTION'S :

TITLE - ROOF AUTOMATION

DWG NO - NTPL-244-PM-001-00-00-00

NIHVA TECHNOLOGIES PVT.LTD.PUNE
Website - www.nihva.com


	NAME	SIGNATURE	DATE
DRAWN	V.W.		26-07-2025
CHK'D	S.P.		28-07-2025
APPV'D	V.T.		28-07-2025


PRODUCT - RETRACTABLE ROOF
PROJECT NO - NTPL-244-PM | REVISION - 04
SITE LOCATION - AHMEDABAD | WEIGHT -
MATRIAL - | QTY - 01
If any queries contact - design.nihva@gmail.com
PROJECTION METHOD: | SCALE :
ALL DIMENSION ARE IN mm | A2
SHEET 2 OF 11

DRAWING


ITEM NO.	PART NUMBER	DESCRIPTION	QTY.
1	OPEN POSITINING.rev0202panel modify-03.		6


REV DESCRIPTION	DATE	REV NO
	26-07-2025	REV 04
1.		

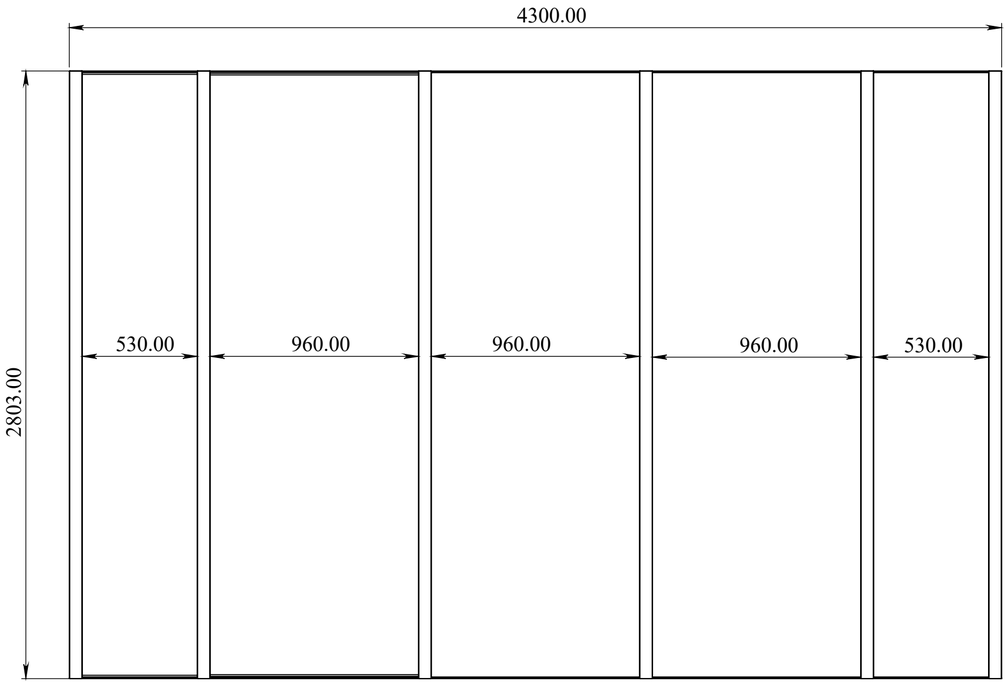


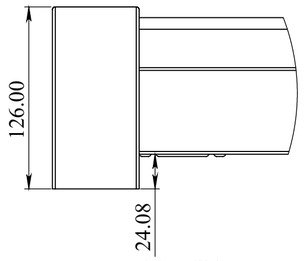

DETAIL F
SCALE 1 : 3

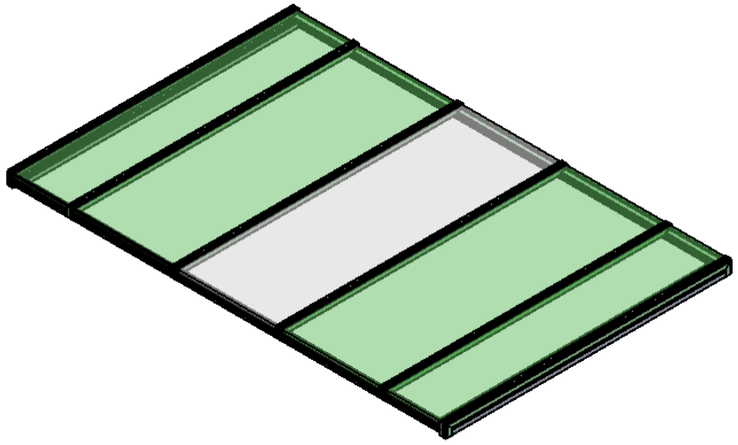

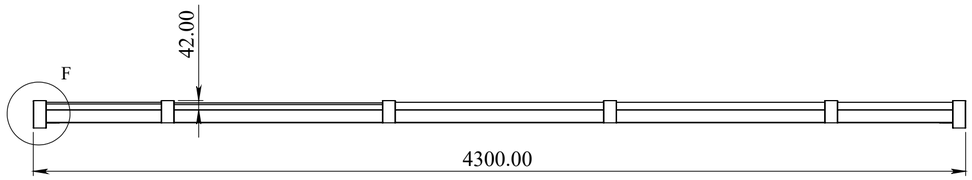

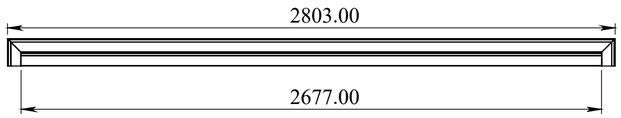

NOTE :

SECTION NO 01 PANEL
ALL PROFILE IN AL GNT-006
QTY - 6 No'S.

SPECIAL INSTRUCTION'S :

ALL PROFILE IN GNT-006

TITLE - ROOF AUTOMATION

DWG NO - NTPL-244-PM-001-00-00-00

NIHVA TECHNOLOGIES PVT.LTD.PUNE
Website - www.nihva.com

	NAME	SIGNATURE	DATE
DRAWN	V.W.		26-07-2025
CHK'D	S.P.		28-07-2025
APPV'D	V.T.		28-07-2025


PRODUCT - RETRACTABLE ROOF
PROJECT NO - NTPL-244-PM
REVISION - 04
SITE LOCATION - AHMEDABAD
WEIGHT -
MATRIAL -
QTY - 01
SCALE :
PROJECTION METHOD:


If any queries contact - design.nihva@gmail.com
ALL DIMENSION ARE IN mm
A2


DRAWING

REV DESCRIPTION	DATE	REV NO
	26-07-2025	REV 04
1.		

ITEM NO.	PART NUMBER	DESCRIPTION	QTY.
1	INTERMEDIATE SUPPORT TUBE - 960 MM L	SQ - 50X50X2 THK	06

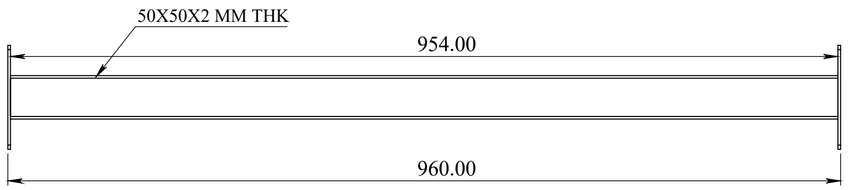

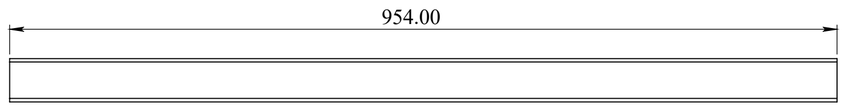

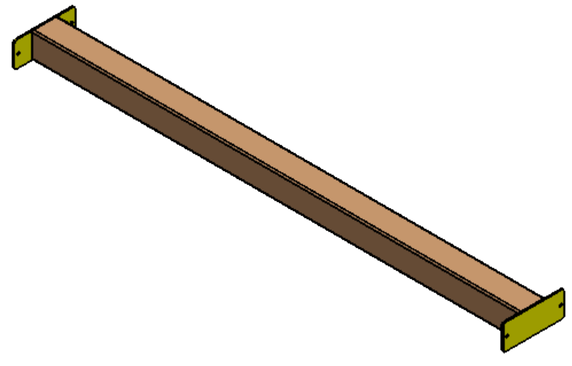

NOTE :

INTERMEDIATE SUPPORT TUBE - 50X50X2 MM THK - 960 MM L
ONE PANEL REQ QTY - 06 No'S
TOTAL REQ QTY - 36 No'S
MTL - AL

SPECIAL INSTRUCTION'S :

TITLE - ROOF AUTOMATION

DWG NO - NTPL-244-PM-001-00-00-00


NIHVA TECHNOLOGIES PVT.LTD.PUNE
Website - www.nihva.com


	NAME	SIGNATURE	DATE
DRAWN	V.W.		26-07-2025
CHK'D	S.P.		28-07-2025
APPV'D	V.T.		28-07-2025


PRODUCT - RETRACTABLE ROOF
PROJECT NO - NTPL-244-PM | REVISION - 04
SITE LOCATION - AHMEDABAD | WEIGHT -
MATRIAL - | QTY - 01
If any queries contact - design.nihva@gmail.com | PROJECTION METHOD: | SCALE :
ALL DIMENSION ARE IN mm | A2

DRAWING

ITEM NO.	PART NUMBER	DESCRIPTION	QTY.
1	INTERMEDIATE SUPPORT TUBE - 530 MM L	REC - 50X50X2 THK	4

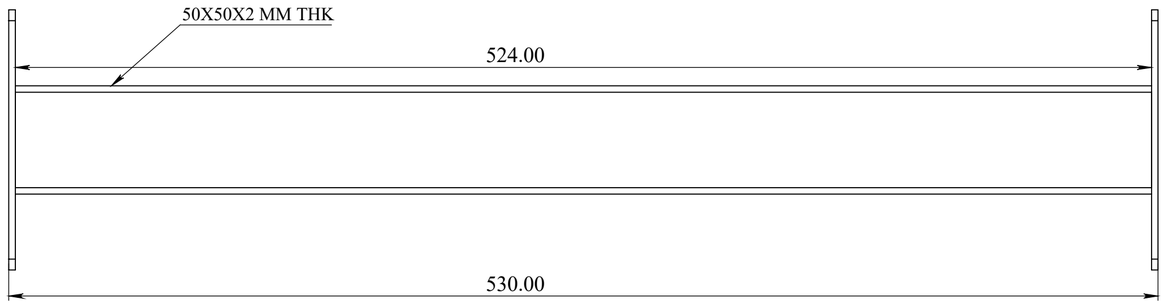

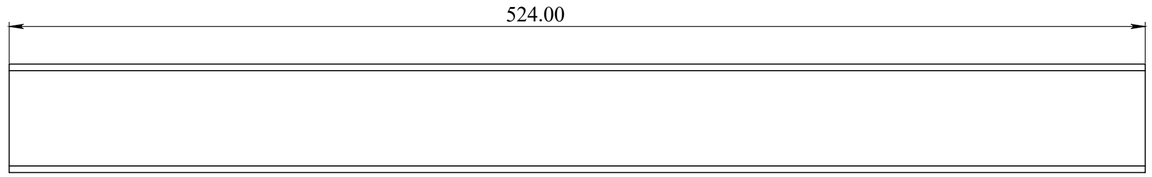

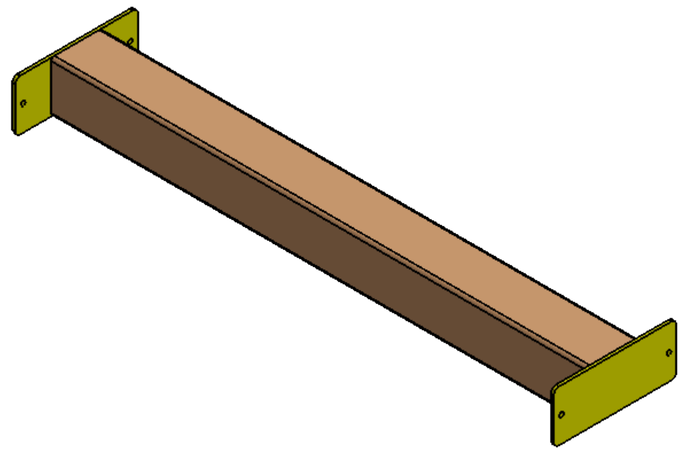

REV DESCRIPTION	DATE	REV NO
	26-07-2025	REV 04
1.		

NOTE :

INTERMEDIATE SUPPORT TUBE - 50X50X2 MM THK
ON'E PANEL REQ QTY - 04 No'S
TOTAL REQ QTY - 24 No'S
MTL - AL.

SPECIAL INSTRUCTION'S :

TITLE - ROOF AUTOMATION

DWG NO - NTPL-244-PM-001-00-00-00

NIHVA Technologies Pvt. Ltd.

NIHVA TECHNOLOGIES PVT.LTD.PUNE
Website - www.nihva.com


	NAME	SIGNATURE	DATE
DRAWN	V.W.		26-07-2025
CHK'D	S.P.		28-07-2025
APPV'D	V.T.		28-07-2025


PRODUCT - RETRACTABLE ROOF
PROJECT NO - NTPL-244-PM | REVISION - 04
SITE LOCATION - AHMEDABAD | WEIGHT -
MATRIAL - | QTY - 01
If any queries contact - design.nihva@gmail.com | PROJECTION METHOD: | SCALE :
ALL DIMENSION ARE IN mm | A2 | SHEET 5 OF 11


DRAWING

REV DESCRIPTION	DATE	REV NO
	26-07-2025	REV 04
1.		

ITEM NO.	PART NUMBER	DESCRIPTION	QTY.
1	NYLON WHEEL	NYLON WHEEL ∅65X18	04

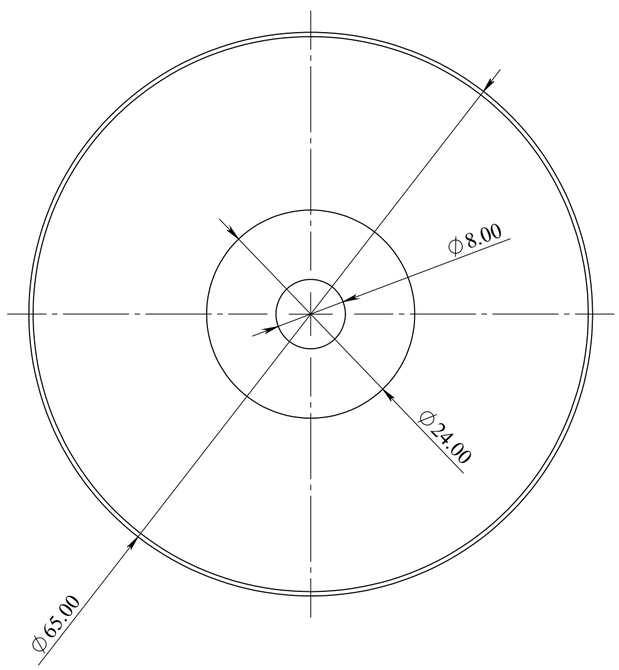

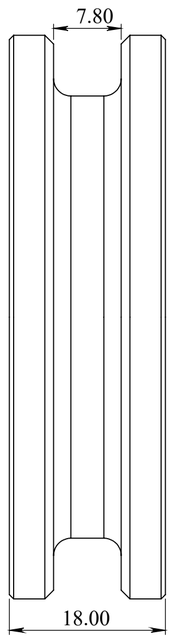

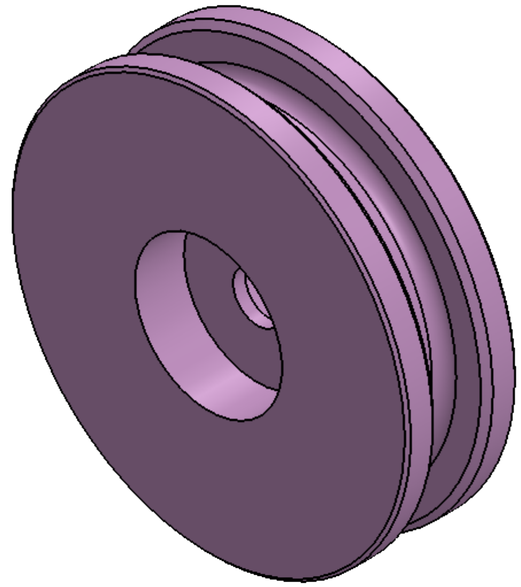

NOTE :

NYLON WHEEL - DIA 65X W 18 MM
ONE PANEL REQ QTY - 04 No'S.
TOTAL REQ QTY - 24 No'S

SPECIAL INSTRUCTION'S :

TITLE - ROOF AUTOMATION

DWG NO - NTPL-244-PM-001-00-00-00

NIHVA Technologies Pvt. Ltd.

NIHVA TECHNOLOGIES PVT.LTD.PUNE
Website - www.nihva.com

	NAME	SIGNATURE	DATE	PRODUCT - RETRACTABLE ROOF	
DRAWN	V.W.		26-07-2025	PROJECT NO - NTPL-244-PM	REVISION - 04
CHK'D	S.P.		28-07-2025	SITE LOCATION - AHMEDABAD	WEIGHT -
APPV'D	V.T.		28-07-2025	MATRIAL -	QTY - 01

If any queries contact - design.nihva@gmail.com

ALL DIMENSION ARE IN mm | A2


PROJECTION METHOD:


SCALE :

DRAWING

REV DESCRIPTION	DATE	REV NO
	26-07-2025	REV 04
1.		

ITEM NO.	PART NUMBER	DESCRIPTION	QTY.
1	L PLATE	91X106X3 MM THK	04

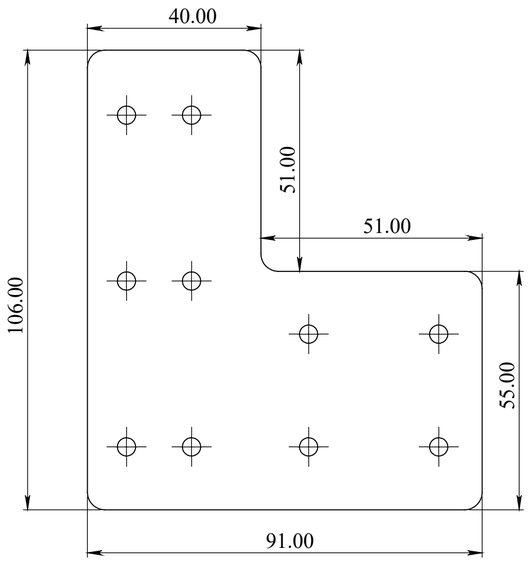

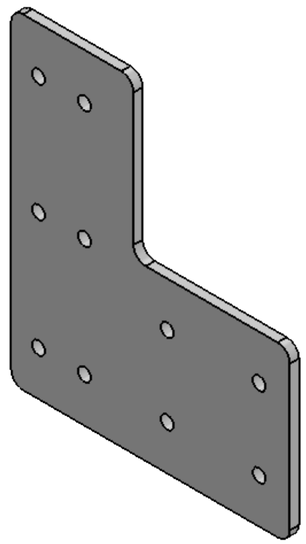

NOTE :

NAME - L PLATE
SIZE - 106X91X3 MM THK
THK - 3 MM
ONE PANEL REQ QTY - 4 No'S
TOTAL REQ QTY - 24 No'S
MTL - SS.

SPECIAL INSTRUCTION'S :

TITLE - ROOF AUTOMATION

DWG NO - NTPL-244-PM-001-00-00-00

NIHVA Technologies Pvt. Ltd.

NIHVA TECHNOLOGIES PVT.LTD.PUNE
Website - www.nihva.com

	NAME	SIGNATURE	DATE
DRAWN	V.W.		26-07-2025
CHK'D	S.P.		28-07-2025
APPV'D	V.T.		28-07-2025


PRODUCT - RETRACTABLE ROOF
PROJECT NO - NTPL-244-PM | REVISION - 04
SITE LOCATION - AHMEDABAD | WEIGHT -
MATRIAL - | QTY - 01


If any queries contact - design.nihva@gmail.com
ALL DIMENSION ARE IN mm | A2
PROJECTION METHOD:
SCALE :
SHEET 7 OF 11

DRAWING

REV DESCRIPTION	DATE	REV NO
	26-07-2025	REV 04
1.		

ITEM NO.	PART NUMBER	DESCRIPTION	QTY.
1	L ANGLE PLATE	17X52X3 MM THK	08

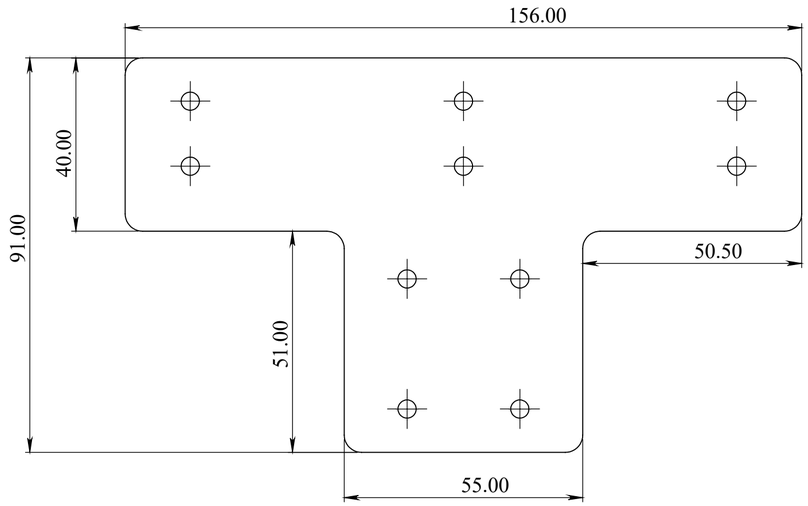

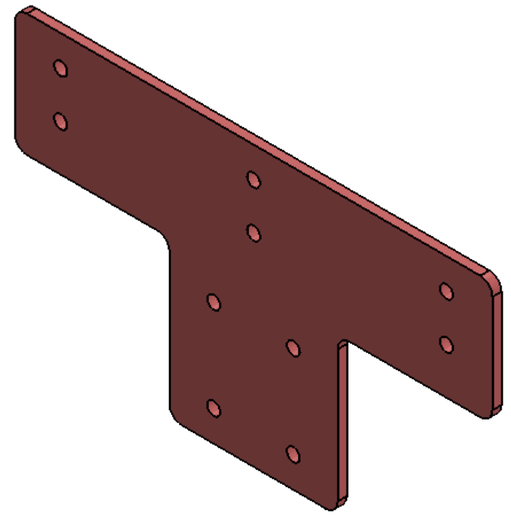

NOTE :

NAME - T PLATE
SIZE - 156X91X3 MM THK
THK - 3 MM
MTL - SS
ONE PANEL REQ QTY - 08 No'S
TOTAL REQ QTY - 48 No'S.

SPECIAL INSTRUCTION'S :

TITLE - ROOF AUTOMATION

DWG NO - NTPL-244-PM-001-00-00-00

NIHVA Technologies Pvt. Ltd.

NIHVA TECHNOLOGIES PVT.LTD.PUNE
Website - www.nihva.com


	NAME	SIGNATURE	DATE
DRAWN	V.W.		26-07-2025
CHK'D	S.P.		28-07-2025
APPV'D	V.T.		28-07-2025


PRODUCT - RETRACTABLE ROOF
PROJECT NO - NTPL-244-PM | REVISION - 04
SITE LOCATION - AHMEDABAD | WEIGHT -
MATRIAL - | QTY - 01
If any queries contact - design.nihva@gmail.com
PROJECTION METHOD:
ALL DIMENSION ARE IN mm | A2
SCALE :


DRAWING

ITEM NO.	PART NUMBER	DESCRIPTION	QTY.
1	.Rev_02_AL INSIDE CORNER WELD PLATE.	196X40X3 MM THK	04

REV DESCRIPTION	DATE	REV NO
	26-07-2025	REV 04
1.		

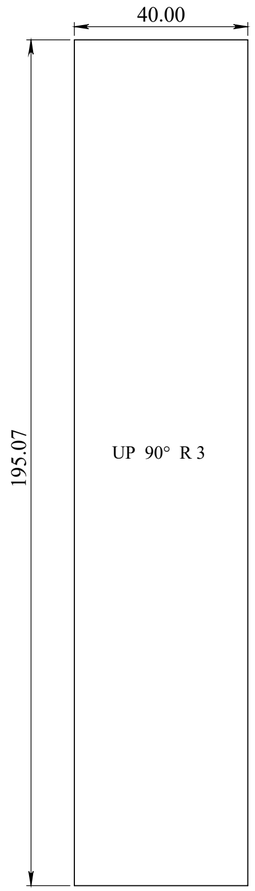

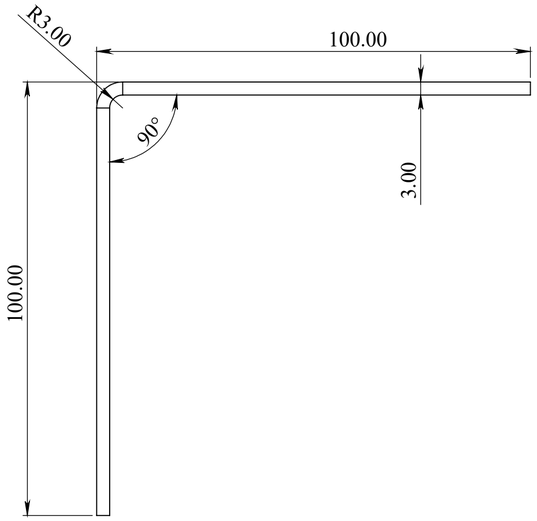

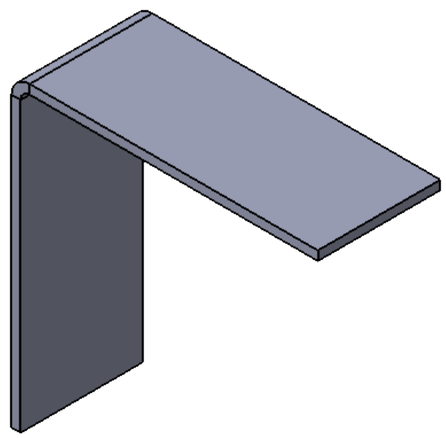

NOTE :

NAME - L ANGLE CORNER WELDING PLATE
SIZE - 195.07X40X3 MM THK
THK - 3 MM
MTL - AL
ONE PANEL REQ QTY - 04 No'S
TOTAL REQ QTY - 24 No'S.

SPECIAL INSTRUCTION'S :

TITLE - ROOF AUTOMATION

DWG NO - NTPL-244-PM-001-00-00-00

NIHVA TECHNOLOGIES PVT.LTD.PUNE
Website - www.nihva.com


	NAME	SIGNATURE	DATE
DRAWN	V.W.		26-07-2025
CHK'D	S.P.		28-07-2025
APPV'D	V.T.		28-07-2025


PRODUCT - RETRACTABLE ROOF
PROJECT NO - NTPL-244-PM | REVISION - 04
SITE LOCATION - AHMEDABAD | WEIGHT -
MATRIAL - | QTY - 01
If any queries contact - design.nihva@gmail.com
PROJECTION METHOD: | SCALE :
ALL DIMENSION ARE IN mm | A2


DRAWING


REV DESCRIPTION	DATE	REV NO
	24-07-2025	REV 06
1.		

ITEM NO.	PART NUMBER	DESCRIPTION	QTY.
1	RACK SUPPORT PLATE.		08

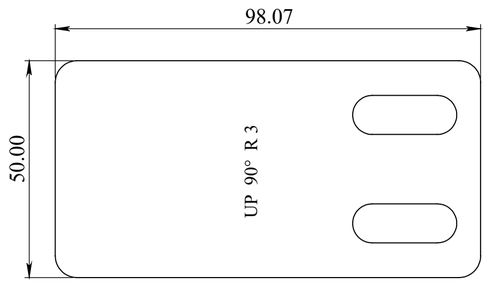

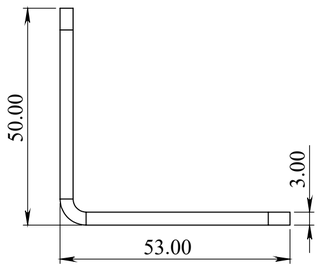

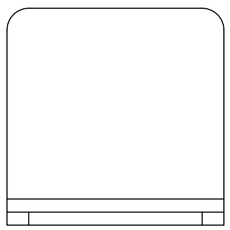

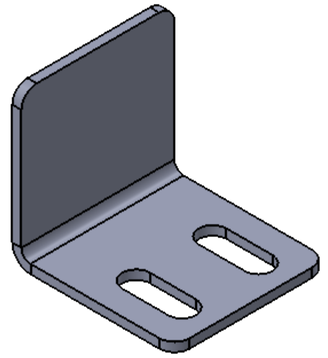

NOTE :

NAME - RACK SUPPORT PLATE
SIZE - 98.07X50X3 MM THK
THK - 3 MM
MTL - AL
ONE PANEL PANEL REQ QTY -8 No'S
TOTAL REQ QTY - 48 No'S.

SPECIAL INSTRUCTION'S :

TITLE - ROOF AUTOMATION

DWG NO - NTPL-244-PM-001-00-00-00

NIHVA Technologies Pvt. Ltd.

NIHVA TECHNOLOGIES PVT.LTD.PUNE
Website - www.nihva.com

	NAME	SIGNATURE	DATE
DRAWN	V.W.		24-07-2025
CHK'D	S.P.		25-07-2025
APPV'D	V.T.		25-07-2025


PRODUCT - RETRACTABLE ROOF
PROJECT NO - NTPL-244-PM | REVISION - 06
SITE LOCATION - AHMEDABAD | WEIGHT -
MATRIAL - | QTY - 1


If any queries contact - design.nihva@gmail.com
ALL DIMENSION ARE IN mm | A2
PROJECTION METHOD:
SCALE :
SHEET 10 OF 11

DRAWING

REV DESCRIPTION	DATE	REV NO
	26-07-2025	REV 04
1.		

ITEM NO.	PART NUMBER	DESCRIPTION	QTY.
1	.Rev_02_RACK..		3

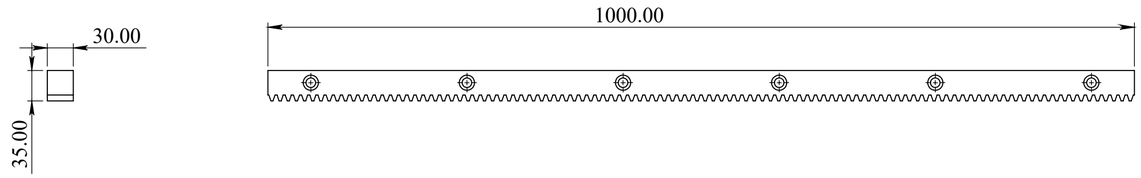

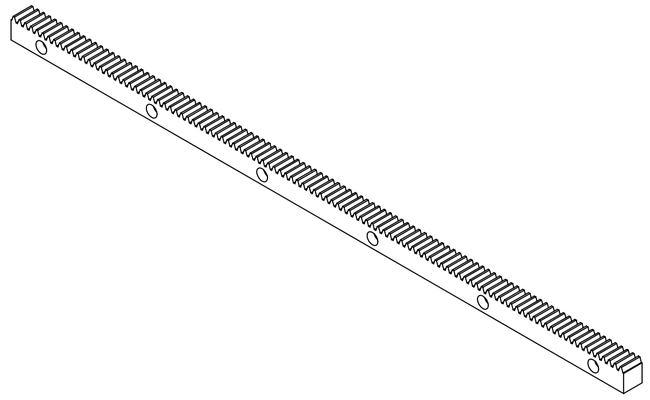

NOTE :

NAME - RACK
ONE PANEL REQ QTY - 3 No'S
TOTAL REQ QTY - 18 No'S.

SPECIAL INSTRUCTION'S :

TITLE - ROOF AUTOMATION

DWG NO - NTPL-244-PM-001-00-00-00

NIHVA TECHNOLOGIES PVT.LTD.PUNE
Website - www.nihva.com

	NAME	SIGNATURE	DATE	
DRAWN	V.W.		26-07-2025	PRODUCT - RETRACTABLE ROOF
CHK'D	S.P.		28-07-2025	PROJECT NO - NTPL-244-PM / REVISION - 04
APPV'D	V.T.		28-07-2025	SITE LOCATION - AHMEDABAD / WEIGHT -
				MATRIAL - / QTY - 01

If any queries contact - design.nihva@gmail.com

ALL DIMENSION ARE IN mm | A2

PROJECTION METHOD:

SCALE :

SHEET 11 OF 11