


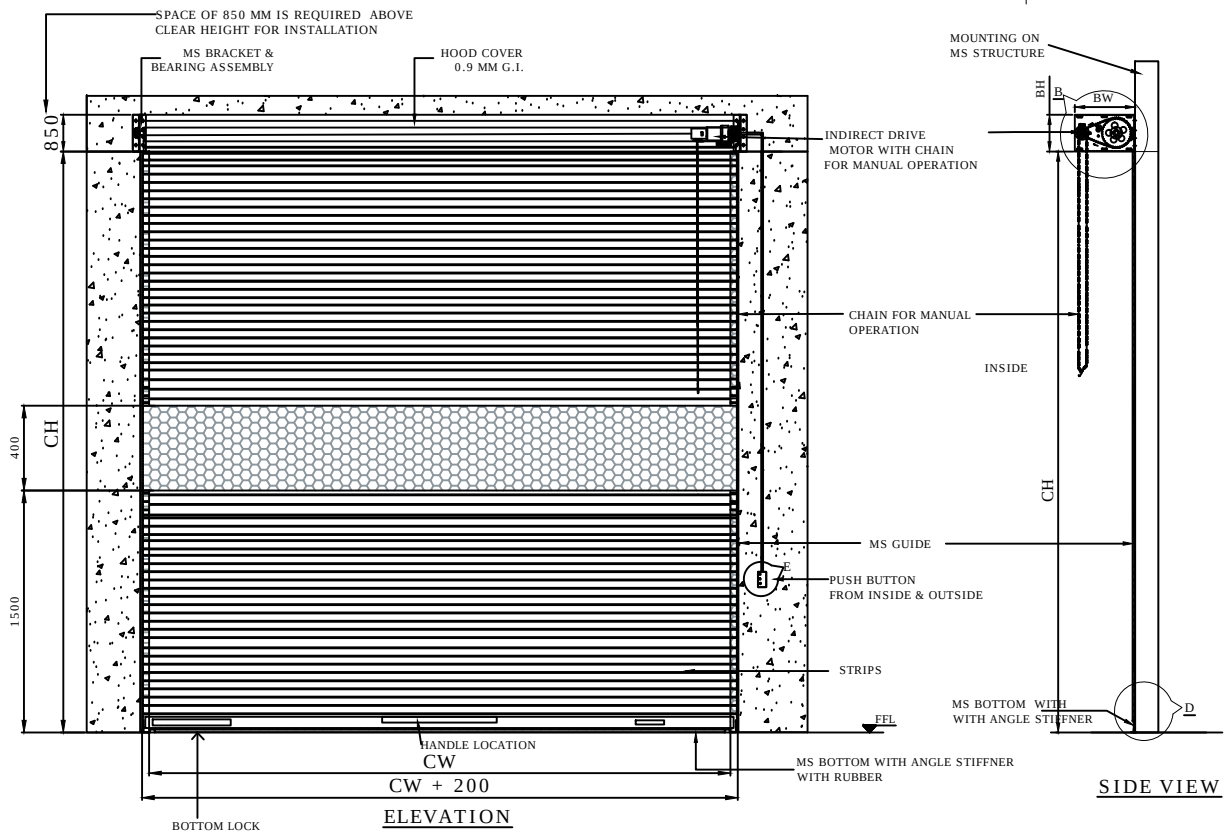


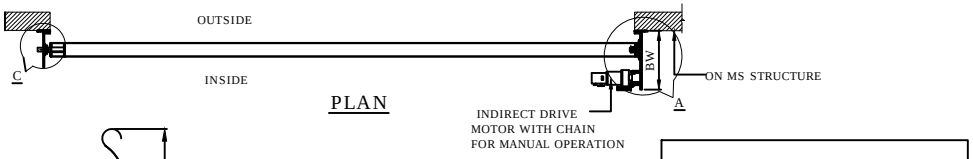


PLAN

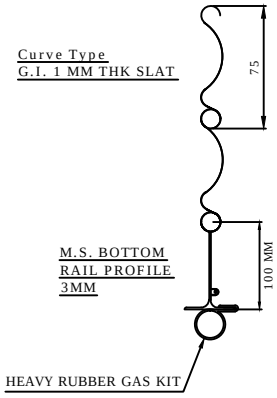


DETAILS : D

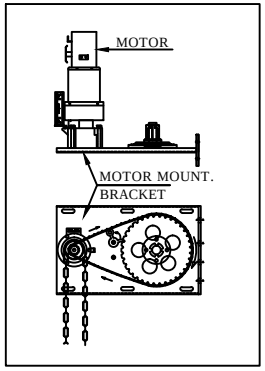


DETAILS : A & B

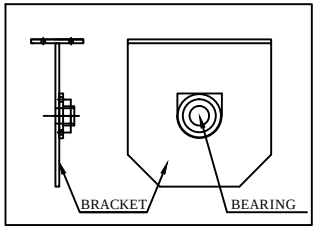

DETAILS : C

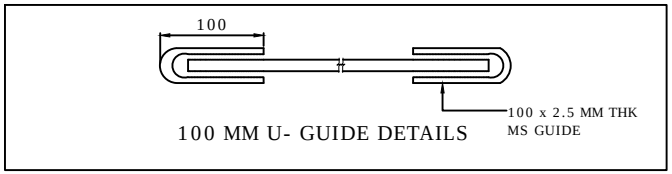

100 MM U- GUIDE DETAILS

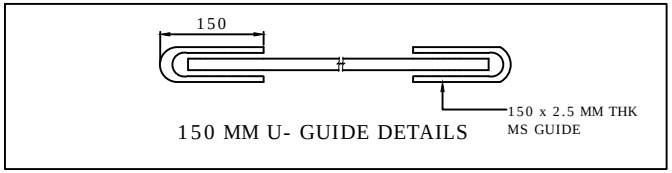

150 MM U- GUIDE DETAILS

REV NO	DRAWN	DATE	REMARK
R05	S.M.S.	13.5.2021	MOUNTING ON M.S. STRUCTURE
R04	V.C.J.	11.5.2021	OUTSIDE PUSHBUTTON ADDED
R03	S.M.S.	29.4.2021	GRILL & U-GUIDE DETAILS ADDED
R02	S.M.S.	1.4.2021	GUIDE DETAILS UPDATED
R01	S.M.S.	31.3.2021	QTY ADDED & RAL SHADE CONFIRMED

SR NO	CLEAR WIDTH (CW)	CLEAR HEIGHT (CH)	QUANTITY	RAL COLOR POWDER COATED
1	4000	4500	2 NOS	RAL 9002

RAL CODE	SHADE	COLOUR
RAL 9002	GREY WHITE	

This drawing & design is the property of NIHVA TECHNOLOGIES. Not to be sold or copied to any other concern.

TITLE: GI MOTORIZED INDIRECT DRIVE ROLLING SHUTTER

	NAME	SIGN	DATE
DRAWN	S.M.S.		16.3.2021
CHECK	S.M.S.		16.3.2021
APPRD.			

NIHVA TECHNOLOGIES PVT. LTD.
NIHVA TECHNOLOGIES PVT. LTD. PUNE
Tel : 020 66304033
Email:- info@nihva.com
Website:- www.nihva.com

CLIENT - ARP CONSTRUCTION

PROJECT - JOHN DEERE

SITE LOCATION - SANASWADI , PUNE

If any queries contact : projectsupport@nihva.com

DWG. NO. : NIHVA/20-21/0177/R05 REV- R05

ALL DIMENSION ARE IN mm

SCALE: NTS WT: SHEET: