




ELEVATION

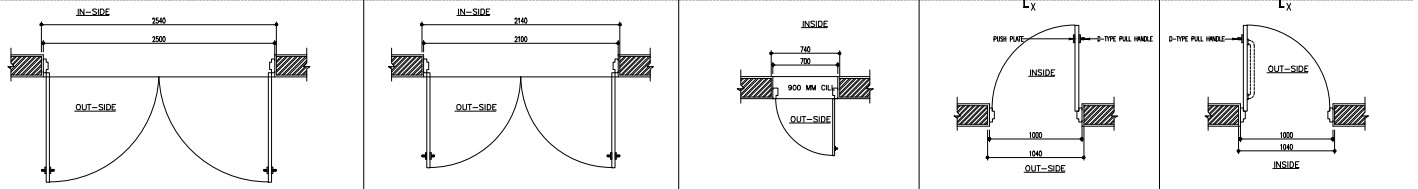



PLAN

| TYPE | FD7 | FD8 | FD9 | D / D1 | D2 |
|---|---|---|---|---|---|
| FINISHED SIZE | 2500X2400 | 2100X2400 | 700x1200 | 900X2100 | 1000X2100 |
| STRUCTURAL OPENING | 2540X2420 | 2140X2420 | 740x1240 | 940X2120 | 1040X2120 |
| LOCATION | ELECTRICAL PANEL ROOM | ELECTRICAL PANEL ROOM | ELECTRICAL | TOILETS ENTRANCE / JANITOR | DISABLED TOILET |
| FRAME TYPE | PROPRIETARY _ TYPE - A | PROPRIETARY _ TYPE - A | PROPRIETARY _ TYPE - D | PROPRIETARY _ TYPE - E | PROPRIETARY _ TYPE - E |
| SHUTTER TYPE | PROPRIETARY FLUSH METAL DOOR | PROPRIETARY FLUSH METAL DOOR | PROPRIETARY FLUSH METAL DOOR | SOLID CORE FLUSH | SOLID CORE FLUSH |
| SHUTTER FINISH | APPROVED ENAMEL PAINT (WOOD GRAINS FINISH) | APPROVED ENAMEL PAINT (WOOD GRAINS FINISH) | APPROVED ENAMEL PAINT (WOOD GRAINS FINISH) | APPROVED LAMINATE FINISH ON BOTH SIDES | APPROVED LAMINATE FINISH ON BOTH SIDES |
| FIRE RATING | 2 HR | 2 HR | 2 HR | ---- | ---- |
| IRONMONGERY | SET - 1 | SET - 1 | SET - 7 | SET - 6 | SET - 6 |
| NOTE : | | | | | DISABLED TOILET DOOR TO HAVE GRAB BAR |

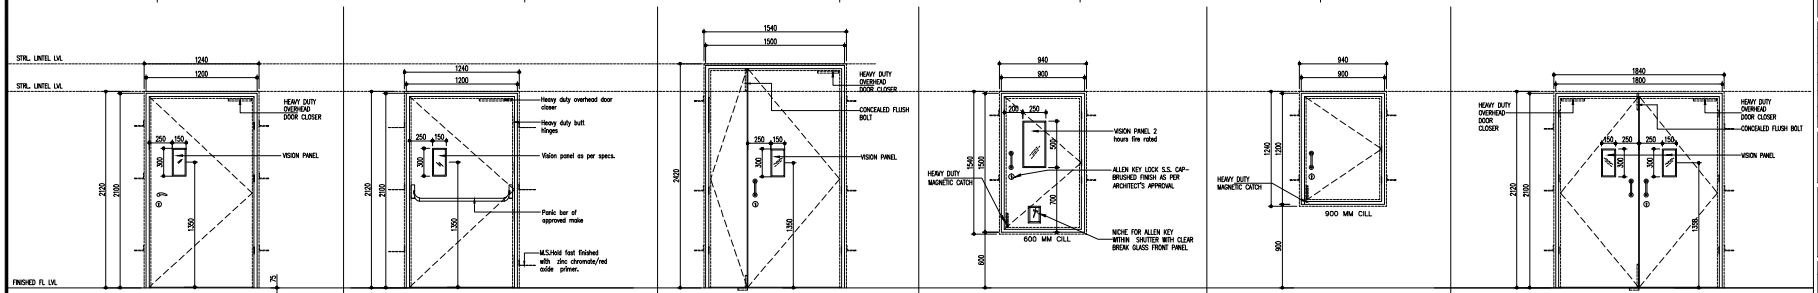



ELEVATION

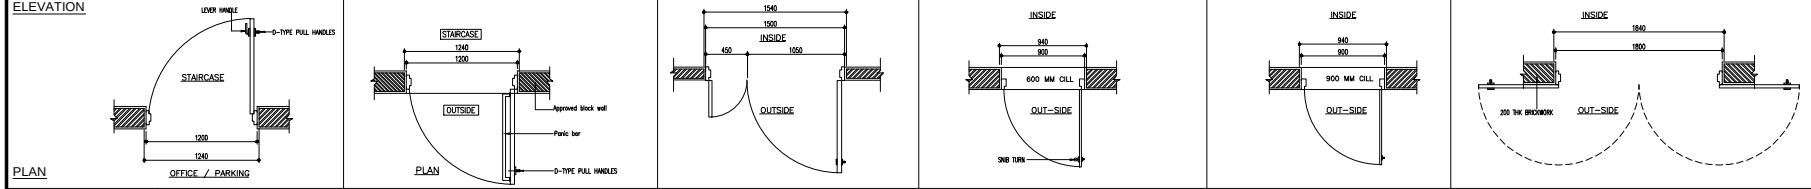


PLAN

| TYPE | FD1 | FD1a | FD2 | FD3 | FD4 | FD5 |
|---|---|---|---|---|---|---|
| FINISHED SIZE | 1200X2100 | 1200 X 2100 | 1500X2400 | 900x1200 | 900x1200 | 1800X2400 |
| STRUCTURAL OPENING | 1240X2120 | 1240 X 2120 | 1540X2420 | 940x1240 | 940x1240 | 1840X2420 |
| LOCATION | STAIRCASE / FIRE CONTRL ROOM | STAIRCASE EXIT AT GF & TERRACE LVLS | VENTILATION P.RM/S.L.LOBBY/GAR.RM/COMM.RM/AHU/REFUGE.TR. | FHR SHAFT | ELECTRICAL | OFFICE - LIFT LOBBY / HVAC PLANT ROOM |
| FRAME TYPE | PROPRIETARY _ TYPE - A | PROPRIETARY _ TYPE - A | PROPRIETARY _ TYPE - A | PROPRIETARY _ TYPE - D | PROPRIETARY _ TYPE - D | PROPRIETARY _ TYPE - A |
| SHUTTER TYPE | PROPRIETARY FLUSH METAL DOOR | PROPRIETARY FLUSH METAL DOOR | PROPRIETARY FLUSH METAL DOOR | PROPRIETARY FLUSH METAL DOOR | PROPRIETARY FLUSH METAL DOOR | PROPRIETARY FLUSH METAL DOOR |
| SHUTTER FINISH | APPROVED ENAMEL PAINT (WOOD GRAINS FINISH) | APPROVED POLYURETHANE / THERMOSETTING PAINT | APPROVED ENAMEL PAINT (WOOD GRAINS FINISH) | APPROVED ENAMEL PAINT (WOOD GRAINS FINISH) | APPROVED ENAMEL PAINT (WOOD GRAINS FINISH) | APPROVED ENAMEL PAINT (WOOD GRAINS FINISH) |
| FIRE RATING | 2 HR | 2 HOURS | 2 HR | 2 HR | 2 HR | 2 HR |
| IRONMONGERY | SET - 2 | SET NO. - 7 | SET - 1 | SET - 4 | SET - 7 | SET - 3 |
| NOTE : | | | | | | |

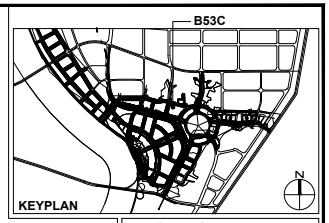


DRAWING REFERENCE :

- FOR SITE PLAN REFER DRAWING NO. A-004
- FOR SITE & BLOCK SETTINGOUT PLAN REFER DRAWING SERIES A-002/003
- FOR FINISHING SCHEDULES REFER DRAWING NO A-005
- FOR FLOOR PLANS REFER DRAWING SERIES A-100
- FOR ELEVATIONS & SECTIONS REFER DRAWING SERIES A-200
- FOR STAIRCASE DETAIL REFER DRAWING SERIES A-300
- FOR TOILET DETAIL REFER DRAWING SERIES A-400
- FOR DOOR DETAILS REFER DRAWING SERIES A-500
- FOR ALUMINUM GLAZING SCHEDULE DETAILS REFER DRAWING SERIES A-600
- FOR LOBBY DETAILS REFER DRAWING SERIES A-700
- FOR RAMP DETAIL REFER DRAWING SERIES A-800
- FOR SIGNAGES & GRAPHICS DETAILS REFER DRAWING SERIES A-900
- FOR BALCONY,UTILITY & OTHER MISCELLEANOUS DETAIL REFER DRAWING SERIES A-1000

NOTES :

- INDICATES 100MMTHK WALL
- INDICATES 150MMTHK WALL
- INDICATES 200MMTHK WALL
- INDICATES 200MM THK NON STRUCTURAL RC WALL
- DOOR & WINDOW SIZES INDICATED IN THE SCHEDULE ARE FINISHED DIMENSIONS. 20MM PLASTERING MARGIN SHALL BE PROVIDED OVER THE SIZES INDICATED ON ALL SIDES.
- ALL STRUCTURAL/CIVIL PROVISION FOR SERVICE ROOMS, PHE/ RAINWATER DISPOSAL SHALL BE MADE AS PER RESPECTIVE CONSULTANTS REQUIREMENTS AND DRAWING.
- INDICATES TILE DROP (IN TOILETS/BALCONY)

GENERAL NOTES

- ALL DIMENSIONS ARE IN MILLIMETERS
- THIS DRAWING IS A COPYRIGHT AND PROPERTY OF THE ARCHITECT, IS NOT TO BE PRODUCED, COPIED, HANDED OVER TO THIRD PARTY OR USED FOR ANY OTHER PURPOSE OTHER THAN FOR WHICH IT IS INTENDED.
- ALL DIMENSIONS SHALL BE VERIFIED ON SITE PRIOR TO START OF WORK. ANY DISCREPANCY SHALL BE BROUGHT TO THE NOTICE OF THE ARCHITECT.
- THE CONTRACTOR MUST CHECK ALL DIMENSIONS AND DETAILS AND BE RESPONSIBLE FOR THE SAME. ANY DISCREPANCY SHALL BE BROUGHT TO THE NOTICE OF THE ARCHITECT.
- THIS DRAWING IS TO BE READ AND NOT SCALED.
- THIS DRAWING SHALL BE READ IN CONJUNCTION WITH ALL RELEVANT ARCHITECTURAL, STRUCTURAL AND SERVICES DRAWINGS. ANY DISCREPANCY NOTICED SHALL BE BROUGHT TO THE ATTENTION OF THE CONSULTANTS AND RESOLVED AS SOON AS POSSIBLE BUT ALWAYS PRIOR TO PROCUREMENT / EXECUTION OF WORKS

| NO | DESCRIPTION | DATE | SIGN. |
|---|---|---|---|
| | ISSUALS | | |

| NO | DESCRIPTION | DATE | SIGN. |
|---|---|---|---|
| | REVISION | | |

SHEET NO.:

ORIENTATION:

CLIENTS :

PRESTIGE ESTATES PROJECTS LTD
The Falcon House, No 1, Main Guard Cross Road, Bangalore - 560 001.
Phone : 91-80-25591080. Fax :91-80-25591945
web : www.prestigeconstructions.com

PROJECT TITLE :

PRESTIGE FINTECH
@
GIFT
GUJARAT INTERNATIONAL FINANCE TEC-CITY COMPANY LTD.

STRUCTURAL CONSULTANT'S :

DUCON
CONSULTANTS PRIVATE LIMITED
A3-4A, 3rd FLOOR, Sahi prathiba, Corporate road, Nr prahladnagar Garden, S.G.ROAD, Ahm-A-15.
E-mails contact@duconconsultants.in
PH:4007319645,45410630,65410631

PROJECT CONSULTANTS : :

RSP PROJECT CONSULTANTS : (India) Pvt

CONSTRUCTION DRAWING

SUBJECT OF DRAWING :

JOINERY DETAIL

FILE NAME :

| SCALE : 1:25 | DATE : 21/03/2017 | JOB.NO: 00000 |
|---|---|---|
| DEALT RAKESH | | |

DRAWING NO : PG-B53C-A-601 REVISION: 00