
THIS DRAWING IS THE PROPERTY AND COPYRIGHT OF © ® **TAO Architecture / TAO- Interior / TAO- Design Pvt. Ltd.** IT SHALL NOT BE COPIED, REPRODUCED OR USED WITHOUT WRITTEN CONSENT.

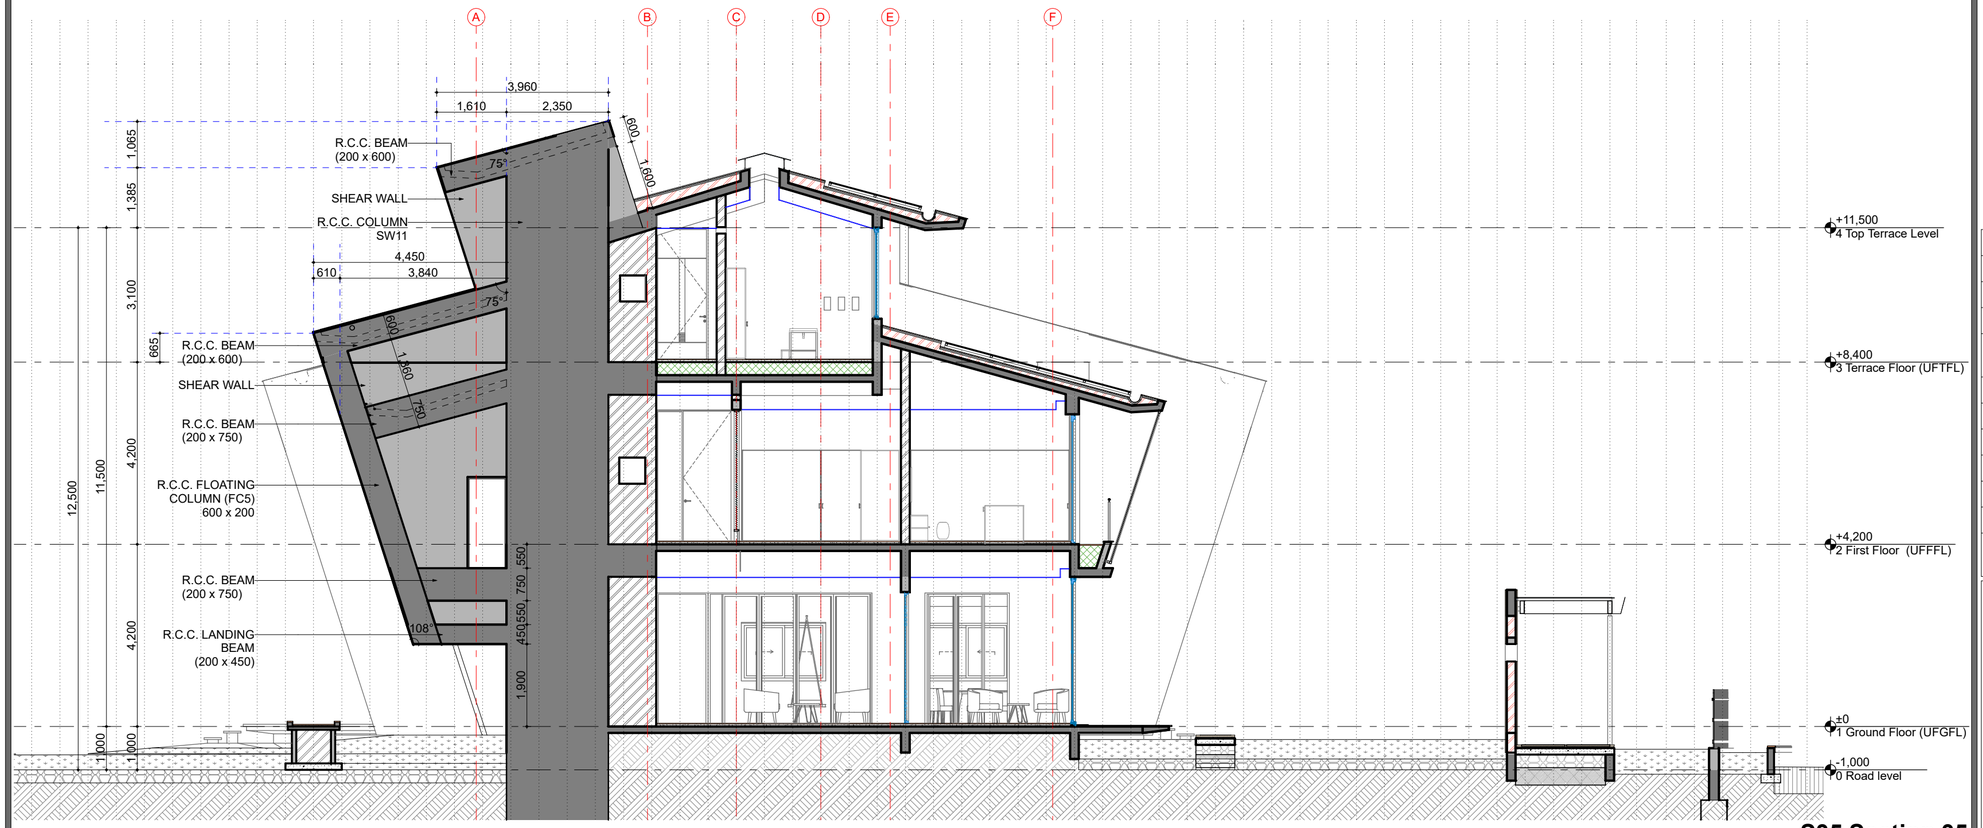

S35 Section 35

NOTES: GENERAL

- ALL DIMENSIONS AREA IN mm (MILLIMETER).
- DRAWING SHALL NOT BE SCALED AND ONLY WRITTEN DIMENSIONS SHALL BE FOLLOWED.
- IN CASE OF ANY DISCREPANCY FOUND IN DRAWINGS AND DETAILS, IT SHALL BE BROUGHT TO THE NOTICE OF THE ARCHITECT AND RECTIFIED PRIOR TO ITS EXECUTION.
- THIS DRAWING IS ISSUED STRICTLY WITH AN UNDERSTANDING THAT IT WILL BE USED ONLY FOR THE PURPOSE MENTIONED AND SHALL NOT BE RETURNED AFTER COMPLETION.
- LARGER SCALE DRAWINGS AND DETAILS SUPERSEDE THE SMALLER SCALE DRAWINGS AND DETAILS.
- THIS DRAWING SHALL BE REFERRED ONLY FOR THE PURPOSE MENTIONED IN ITS TITLE (FLOORING PATTERN, FALSE CEILING, SHUTTERING PATTERN, ELECTRICAL, PLUMBING ETC.)

NOTES: CONTENT

LEGEND

SYMBOL	DESCRIPTION	SYMBOL	DESCRIPTION
	UNFINISHED LEVELS	D#	DOOR TAG
	BUILDING LINE	OP#	OPENING TAG
	PLOT BOUNDARY	C#	COLUMN NUMBER TAG
W#	WINDOW TAG	UFGFL	UNFINISH GROUND FLOOR LEVEL
GZ#	GLAZING TAG		STRUCTURAL RCC
#	STRUCTURAL GRID LINE		SUNK SLAB
E-#	ELEVATION TAG	S#	SECTION TAG
	NON STRUCTURAL WALLS		FALSE CEILING

#	DATE	ISSUED TO	COPIES	PURPOSE
C	23.07.2025	PMC	01	FOR SITE EXECUTION
B	04.04.2025	PMC	01	FOR SITE EXECUTION
A	16.12.2024	PMC	01	FOR STUDY PURPOSE

SUFFIX

#	DATE	REVISION	CHECKED
03.	23.07.2025	R2	ABRAR / KAVISH
02.	04.04.2025	R1	ABRAR / KAVISH
01.	16.12.2024	R0	ABRAR / KAVISH

REVISIONS



GRID 650 x 650
KEY PLAN

N
NORTH

GOOD FOR CONSTRUCTION TAO PUNE
SEAL

SIGN

PROJECT	**FE-97 RESIDENCE**
CONTENT	**SECTION 35**
DRG NO	AI/TT/2301

DRAWN	ATUL / ARUSHI	SCALE	**A2**	1:100
CHECKED	KAVISH / ABRAR		A3	
APPROVED	MANISH	DATE	13-11-2025	

TAOSTUDIO
ARCHITECTURE + INTERIORS + LANDSCAPE + ART INSTALLATION
A/2, FRIENDS ENCLAVE SOCIETY, PART-2, WEST BLOCK, OPP. SAI HIRA COMPLEX,MUNDHWA, PUNE, MAHARASHTRA, INDIA.
PIN - 411036 PHONE : +91-744-771-9343 / 44
E-mail: admin@taoarchitecture.com