Weitergabe sowie Vervielfältigung dieses Dokuments, Verwertung und Mitteilung seines Inhalts sind nur nach vorheriger ausdrücklicher schriftlicher Zustimmung von SMS Meer GmbH gestattet. Das Dokument ist vor unberechtigtem Zugriff Dritter zu schützen. Zuwiderhandlungen verpflichten zu Schadensersatz. Alle Rechte aus Patent-/Gebrauchsmuster-/Markenschutz vorbehalten.

The reproduction, distribution and utilization of this document as well as the disclosure of its content to others without prior explicit written consent of SMS Meer GmbH is prohibited. Holder has to protect this document against unauthorized withdrawal of third parties. Offenders will be held liable for the payment of damages. All rights reserved in case of patent/utility model/trademark protection.

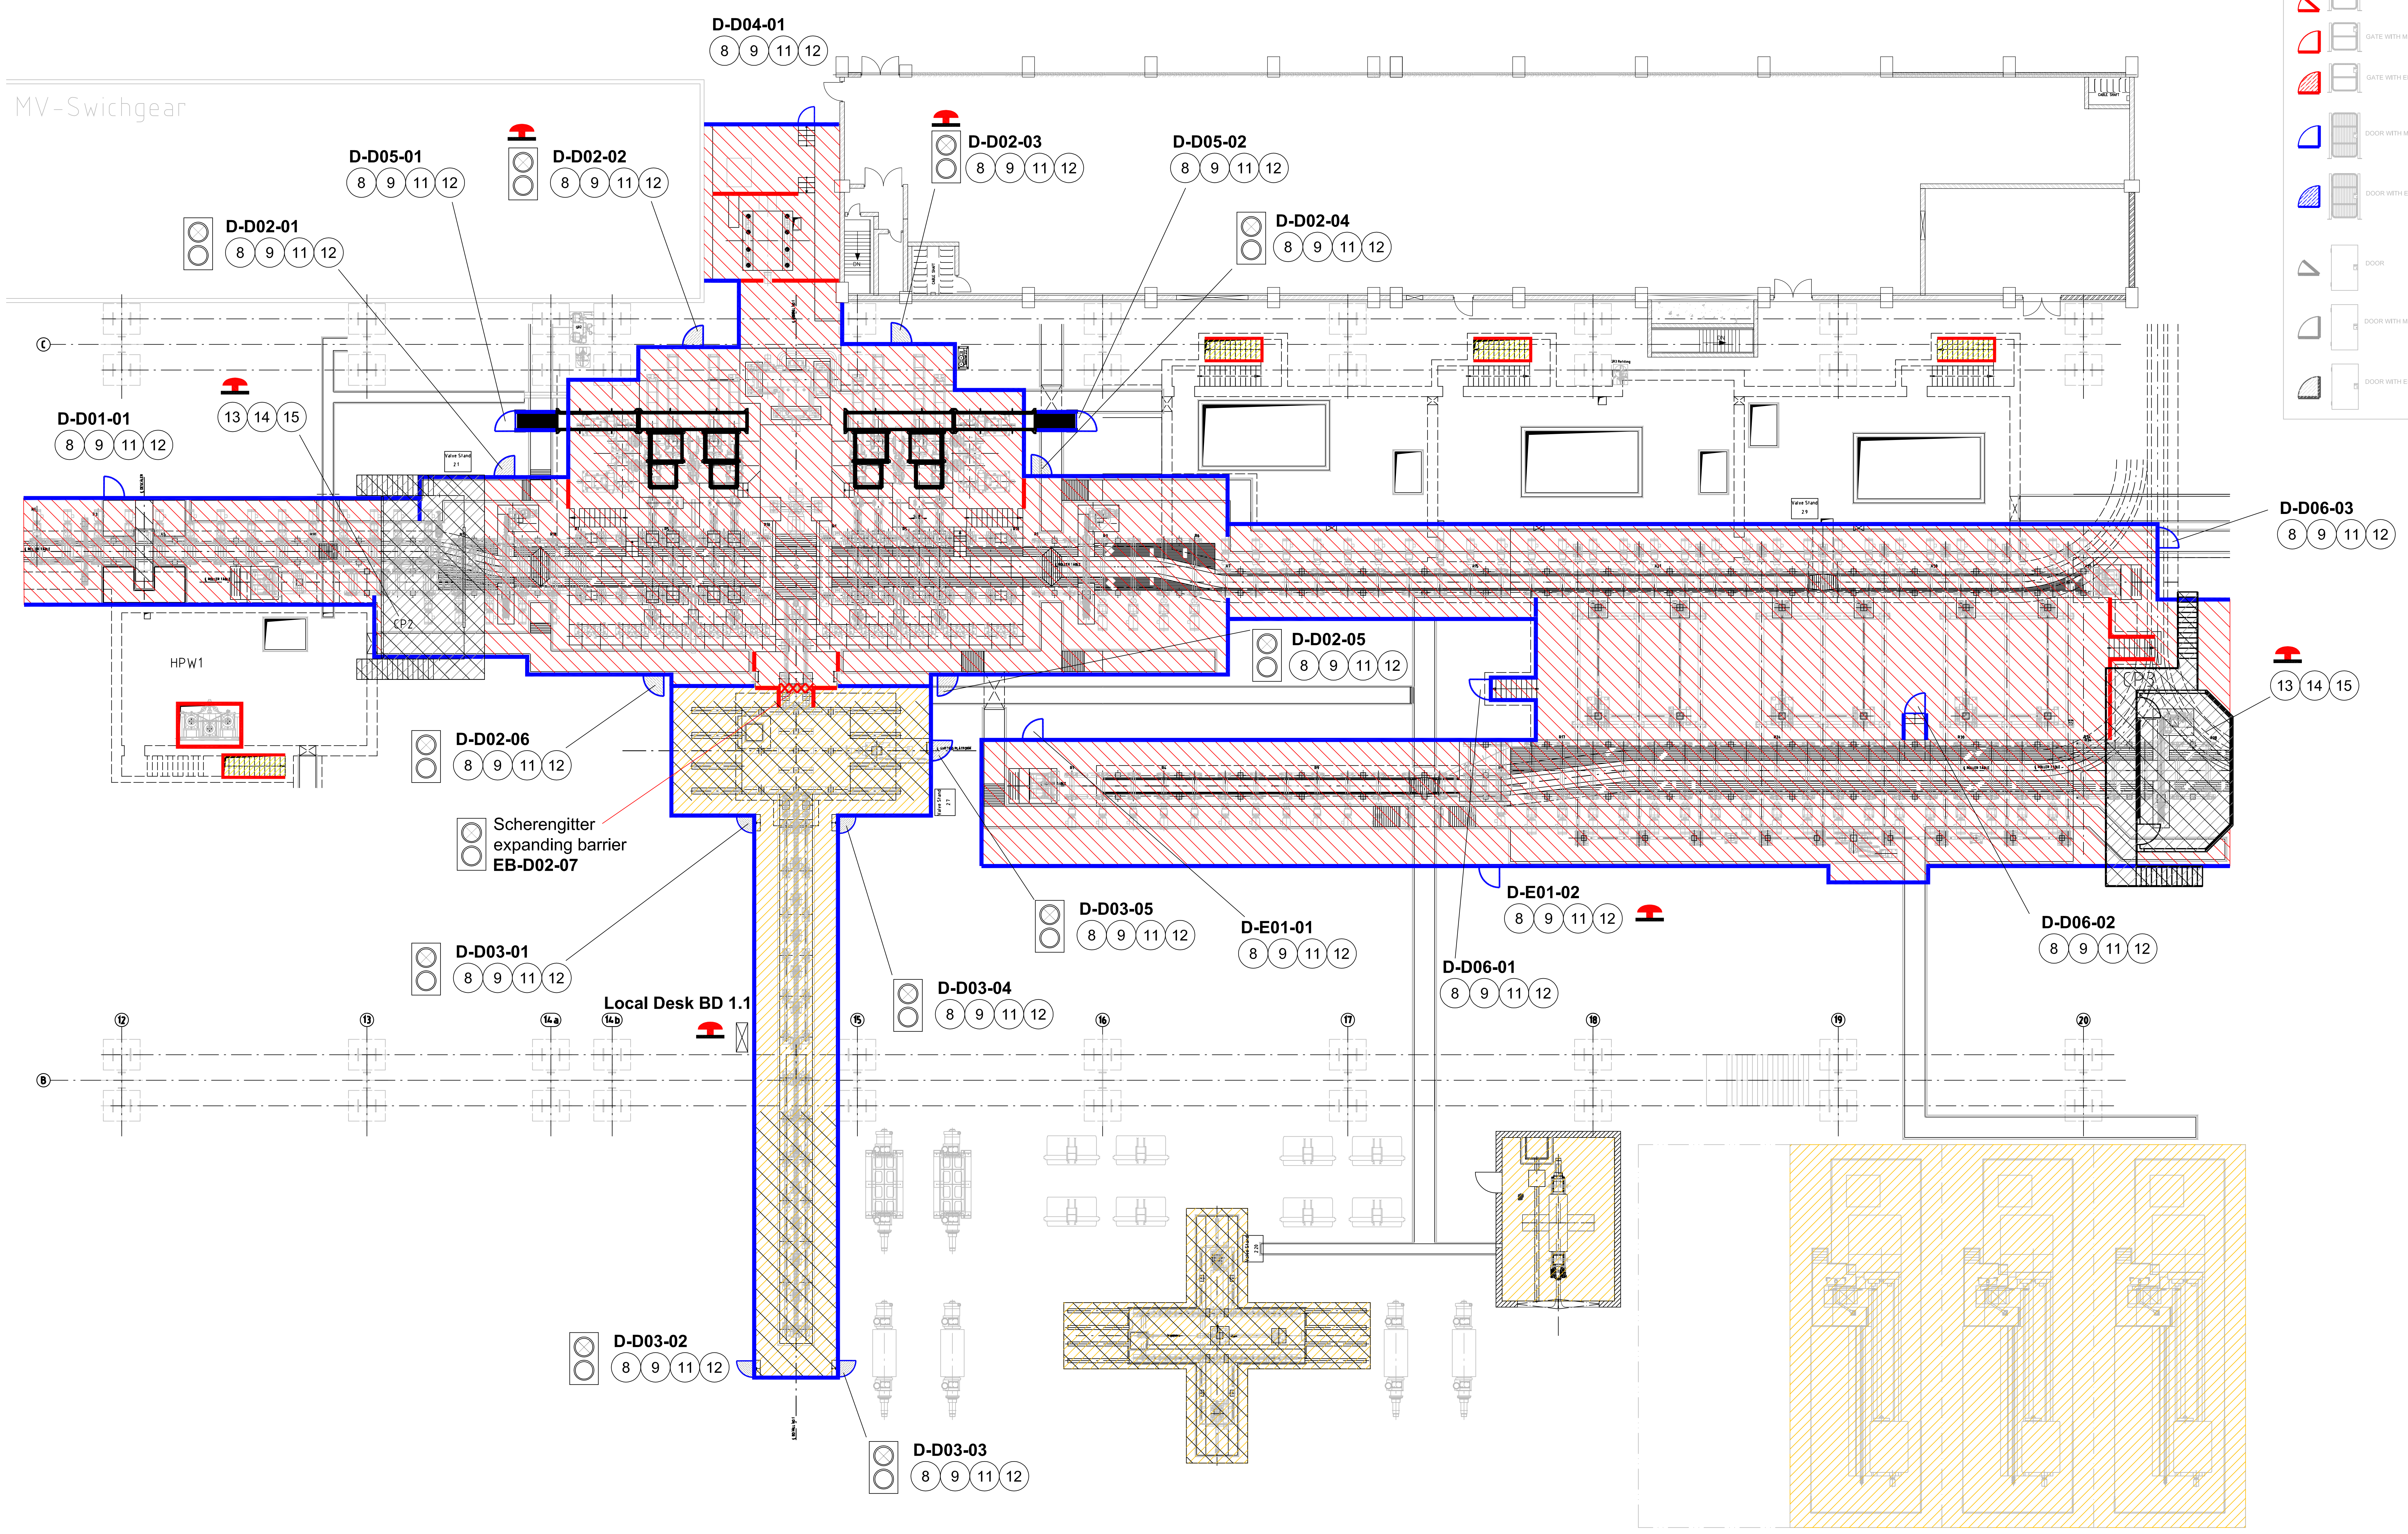

GATE	DANGER ZONE 1 No access while unit is in operation.	ESCAPE ROUTES
GATE WITH MECH. LOCKING DEVICE	DANGER ZONE 2 Access only to qualified and authorized persons possible in defined operating states. High Residual Risks Note safety instructions in operating and maintenance manual.	RAILING
GATE WITH ELECT. LOCKING DEVICE	DANGER ZONE 3 Access only to qualified and authorized persons possible in defined operating states. Low Residual Risks Note safety instructions in operating and maintenance manual.	REMOVABLE RAILING
DOOR WITH MECH. LOCKING DEVICE	DANGER ZONE 4 Permanente working place: Unrestricted access possible while unit is in operation. Note general safety instructions.	FENCE
DOOR WITH ELECT. LOCKING DEVICE	WORKING PLACE Part of no access zone, that can be entered by trained operators under particular conditions only Note safety instructions in operating and maintenance manual.	REMOVABLE FENCE
DOOR	REQUEST-/ ACKNOWLEDGEMENT BUTTON	REMOVABLE CHAIN
DOOR WITH MECH. LOCKING DEVICE	EMERGENCY STOP	LIGHT CURTAIN
DOOR WITH ELECT. LOCKING DEVICE	ACKNOWLEDGEMENT BUTTON	

9463 0000 / RAILBHIL

CATEGORY OF DRWG.	APPROVAL	INFORMATION	REFERENCE	RECORD	CONSTRUCTION

SAIL

BHILAI STEEL PLANT, BHILAI, CHATTISGARH
7,0 MTPA EXPANSION

मेकॉन लिमिटेड
MECON LIMITED

VENSDOR'S NAME: SMS Meer/SMS Meer India/ABB
PACKAGE DESCRIPTION: UNIVERSAL RAIL MILL (Pkg No-047)
TITLE OF DRAWING. PARTITION 2,3 SAFETY LAYOUT
SCALE-
VENDOR'S DRG NO.-
PROJECT DRG. NO. BSP-SMS Meer-08-047-21-130-35-BE-06651
REV. -

Fertigungsvorschriften
Manufacturing Instructions
SN 200

Ursprung / Origin
Fertiggewicht
Finished weight
kg
Modell-Nr.
Pattern-No.
Werkstoff / Material
Projektionsmethode 1
First angle projection method
ISO 128

	Datum Date	Name
Bearb. Drawn	27.09.11	Fryen
Geprüft Checked	27.09.11	Prätzel
Norm Stand		

Typ
Type
Safety Layout
Benennung
Teilbereich. 2. 3
Title
PARTITION 2. 3
Maßstab
Scale
1:100
Sach-Nr.
Drawing-No.
0100133-00.651
Blatt
Sheet
1
2
Blätter
Sheets

Aus- gabe Issue	Änderung Revision	Datum Date	Name

SMS
MEER
SMS group

Ersatz für:/Supersedes:
Ersetzt durch:/Superseded by:

Diese Zeichnung und alle darauf enthaltenen Informationen sind vertraulich. This drawing and all information on it is confidential.

A0