
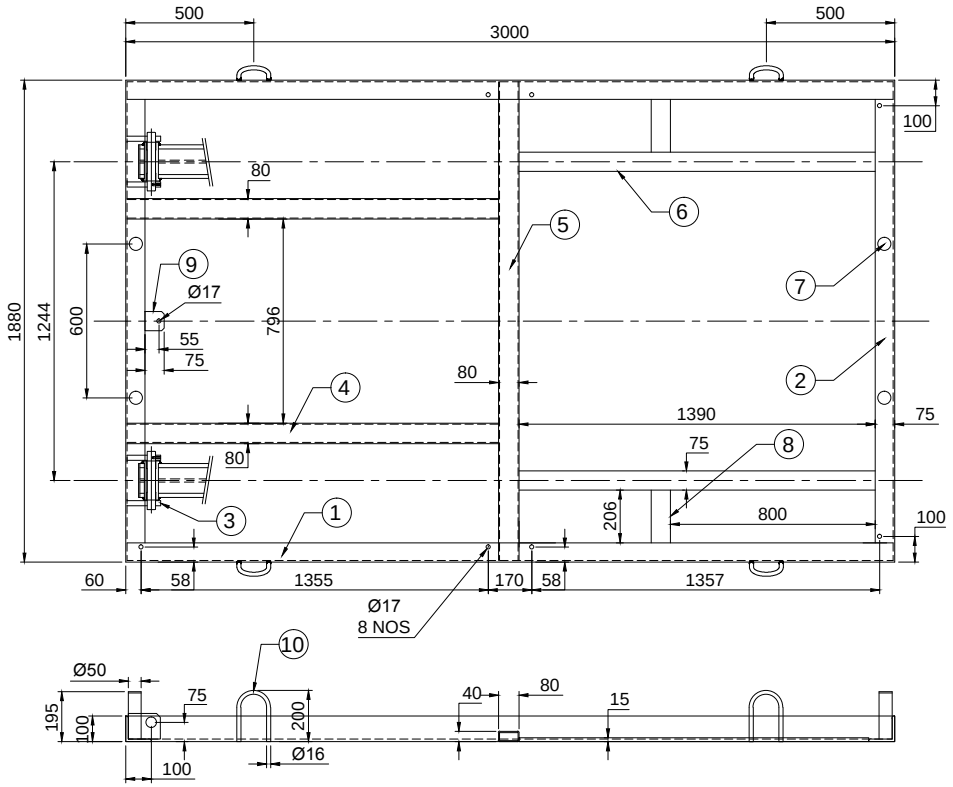


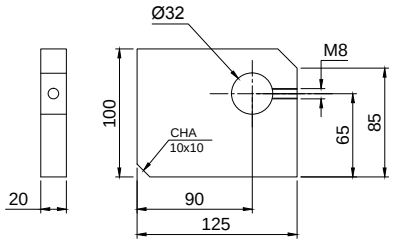

SR NO	PART NAME	SPECIFICATION	QTY
1	ISA	100 X 100 X 10 X 3000L	2 NOS
2	ISA	100 X 100 X 10 X 1860L	2 NOS
3	LASER PRO.	100 X 20 THK X 125L	4 NOS
4	R.TUBE	80 X 40 X 4 X 1448L	2 NOS
5	R.TUBE	80 X 40 X 4 X 1860L	1 NO
6	EN8 FLAT	75 X 15 X 1390L	2 NOS
7	STOPPER	EN8 Ø50 X 200L	4 NOS
8	FLAT	75 X 15 X 205L	2 NOS
9	FLAT	75 X 15 X 75L	1 NO
10	MS BAR	Ø16 X 500L	4 NOS
11	ANCHOR BOLT	M16 X 150L	9 NOS

This drawing & design is the property of NIHVA TECHNOLOGIES. Not to be sold or copied to any other concern.

TITLE: BASE FRAME

	NAME	SIGN	DATE
DRAWN	P.A		19.11.2018
CHECK	R.D		19.11.2018
APPRD.	V.T		19.11.2018

NIHVA TECHNOLOGIES PVT. LTD.
NIHVA TECHNOLOGIES PVT. LTD. PUNE
Tel : 020 66304033
Email:- info@nihva.com
Website:- www.nihva.com

CLIENT -

PROJECT -

SITE LOCATION -

If any queries contact : design@nihva.com

DWG. NO. : NIHVA/18-19/MFG/NSL1002/03 | REV- 0

ALL DIMENSION ARE IN mm | SCALE: NTS | WT: | SHEET: 01 OF 01