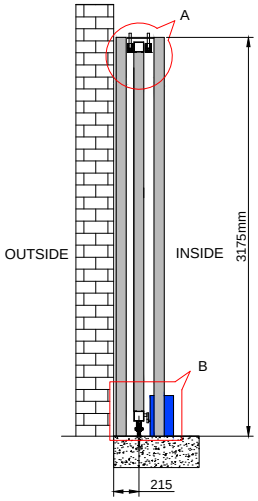

SIDE VIEW

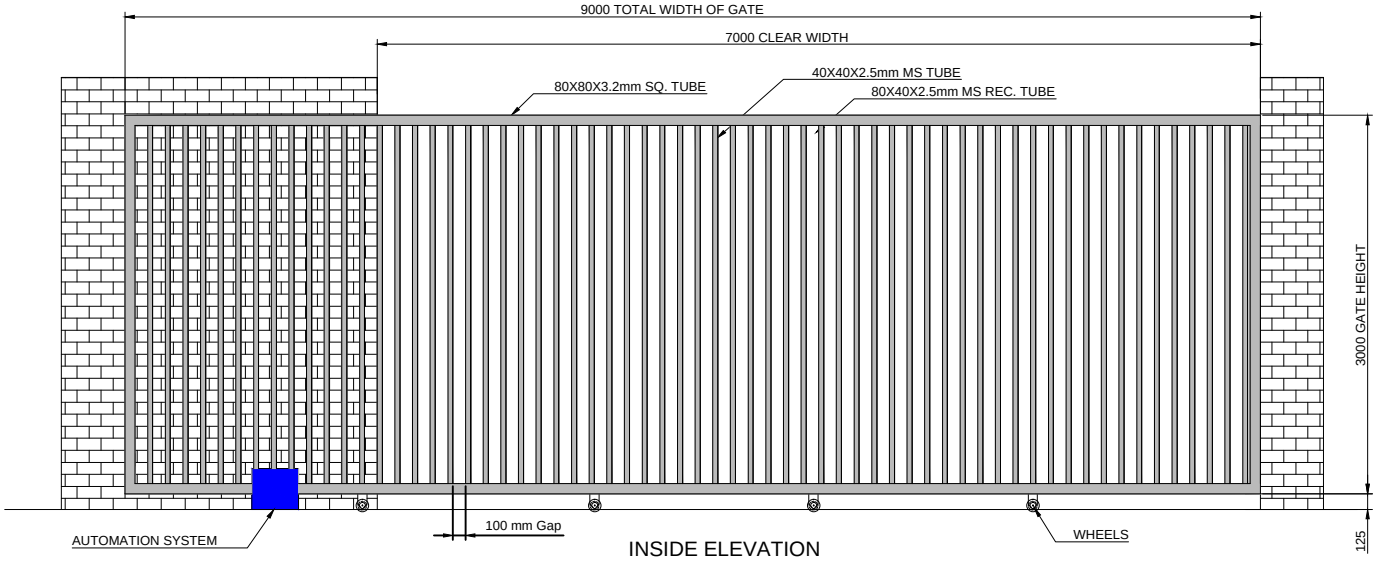

INSIDE ELEVATION

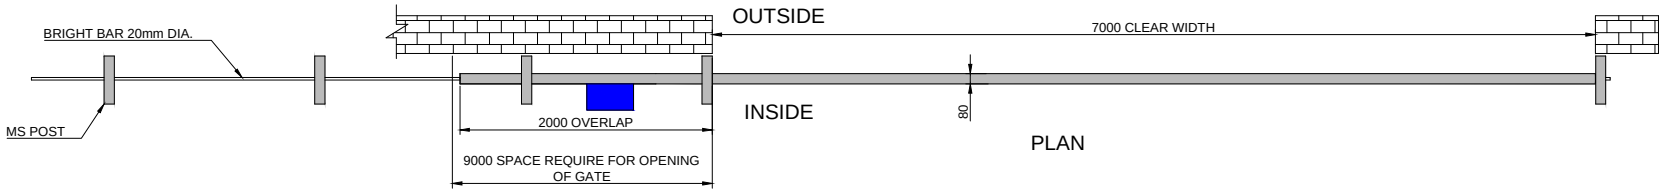

PLAN

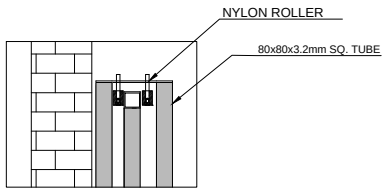

DETAILED VIEW OF A

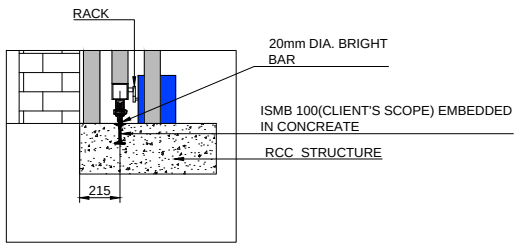

DETAILED VIEW OF B

NOTE: NIHVA RECOMMENDS THAT HEIGHT OF GATE SHOULD BE 2500mm.

DIMENSION :

CLEAR WIDTH	CLEAR HEIGHT	QUANTITY
7000 mm	3000 mm	1 NOS.

MATERIAL : MS

THICKNESS :

MATERIAL SPECIFICATION

SR NO	TUBE SIZE	
1	MS TUBE 80X80X3.2mm	OUTER TUBE
2	MS TUBE 40X40X2.5mm	INNER TUBE

NOTE: ALL REQUIRED CIVIL WORK WILL BE IN CLIENT'S SCOPE.
ONE COAT RED OXIDE PRIMER WILL BE GIVEN TO THE STRUCTURE OF GATE.
ISMB 100 WILL BE CLIENTS SCOPE.

NIHVA TECHNOLOGIES PVT. LTD.
NIHVA TECHNOLOGY PVT. LTD. PUNE
Email:- info@nihva.com
Website:- www.nihva.com

TITLE:

SINGLE LEAF MOTORISED SLIDING GATE

CLIENT'S APPROVAL :

CLIENT - BVG INDIA LIMITED

PROJECT -

SITE LOCATION -

DWG. NO. : NIHVA/16-17/0100/2

SCALE: NTS	WT:	SHEET:1 OF 1

DRAWN BY: OMKAR	DATE: 09-11-2016
CHECK : SAGAR P.	DATE: 09-11-2016

If any queries contact : projects@nihva.com

NOTE: ALL DIMENSION ARE IN mm

THIS DRAWING & DESIGNING IS THE PROPERTY OF NIHVA TECHNOLOGIES. NOT BE SOLD OR COPY TO ANY OTHER CONCERN.