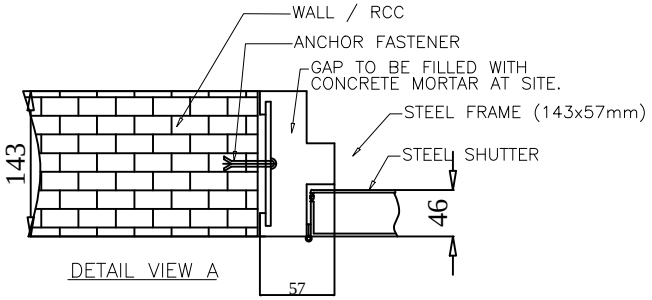

NOTES:–
ALL DIMENSIONS ARE IN MM.

NOTES:–
ALL DIMENSIONS ARE IN MM.

A. ABBREVIATION
Wall Opening Width : WOW
Wall Opening Height : WOH
Frame Opening Height : FOH
Frame Opening Width : FOW
Shutter Opening Height : SOH
Shutter Opening Width : SOW

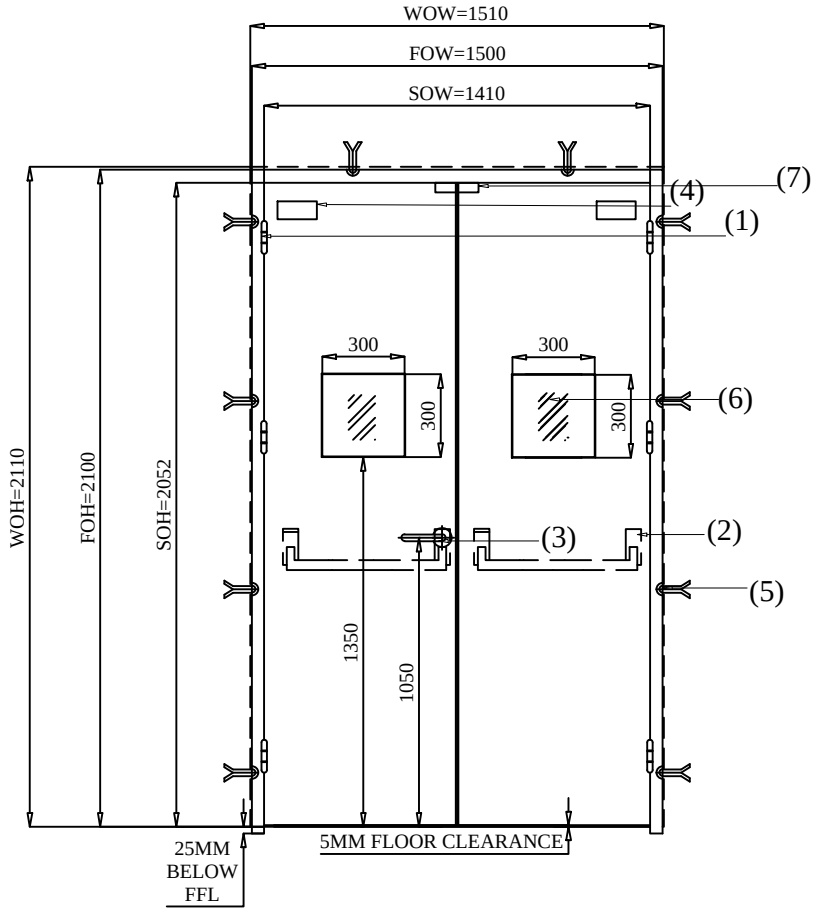

MATERIAL OF CONSTRUCTION
2 HR FIRE RATED

FRAME : G.I. 1.60mm Sheet
SHUTTER : G.I. 1.20mm Sheet
THICKNESS : 46MM
FRAME PROFILE : 143 x 57Mm (Double Ribet)

INFILL MATERIAL : MINERAL WOOL
DENSITY 96kg/cm3

PAINT: AS PER AS APPROVED RAL SHADE
POWDER COATED (DFT 80 Microns min)

SCHEDULE OF HARDWARE

1) S.S. Ball Bearing Hinges - Geze Make - 6 NOS.
2) Panic Bar for Double Leaf Door - Yale Make
3) External Trim Bar (Panic Latch) - Yale Make -1 Nos.
4) Heavy Duty Door Closer Geze Make -2 Nos
5) Anchor Fastener - 8 x 80MM.
6) Vision Panel with Fire Rated Glass of Size: 300 x 300MM - Clear Glass 6mm Thick - 2 Nos.
7) Door Coordinator - 1 Nos (Yale Make)

DATE	REV.	STATUS	PARTICULARS	BY	CHKD.	APPD.

REVISIONS.

STATUS CODE: 1:PRELIMINERY COPY 2:FOR REVIEW 3:FOR MATERIAL PROCUREMENT
4:FOR APPROVAL 5:APPROVED FOR CONSTRUCTION

THIS DESIGNED OR DRAWING IS THE PROPERTY OF RADIANT SAFEDOORS PVT. LTD. IT IS SUBJECT TO THEIR RECALL, AND MUST NOT BE LENT,COPIED OR REPRODUCED WITHOUT THEIR WRITTEN PERMISSION.

APPROVED FOR CONSTRUCTION BY.:–

	SIGN	DATE
DRAWN. BY		02/04/2019
CHKD. BY		02/04/2019
APPD. BY		02/04/2019

CLIENT : M/S. Nihva Technologies Pvt Ltd
SITE :
QTY. 1 Nos
TITLE: DOUBLE LEAF FIRE STEEL DOOR WITH PANIC BAR
DOOR SIZE: 1500MM (W) x 2100MM (H) – D.L.
PROJECTION
SCALE N.T.S.
RADIANT SAFEDOORS PVT. LTD.
WORKS : 539, PHASE II, VATVA GIDC, AHMEDABAD.
DRG. NO. RSPL/190402/06