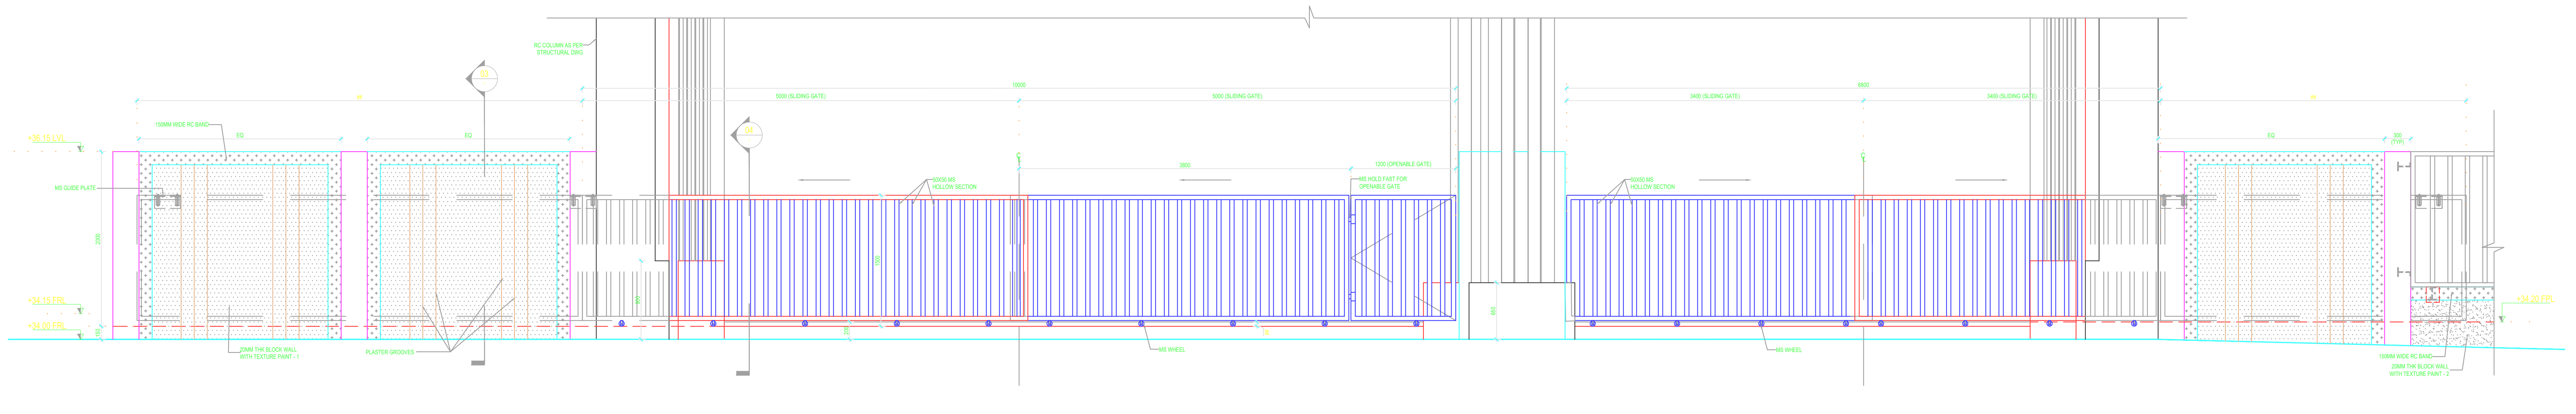
RC COLUMN AS PER STRUCTURAL DWG
03
04
10000
5000 (SLIDING GATE)
6800
3400 (SLIDING GATE)
150MM WIDE RC BAND
EQ
+36.15 LVL
MS GUIDE PLATE
2000
+34.15 FRL
+34.00 FRL
150
20MM THK BLOCK WALL WITH TEXTURE PAINT - 1
PLASTER GROOVES
50X50 MS HOLLOW SECTION
1500
900
200
3800
1200 (OPENABLE GATE)
MS HOLD FAST FOR OPENABLE GATE
650
MS WHEEL
300 (TYP)
+34.20 FPL
20MM THK BLOCK WALL WITH TEXTURE PAINT - 2

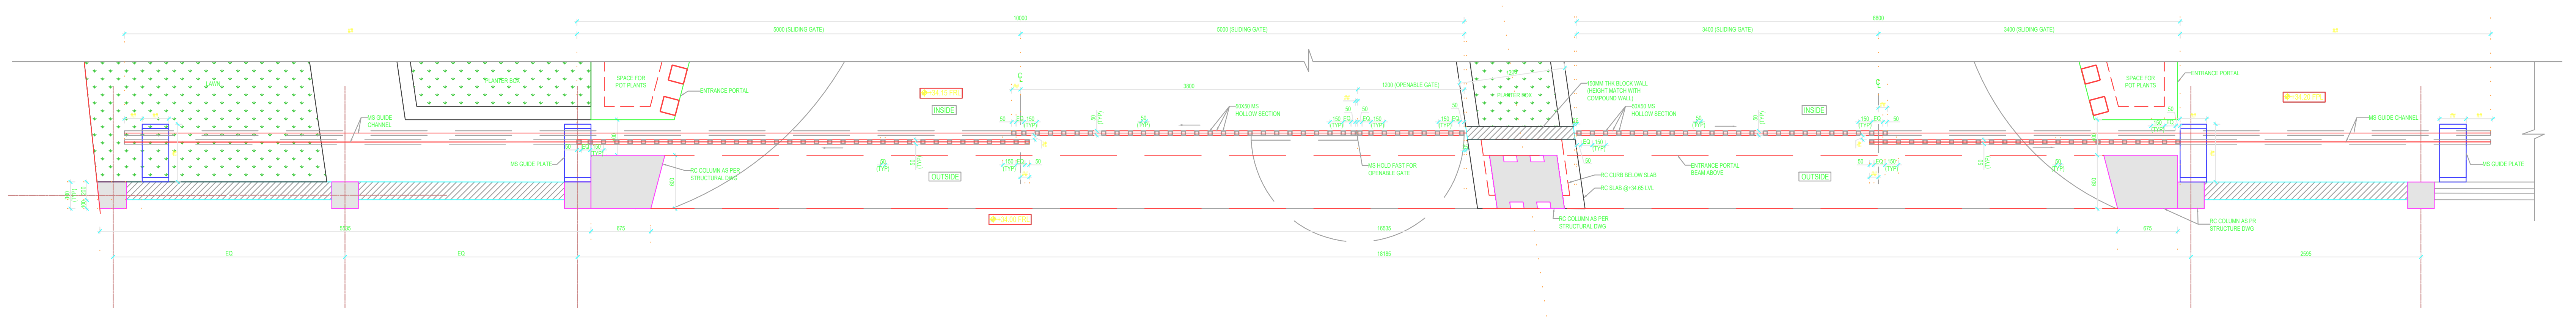
5000 (SLIDING GATE)
10000
3400 (SLIDING GATE)
6800
LAWN
PLANTER BOX
SPACE FOR POT PLANTS
ENTRANCE PORTAL
MS GUIDE CHANNEL
MS GUIDE PLATE
RC COLUMN AS PER STRUCTURAL DWG
300 (TYP)
200
100
600
675
5535
EQ
50
150 (TYP)
+34.15 FRL
INSIDE
OUTSIDE
+34.00 FRL
3800
1200 (OPENABLE GATE)
50X50 MS HOLLOW SECTION
MS HOLD FAST FOR OPENABLE GATE
1200
150MM THK BLOCK WALL (HEIGHT MATCH WITH COMPOUND WALL)
ENTRANCE PORTAL BEAM ABOVE
RC CURB BELOW SLAB
RC SLAB @+34.65 LVL
16535
18185
+34.20 FPL
400
RC COLUMN AS PR STRUCTURE DWG
2595

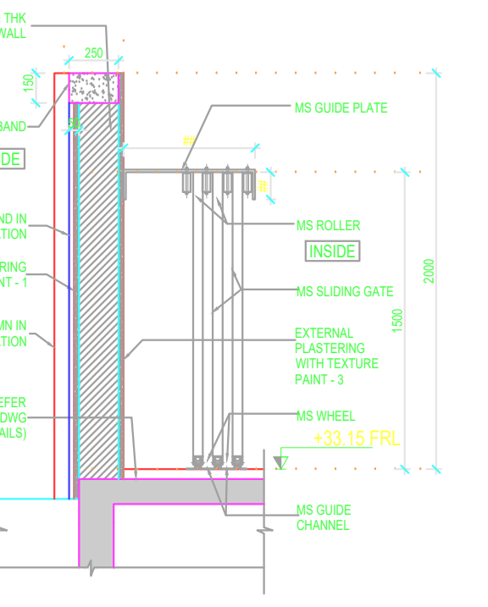
200MM THK BLOCK WALL
250
150
RC BAND
OUTSIDE
MS GUIDE PLATE
MS ROLLER
INSIDE
PLASTER BAND IN ELEVATION
EXTERNAL PLASTERING WITH TEXTURE PAINT - 1
MS SLIDING GATE
RC COLUMN IN ELEVATION
EXTERNAL PLASTERING WITH TEXTURE PAINT - 3
DRAIN SLAB (REFER STRUCTURAL DWG FOR DETAILS)
MS WHEEL
+33.15 FRL
MS GUIDE CHANNEL
1500
2000

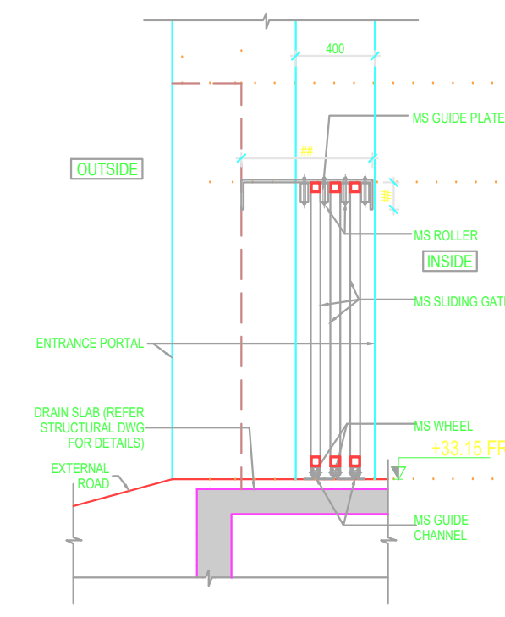
400
MS GUIDE PLATE
OUTSIDE
MS ROLLER
INSIDE
MS SLIDING GATE
ENTRANCE PORTAL
DRAIN SLAB (REFER STRUCTURAL DWG FOR DETAILS)
MS WHEEL
+33.15 FRL
EXTERNAL ROAD
MS GUIDE CHANNEL
1500
2000

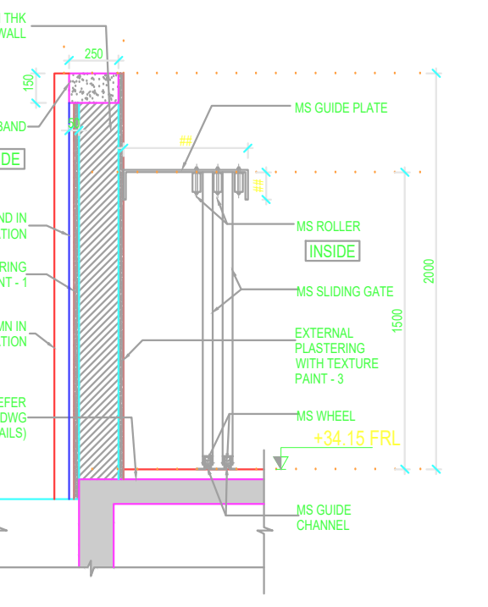
200MM THK BLOCK WALL
250
150
RC BAND
OUTSIDE
MS GUIDE PLATE
MS ROLLER
INSIDE
PLASTER BAND IN ELEVATION
EXTERNAL PLASTERING WITH TEXTURE PAINT - 1
MS SLIDING GATE
RC COLUMN IN ELEVATION
EXTERNAL PLASTERING WITH TEXTURE PAINT - 3
DRAIN SLAB (REFER STRUCTURAL DWG FOR DETAILS)
MS WHEEL
+34.15 FRL
MS GUIDE CHANNEL
1500
2000

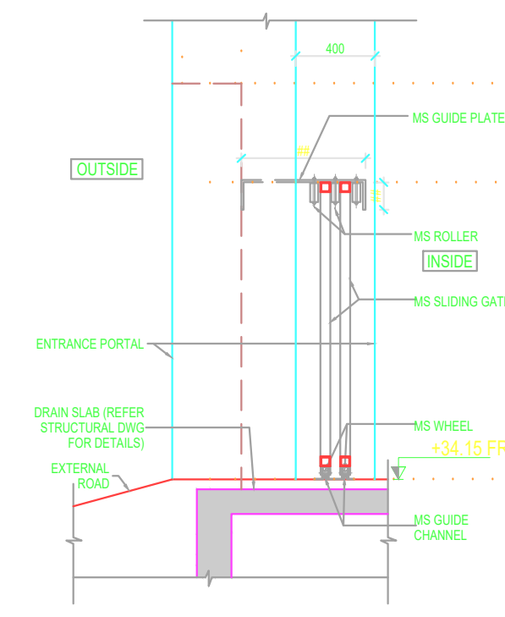
400
MS GUIDE PLATE
OUTSIDE
MS ROLLER
INSIDE
MS SLIDING GATE
ENTRANCE PORTAL
DRAIN SLAB (REFER STRUCTURAL DWG FOR DETAILS)
MS WHEEL
+34.15 FRL
EXTERNAL ROAD
MS GUIDE CHANNEL
1500
2000