


LOAD DIAGRAM

Nominal static vertical loads are indicated. Value within brackets include dynamic surload factor 1.25 for door leaf loads in open position. Includes items provided by ASSA ABLOY only.

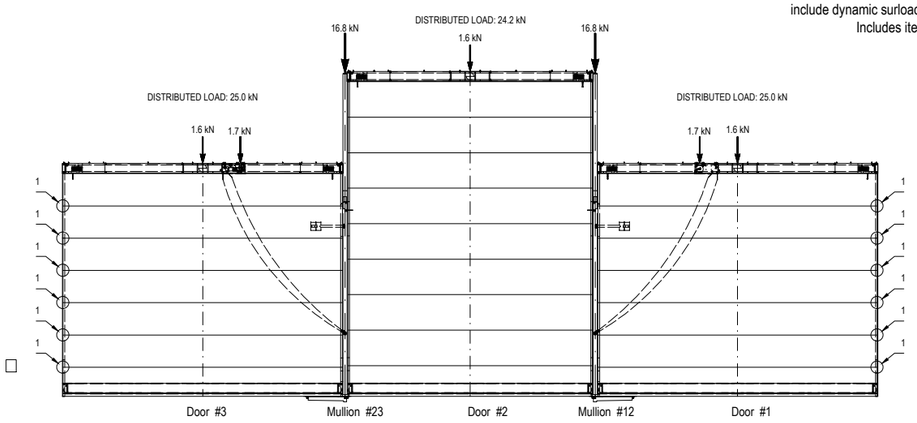


Exterior view, Door closed

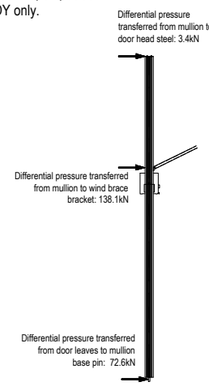


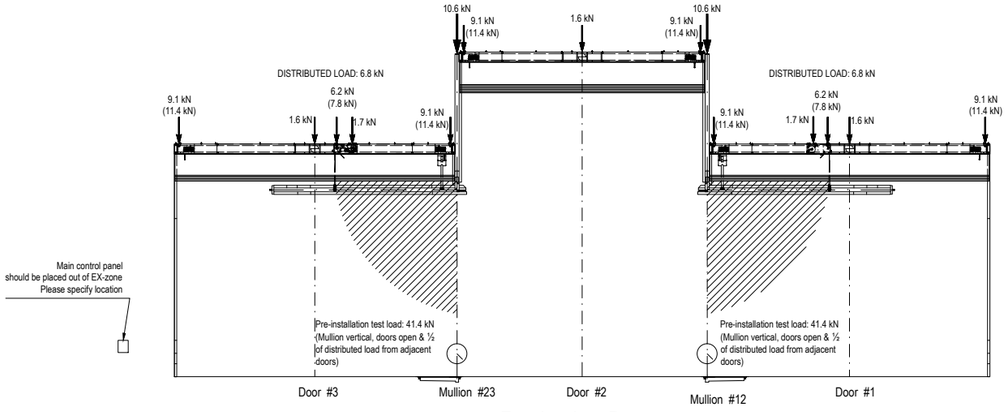


Exterior view, Door open

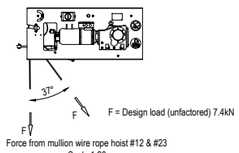


Force from mullion wire rope hoist #12 & #23
Scale 1:20

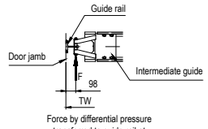

Force by differential pressure transferred to guide rail at each intermediate position. (located at pos 1)
F=12.6 kN

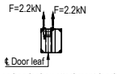

Load on header box attachment (each screw), due to wind load and door weight

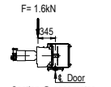

Section @ gear motor
Nord SK 973.1Z-112M/4
Scale 1:20

Steel building company in cooperation with door installing company must make a pre-installation load test on the structure, where the mullions are located, in order to simulate the vertical deflection of the structure that occurs when doors are installed. This vertical deflection figure will be used to determine the correct installation level of the mullions. Required material/equipment and personnel by others than ASSA ABLOY.

NOT INCLUDED IN DOOR SUPPLY:

1. Design and supply of all door supporting structural components.
2. Design and supply of all closure between door and adjacent steel.
3. Door jambs adjustable for overall door width and true to plumb.
4. Design and supply of coverage, such as roofing or enclosure, for door components at door head
5. Paint job after completed door installation.
6. Any frameworks being provided by ASSA ABLOY will be clearly indicated as "by ASSA ABLOY".

REQUIREMENTS ON BUILDING:

7. Door head support must be straight within 1/600 of span in the in/out direction and free from protrusions of any kind.
8. For a single door leaf, door head support should be horizontal and straight within 1/600 of span at distributed full door load.
9. Door side jambs must be smooth, straight and parallel, out of plumb must not exceed 2mm/m (total deviation at full length 5 mm) in any direction.
10. Any footings at bottom of jamb columns must not interfere with installation of guide rails at floor level.
11. At time of installation, finished floor, free from obstructions, out to a distance of 2 m on each side of door centreline must be available.

DOOR PROPERTIES:

12. The door is designed to withstand a differential pressure of 1.2kPa.
14. Mullions #12 & #23 and mullion pits are designed to allow for 59mm of downward deflection and 59mm of upward deflection due to external loads such as wind.
15. Guide rails, top- and intermediate beams in extruded aluminium with natural finish.
16. Environmental category: Megadoor standard
17. Bottom beams & Mullions carbon steel painted: Light grey (RAL7047)
18. Color of header box: BLACK (NCS 9000-N. RAL 9005)
17. Door header box enclosed on both sides .
18. Colored clamp strips on both sides: TBC
19. The door fabric is a UV stabilized, flame retardant, self-extinguishing, PVC coated polyester fabric with fire technical properties Euroclass C-s2, d0 (according to EN 13501-1:2007).

Colour of fabric: RED (NCS S2070-R, RAL 3001)
BLUE (NCS S3560-R80B, RAL 5005)
GREY (NCS 3500, RAL 7004)
WHITE (NCS 0500, RAL 9016)
TAN (NCS 2010-Y40R, RAL 1001)
WHITE ALUMINUM (RAL 9006)
GREEN (NCS 8010-G10Y, RAL 6009)
ANTHRACITE GREY (NCS 8005-B20G, RAL 7016)
TRANSLUCENT WHITE
(Please specify)

ELECTRICAL:

20. One main control panel provided of PLC type.
21. Control mode : Impulse up / Constant contact down.
22. Cables are included.
23. Back-up power socket & switch.
24. Audible & visual alarm.
25. Approx. size of main control panel: WxHxD (500mm x 600mmx250 mm),
26. Location of main control panel: Please specify location.
27. Aux. Voltage 24VDC
28. Power supply: 400V /3Ph /50Hz
29. Power: 15.0kW
30. Nom. current: 30.6A
31. Start. current: 45.0A
32. (max. allowed voltage drop at start: 5%)

BELT HOIST UNITS:#1. #2 & #3
SK 973.1Z-112M/4
75mm wide polyester belt . Rupture load 80kN/belt.

MULLION HOIST #12 & #23
LIDAN 0.7T/10 TB
Ø 8mm wire rope for normal operation. rupture load of 37.4 kN/rope.
Ø 8mm idling wire rope for arresting operation. rupture load of 37.4 kN/rope.

DOOR IDENTITY NUMBER: 84159001

INTERFACE DRAWING, ref. to drwng. no. 63651

DESIGNED: PL	SIZE: A1F	SCALE: 1:100	GMR Hyderabad
CODE: 84159	If not otherwise stated: Tolerances ISO 2768-m EN ISO 13920-B		India
ITEM NO			Megadoor 40000 x 14000 / 9000
DATE: 2017-03-31	Cutting class: ISO 9013-442		Load diagram & Notes
ASSA ABLOY	Weld class: ISO 5817-C Surface finish: Smooth raw surface	DRAWING NO: 63652	REVISION: --

This document is the property of ASSA ABLOY Entrance Systems AB and shall not be reproduced or disclosed to a third party or used for any other unauthorized purpose.