




SECTION–A–A

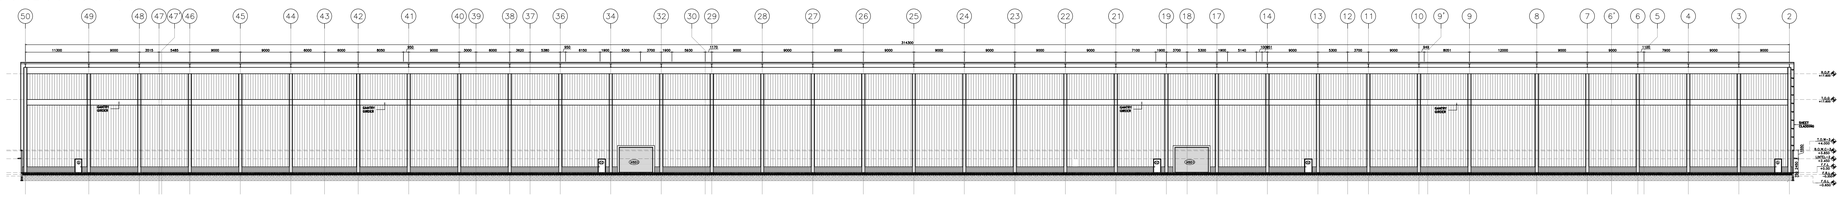

SECTION–C–C

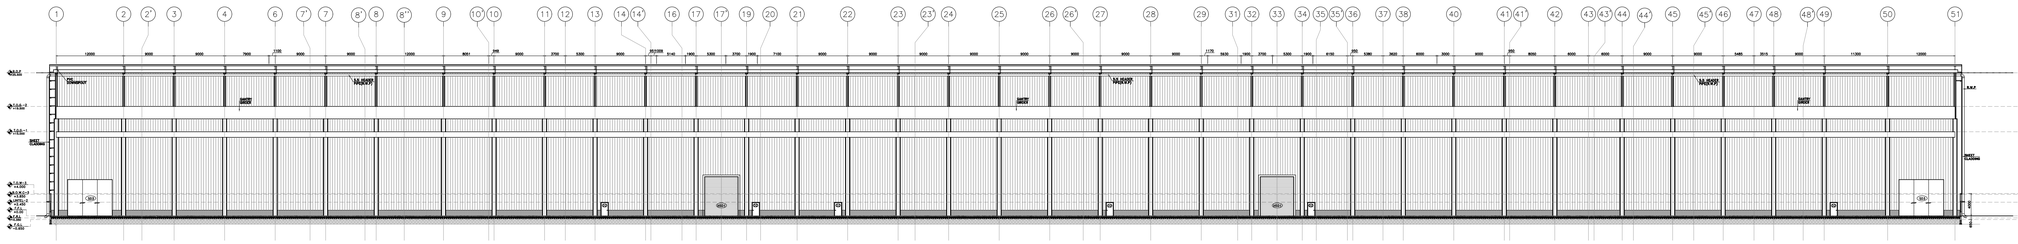

SECTION–B–B

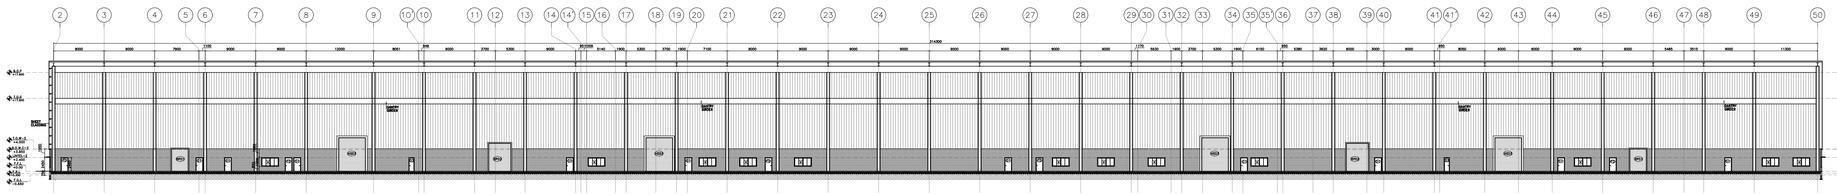

SECTION–D–D

## REFERENCE DRAWINGS

| SR.NO. | DRAWING TITLE | DRAWING NO. |
|---|---|---|

NOTE :-

1. DO NOT SCALE THE DRAWING. REFER TO WRITTEN DIMENSIONS ONLY. ALL MEASUREMENTS MUST BE CHECKED AND VERIFIED AT SITE. ANY DISCREPANCY FOUND,TO BE NOTIFIED TO THE CONSULTING ENGINEER BEFORE EXECUTION.
2. ALL DIMENSIONS ARE IN MM.& ALL LEVELS ARE IN METERS UNLESS OTHERWISE SPECIFIED.
3. F.G.L & F.R.L AS PER SITE ROAD LAYOUT PLAN.

ABBREVATION :-

| | |
|---|---|
| N.G.L | = NATURAL GROUND LEVEL |
| F.G.L. | = FINISHED GROUND LEVEL |
| F.R.L. | = FINISHED ROAD LEVEL |
| F.F.L. | = FINISHED FLOOR LEVEL |
| T.O.C. | = TOP OF CONCRETE |
| T.O.W. | = TOP OF WALL |
| B.O.C. | = BOTTOM OF CONCRETE |
| B.O.W.C | = BOTTOM OF WALL CLADDING |
| B.O.P | = BOTTOM OF PORTAL |
| T.O.T | = TOP OF CABLE TRAY |
| T.O.G | = TOP OF GANTRY |
| T.O.B | = TOP OF BEAM |
| T.O.F | = TOP OF FASCIA |

LEGEND :-

230MM THK. BRICK MASONRY WALL

115MM THK. BRICK MASONRY PARTITION WALL

KEY - PLAN :

OPENING SCHEDULE GROUND FLOOR

| TYPE | CLEAR SIZE | WITH STONE FRAME SIZE | FINISHED SILL | FINISHED LINTEL | NOS. | DESCRIPTION |
|---|---|---|---|---|---|---|
| ROLLING SHUTTER | | | | | | |
| RS1 | 6000X6000 | – | – | 6000 | 04 | MOTORIZED MS ROLLING SHUTTER |
| RS3 | 5000X5000 | – | – | 5000 | 07 | MOTORIZED MS ROLLING SHUTTER |
| RS4 | 4000X5000 | – | – | 5000 | 02 | MOTORIZED MS ROLLING SHUTTER |
| HSD1 | 6000X4500 | – | – | 4500 | 02 | HIGH SPEED DOOR |
| HSD2 | 5000X5000 | – | – | 5000 | 02 | HIGH SPEED DOOR |
| HSD3 | 4800X6000 | – | – | 7000 | 04 | HIGH SPEED DOOR |
| HSD4 | 5200X6200 | – | – | 7200 | 03 | HIGH SPEED DOOR |
| HSD5 | 6200X6800 | – | – | 7700 | 01 | HIGH SPEED DOOR |
| SD1 | 11000X15000 | – | – | 15000 | 02 | SLIDING DOOR WITH MAN ENTRY |
| SD2 | 5000X5000 | – | – | 5000 | 02 | SLIDING DOOR WITH MAN ENTRY |
| SD3 | 8000X6500 | – | – | 6500 | 04 | SLIDING DOOR WITH MAN ENTRY |
| RPD1 | 3000X4000 | – | – | 4000 | 02 | RAPID DOOR |
| RPD2 | 4000X5000 | – | – | 5000 | 02 | RAPID DOOR |
| DOOR | | | | | | |
| FD | 1200X2400 | 1400X2450 | – | 2450 | 23 | EMERGENCY FIRE EXIT DOOR |
| D1 | 1200X2400 | – | – | – | 11 | STEEL DOOR WITH VISION PANEL (IN PEB) |
| D2 | 1200X2400 | 1300X2450 | – | 2450 | 21 | STEEL DOOR WITH VISION PANEL |
| D3 | 900 X 2400 | 1000X2450 | – | 2450 | 10 | STEEL DOOR WITHOUT VISION PANEL |
| D4 | 750 X 2100 | 850X2150 | – | 2150 | 12 | STEEL DOOR WITHOUT VISION PANEL |
| WINDOW | | | | | | |
| W | 3000X1450 | 3100X1550 | 900 | 2450 | 48 | ALUMINUM SLIDING WINDOW STONE FRAME ON FOUR SIDE |
| VENTILATION | | | | | | |
| V | 3000 X 600 | – | 1750 | – | 56 | ALUMINUM FIX GLASS WITH EXHAUST FAN(IN PEB) |
| V1 | 1200 X 600 | 1300 X 700 | 1750 | 2450 | 14 | ALUMINUM FIX GLASS WITH EXHAUST FAN |

| REV. | DATE | DESCRIPTION | DRN. | CHK. | APP. | PRN. |
|---|---|---|---|---|---|---|
| R0 | 26-12-25 | ISSUED FOR INFORMATION | JP | GJT | GJT | EMAIL |
| R0 | 05-12-25 | ISSUED FOR INFORMATION | JP | GJT | GJT | EMAIL |

ISSUED FOR

☑ INFORMATION ☐ APPROVAL ☐ CONSTRUCTION

☐ ENQUIRY ☐ ORDER ☐ REVIEW

CLIENT : **TRANSFORMER FACT (45000 MVA) FOR CG POWER AT JAHANGIRPURA**

PROJECT : 45000 MVA PLANT

CONSULTANT : SHAH & TALATI Design & Engineering

9th FLOOR, KIRTI TOWER, TILAK ROAD, VADODARA-390001, GUJARAT, INDIA.
PHONE : +91-265-2440701 / 2440726
E-MAIL : design@shahntalati.com
WEBSITE : www.shahntalati.com

PROJECT NO. :- **2537**

TITLE :- **FACTORY SECTIONS**

| | | | |
|---|---|---|---|
| DRAWN BY | JANKI | | R0 26 12 25 |
| CHECKED BY | GJT | | |
| APPROVED BY | GJT | | |
| DRAWING NO. | **2537-FAC-A02-SH1-A1-R0** | | SHEET 1 OF 1 |
| SCALE : 1:600 | | | |

THIS DOCUMENT OR DRAWING IS THE PROPERTY OF SHAH & TALATI CONSULTING ENGINEERS AND SHALL NOT, UNDER ANY CIRCUMSTANCES, BE TOTALLY OR PARTIALLY, DIRECTLY OR INDIRECTLY, TRANSFERRED, REPRODUCED, COPIED, DISCLOSED OR USED WITHOUT SHAH & TALATI'S PRIOR WRITTEN CONSENT.

A1