

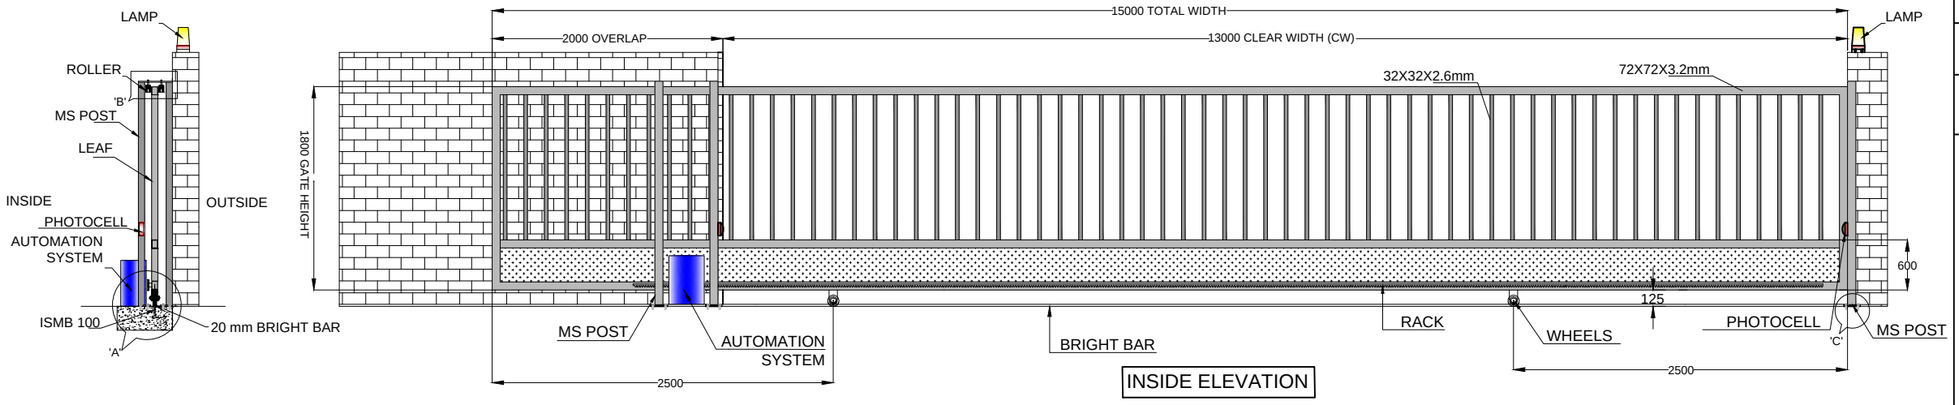


INSIDE ELEVATION

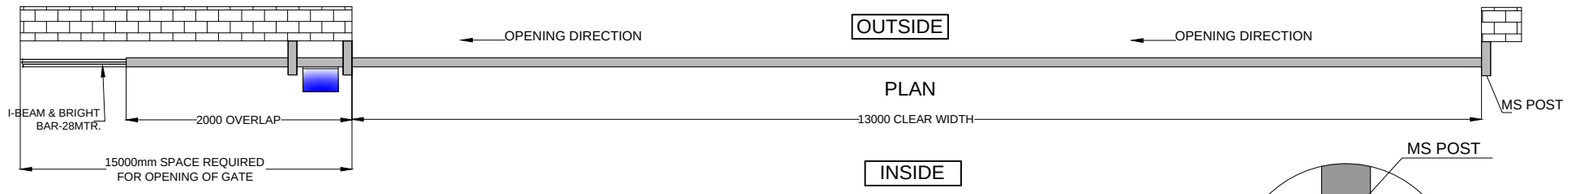


PLAN


INSIDE

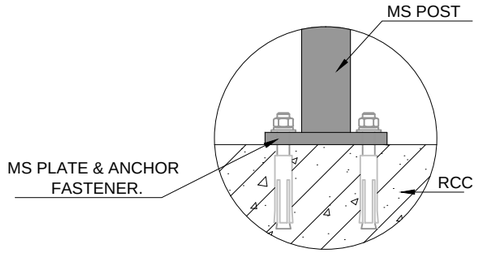

DETAIL VIEW OF C
(FIXING DETAILS)

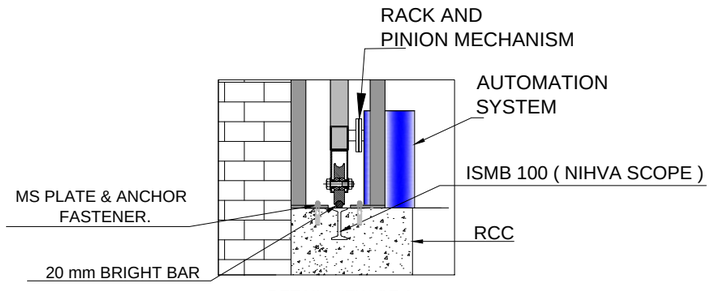

DETAIL VIEW OF A

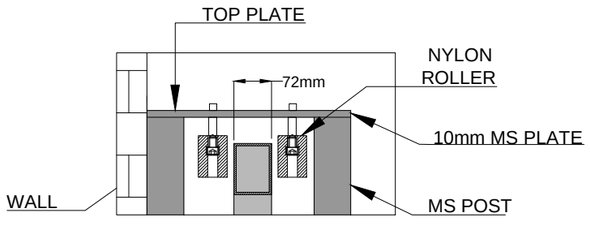

DETAIL VIEW OF B

SR NO	TUBE SPECIFICATION	
1	72X72X3.2mm MS TUBE	OUTER FRAME
2	32X32X2mm MS TUBE	INNER PATTERN
3	GAP BETWEEN TUBES	150mm
4	MS SHEET	MS SHEET
5	72X72X3.2mm MS TUBE	FOR POST

TOLERANCE:- ± 10mm

CLEAR WIDTH (CW)	CLEAR HEIGHT (CH)	QUANTITY
13000mm	1800mm	1 NOS

RAL CODE	RAL COLOR
RAL 9002	GREY WHITE

REV. NO	NAME	DATE	DESCRIPTION
R02	SURAJ	20-11-18	1.OPENING AS PER CLIENT SHOP LAYOUT DRAWING
R01	SURAJ	13-11-18	1.CHANGE FOR SPACE REQUIRED FOR OPENING OF GATE 2.BEAM & BRIGHT BAR SIZE DETAILS CHANGED.

DIMENSION :

CLEAR WIDTH	CLEAR HEIGHT	QUANTITY
13000mm	1800mm	1 NOS

MATERIAL: MS

THICKNESS :

NOTE-
1. ALL REQUIRED CIVIL WORK WILL BE IN CLIENTS SCOPE.
2. ONE COAT OF RED OXIDE & TWO COAT OF APPROVED RAL SHADE WILL BW GIVEN TO THE GATE
3. IN NECESSARY GATE LEAF WILL BE IN TWO PART FOR TRANSPORTATION AND ILL BE WELDED TOGETHER ON SITE

NIHVA TECHNOLOGIES PVT. LTD.
NIHVA TECHNOLOGIES PVT. LTD. PUNE
Email:- info@nihva.com
Website:- www.nihva.com
TEL :020 66304033

TITLE:

AUTOMATIC SINGLE LEAF SLIDING GATE

CLIENT'S APPROVAL :

CLIENT - INOX

PROJECT -

SITE LOCATION -CHAKAN

DWG. NO. : NIHVA/18-19/0166 /R02 | REV. : 02

SCALE: NTS | WT: | SHEET:1 OF 1

DRAWN	SURAJ		DATE: 03-11-18
CHECK	PRADEEP		DATE: 03-11-18
APPROVED	R.D		DATE: 03-11-18

IF ANY QUERIES CONTACT:- design@nihva.com

NOTE: ALL DIMENSIONS ARE IN mm

THIS DRAWING & DESIGN IS THE PROPERTY OF NIHVA TECHNOLOGIES. NOT TO BE SOLD OR COPIED TO ANY OTHER CONCERN.